




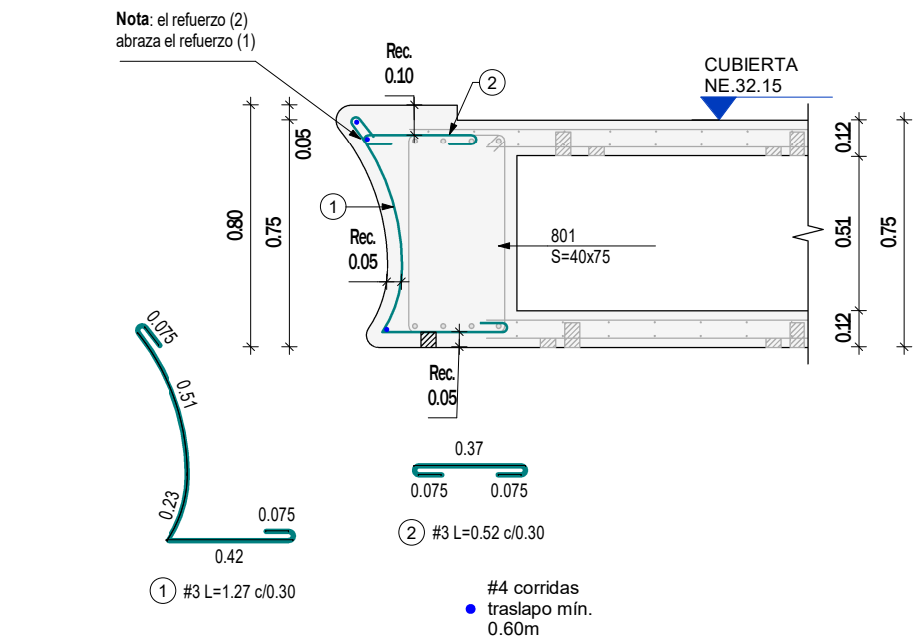


CORTE 1 - 1
Escala 1 : 25

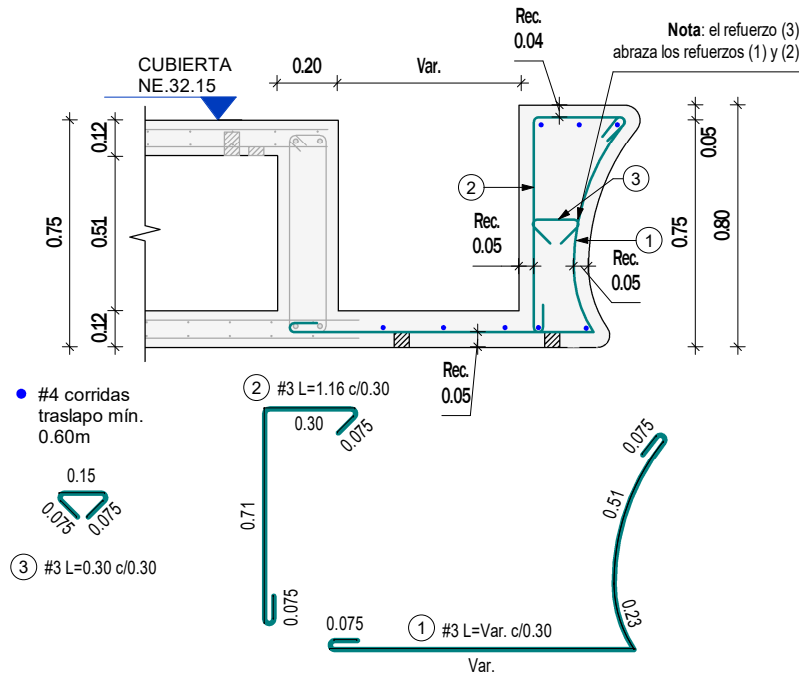


CORTE 2 - 2
Escala 1 : 25

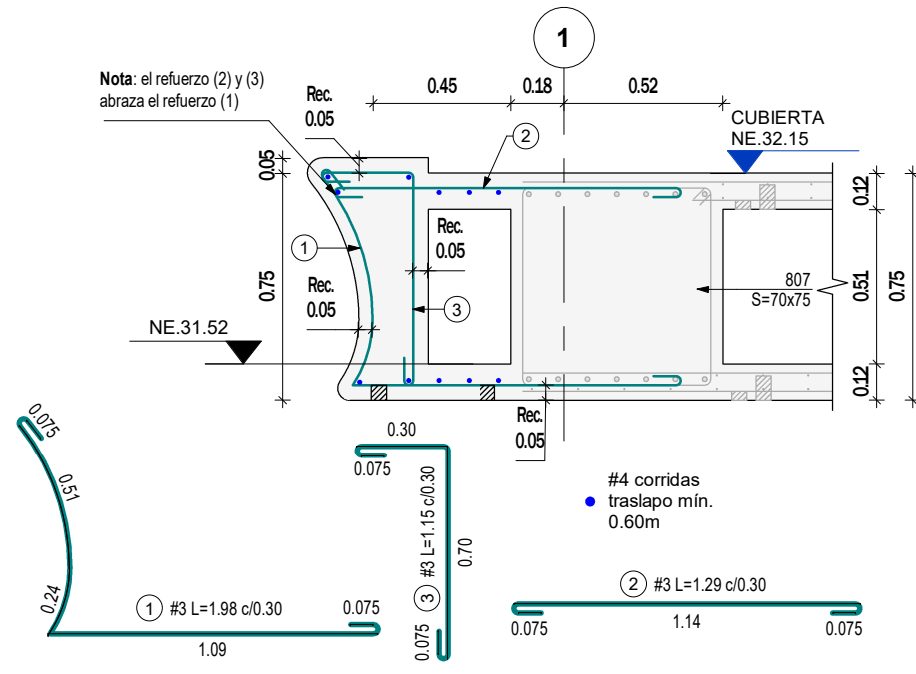


CORTE 4 - 4
Escala 1 : 25

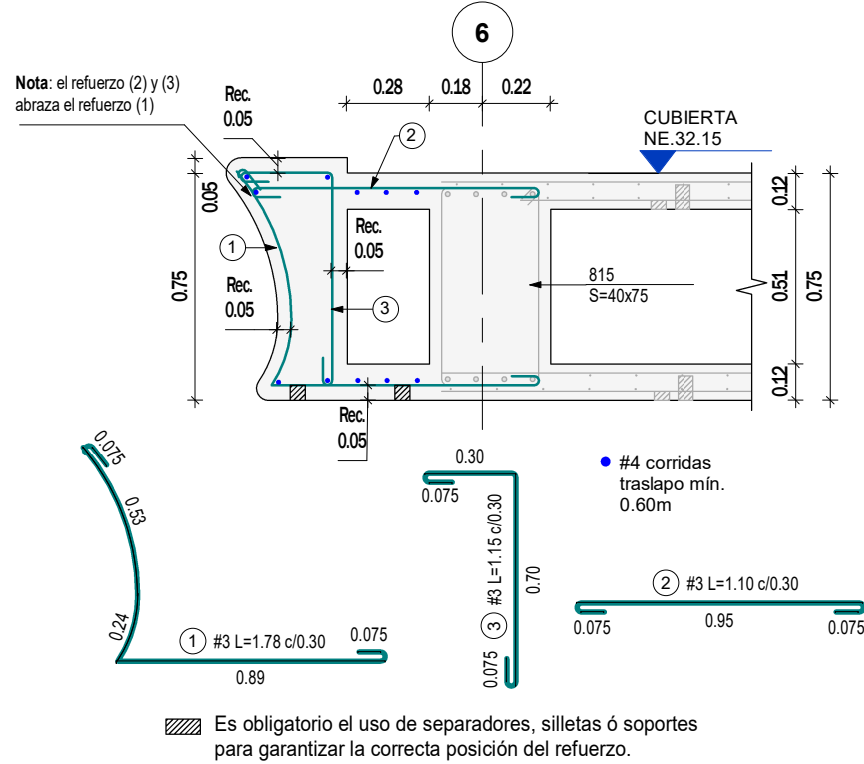


CORTE 5 - 5
Escala 1 : 25

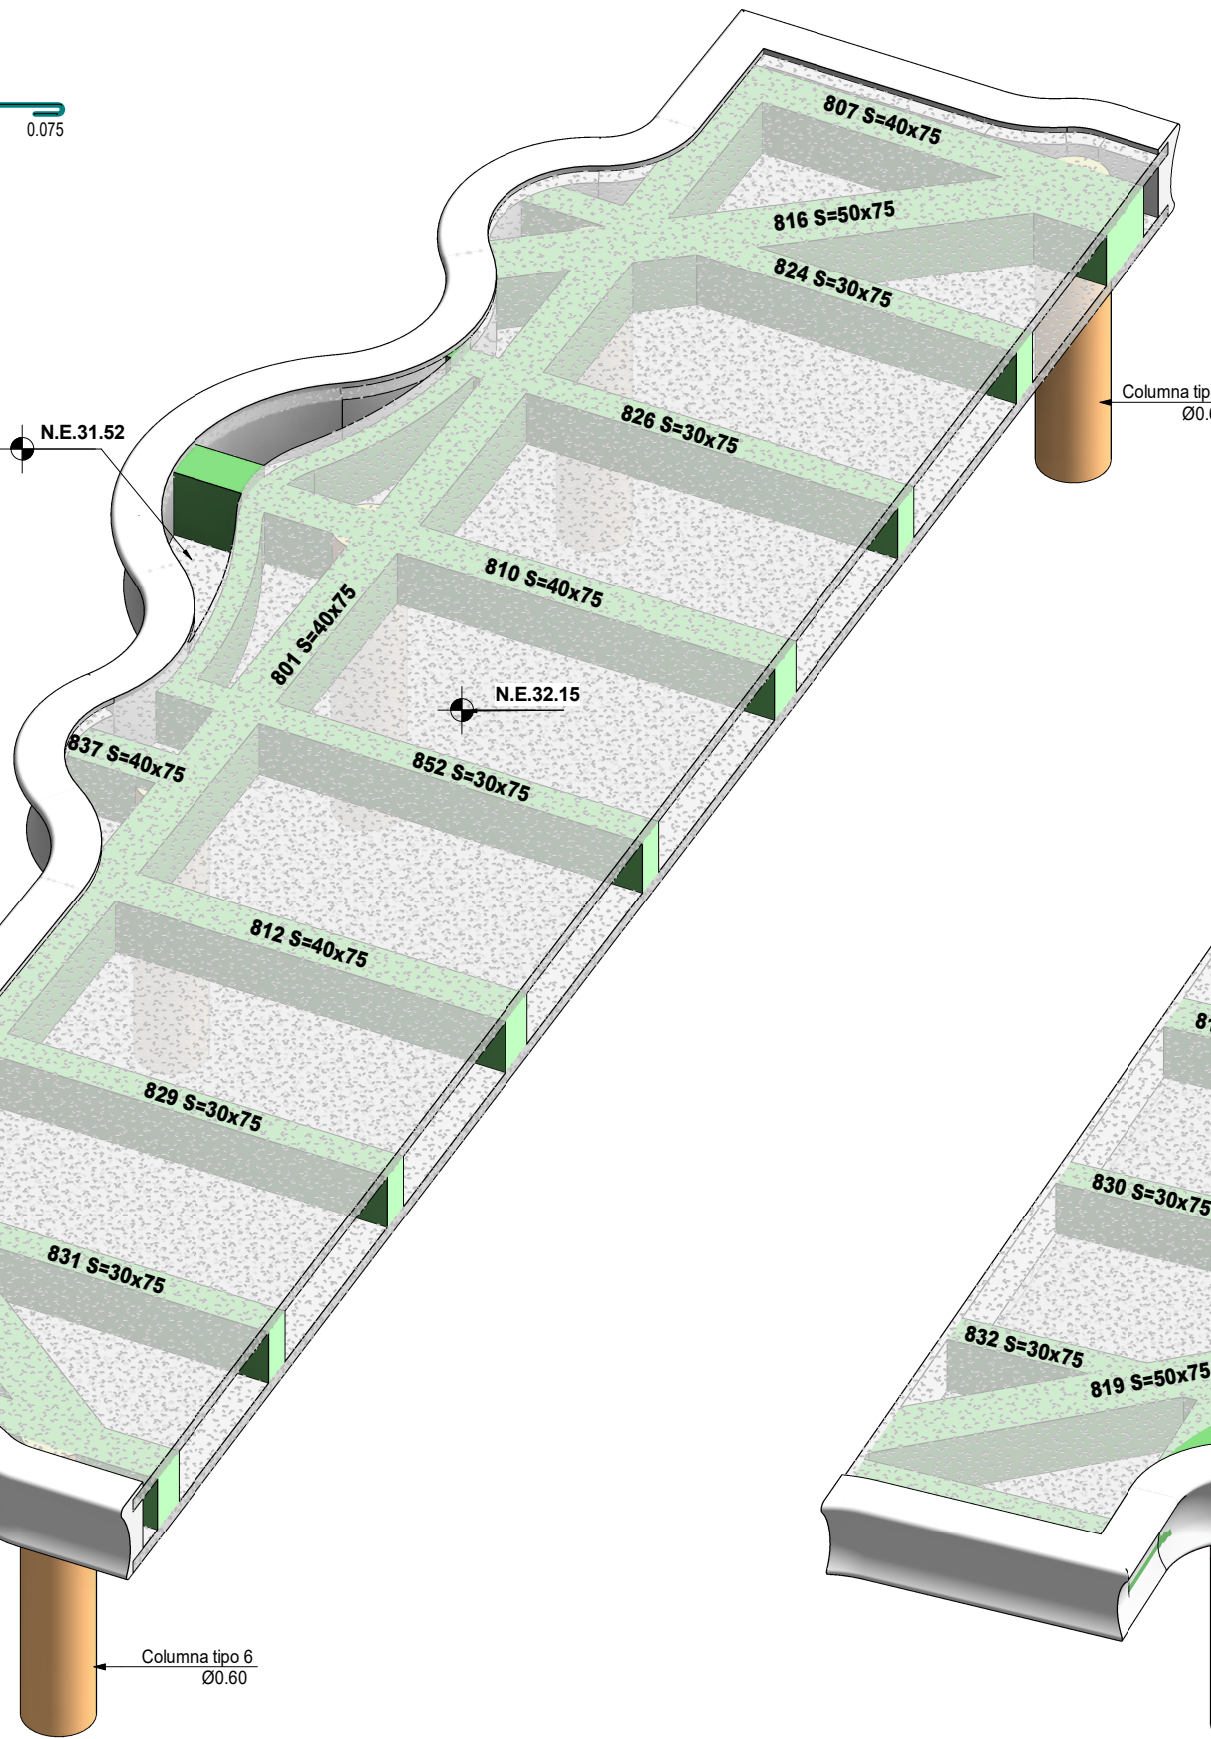


ESQUEMA 3D CUBIERTA DE BALCON COSTADO SUR CUBIERTA
Sin escala

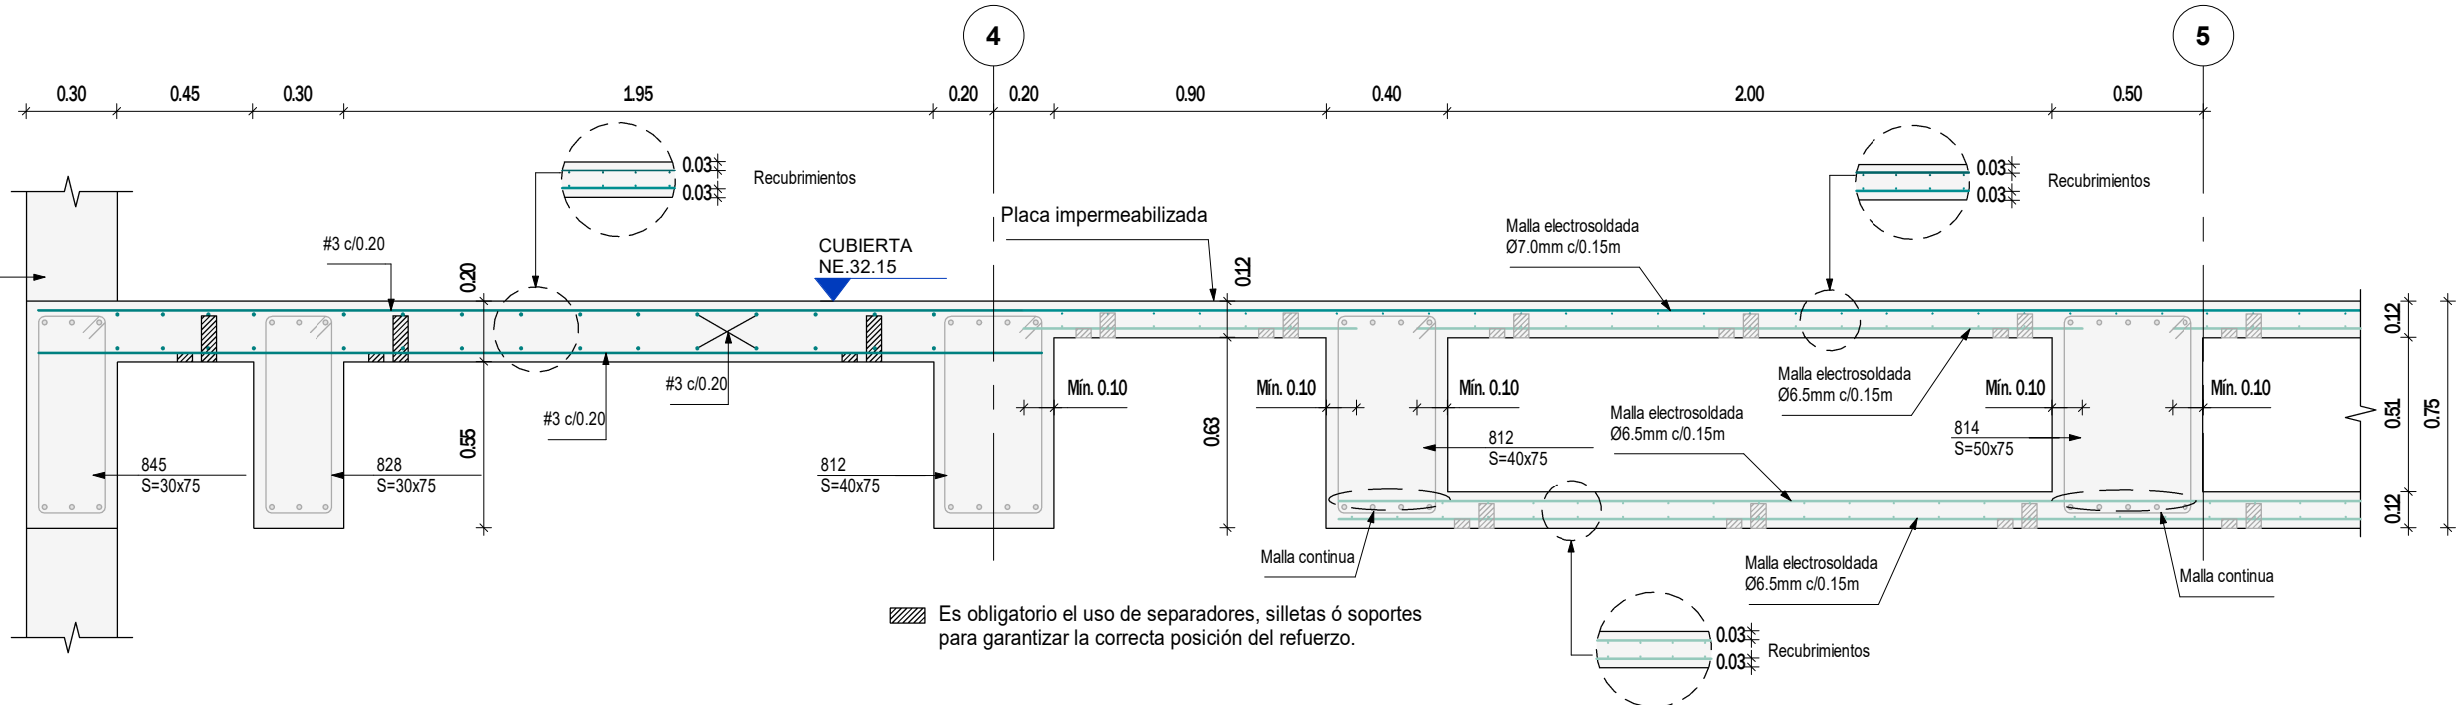

CORTE 3 - 3
Escala 1 : 25

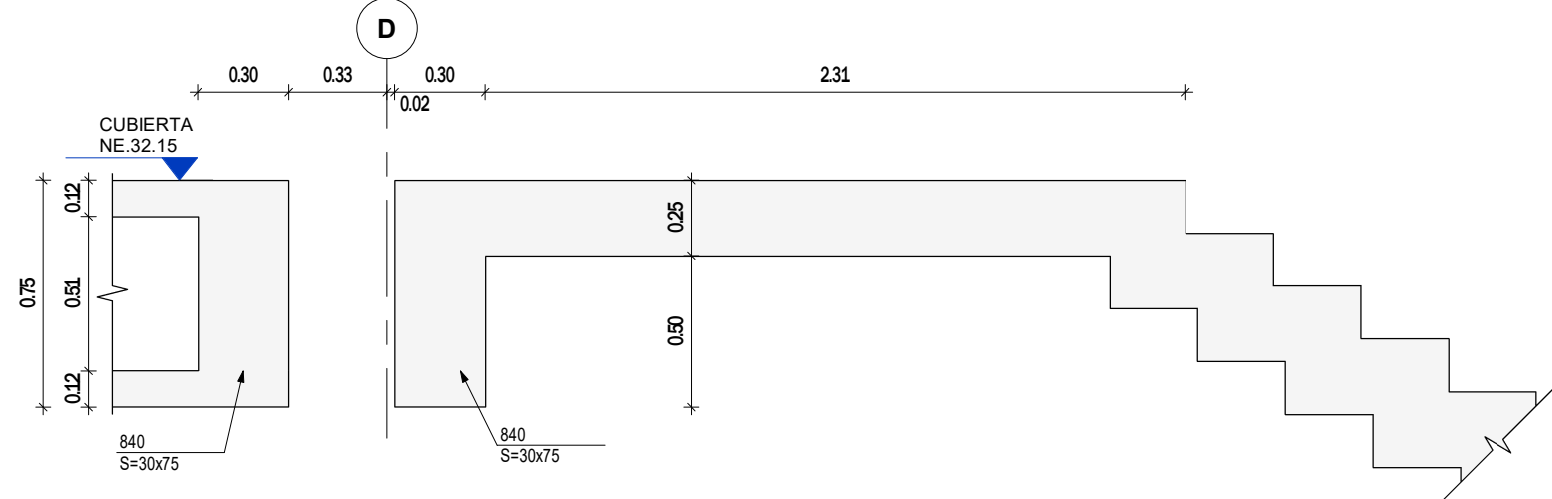

CORTE 6 - 6
Escala 1 : 25

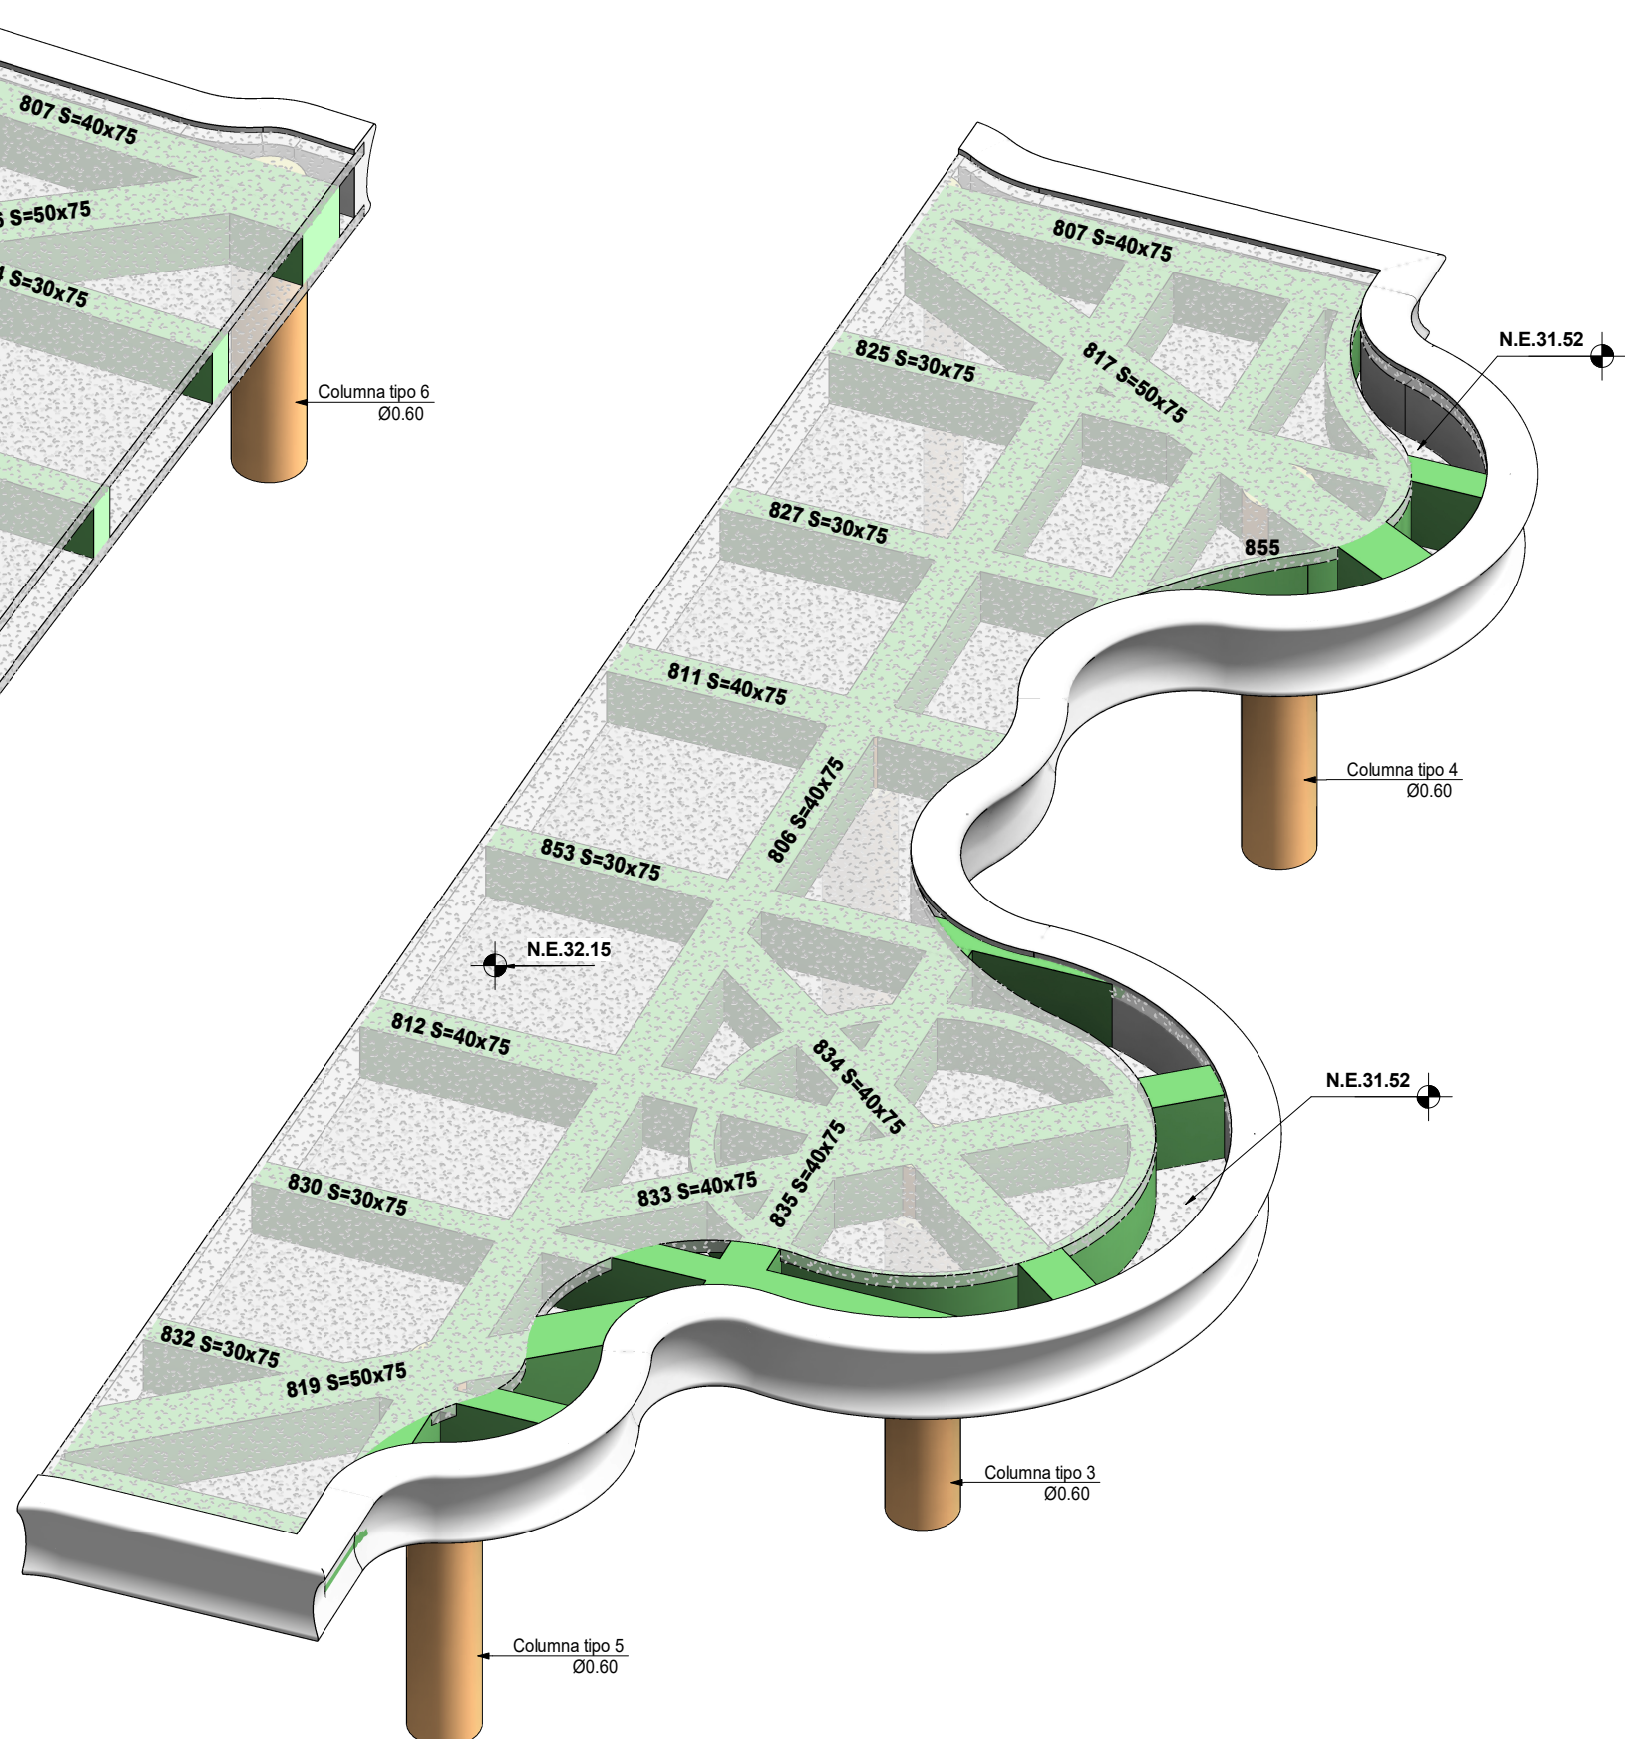

ESQUEMA 3D CUBIERTA DE BALCON COSTADO NORTE CUBIERTA
Sin escala

NOTAS

1. Ver detalles generales en PL N° 01.02 y 01.03
2. Ver planta de cubierta en PL N° 14.00

VERSIÓN :

0

PLANO N°

14.01

Aycardi
Estructural

GERENTE DE PROYECTO

LUIS ENRIQUE AYCARDI F.
MAT. 2520212794 CND

INGENIERO

DANIEL E. QUICANO C.

MODELADOR

PAULA ANDREA MONTOYA RENDÓN

MODIFICACIONES

FECHA

Emisión Inicial	21-11-2025

HUMANISE STUDIO

EAN-0519- AES-01-EST

Calle 71 #9-84

CORTES Y ESQUEMAS 3D CUBIERTA

EAN-0519- AES-01-EST-CUB-PL-573 14.01

REVISOR ESTRUCTURAL

JULIO CESAR SANMIGUEL CAMACHO
MAT. 25202-57738 CND

PLANO N°

14.01

VERSIÓN :

0