


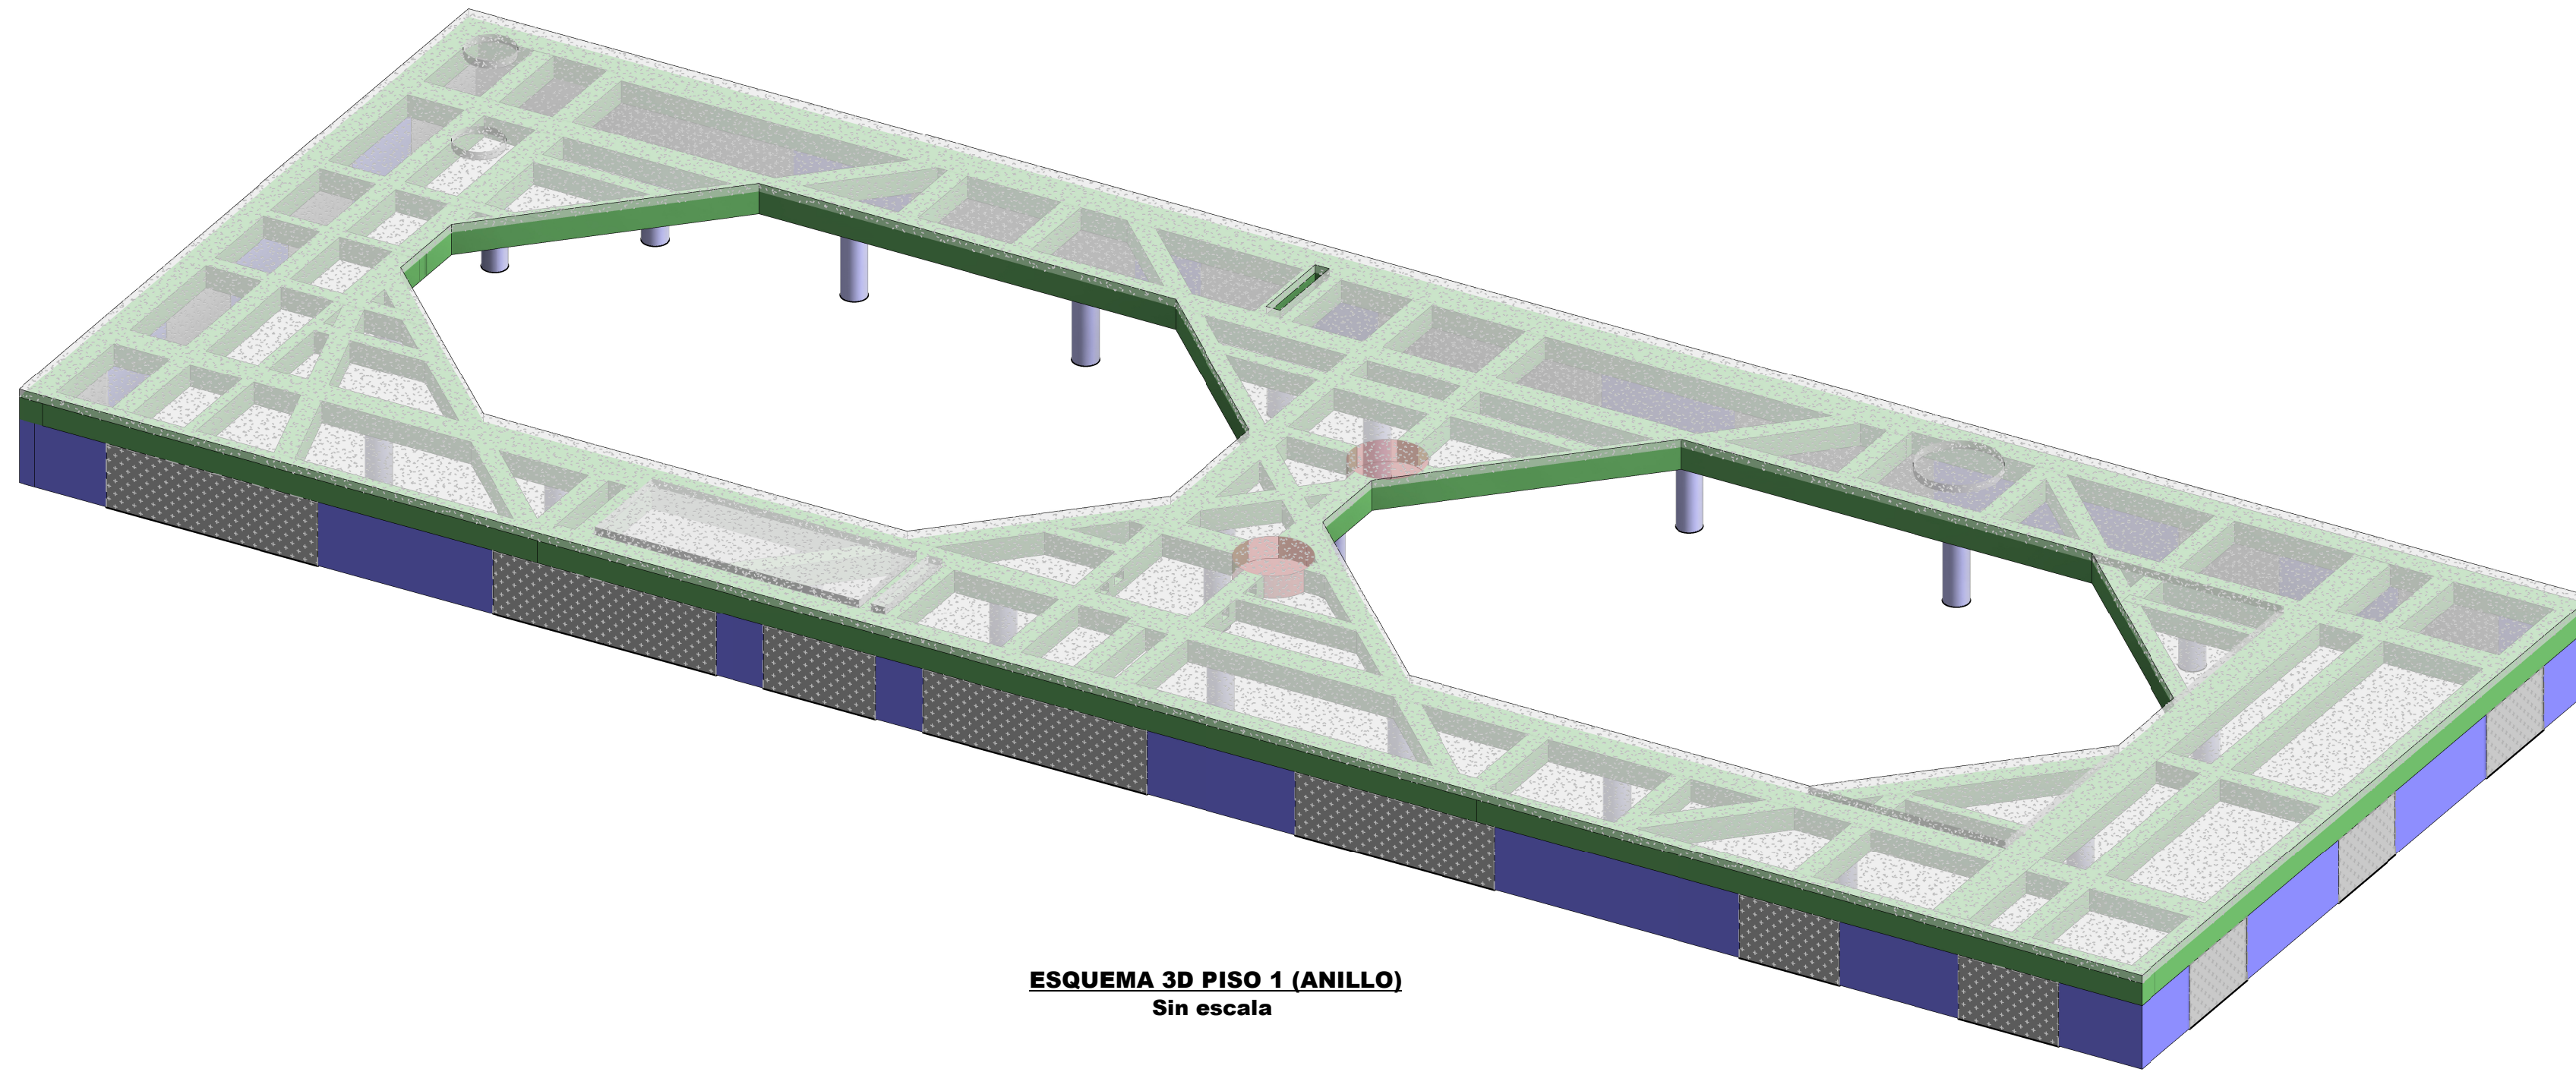

**NOTAS**

1. Ver detalles generales en PL N° 01.02 y 01.03
2. Ver planta de piso 1 etapa 1 (anillo) en PL N° 07.00

**CONCRETO**

$f'c=35$  MPa  
 $f'c=350$  kg/cm<sup>2</sup>  
 $f'c=5000$  psi

PLANO N° **07.01**

VERSIÓN : **0**



GERENTE DE PROYECTO  
**LUIS ENRIQUE AYCARDI F.**  
MAT. 2520212794 CND

INGENIERO  
**DANIEL E. QUICANO C.**

MODELADOR  
**PAULA ANDREA MONTOYA RENDÓN**

| MODIFICACIONES  | FECHA      |
|-----------------|------------|
| Emisión Inicial | 21-11-2025 |
|                 |            |
|                 |            |
|                 |            |

**HUMANISE STUDIO**

**EAN-0519- AES-01-EST**

Calle 71 #9-84

**CORTES Y ESQUEMA 3D PISO 1  
ETAPA 1 (ANILLO)**


EAN-0519- AES-01-EST-N01-PL-526 07.01

REVISOR ESTRUCTURAL  
**JULIO CESAR SANMIGUEL CAMACHO**  
MAT. 25202-57738 CND


PLANO N° **07.01**

VERSIÓN : **0**


**ESQUEMA 3D PISO 1 (ANILLO)**  
**Sin escala**

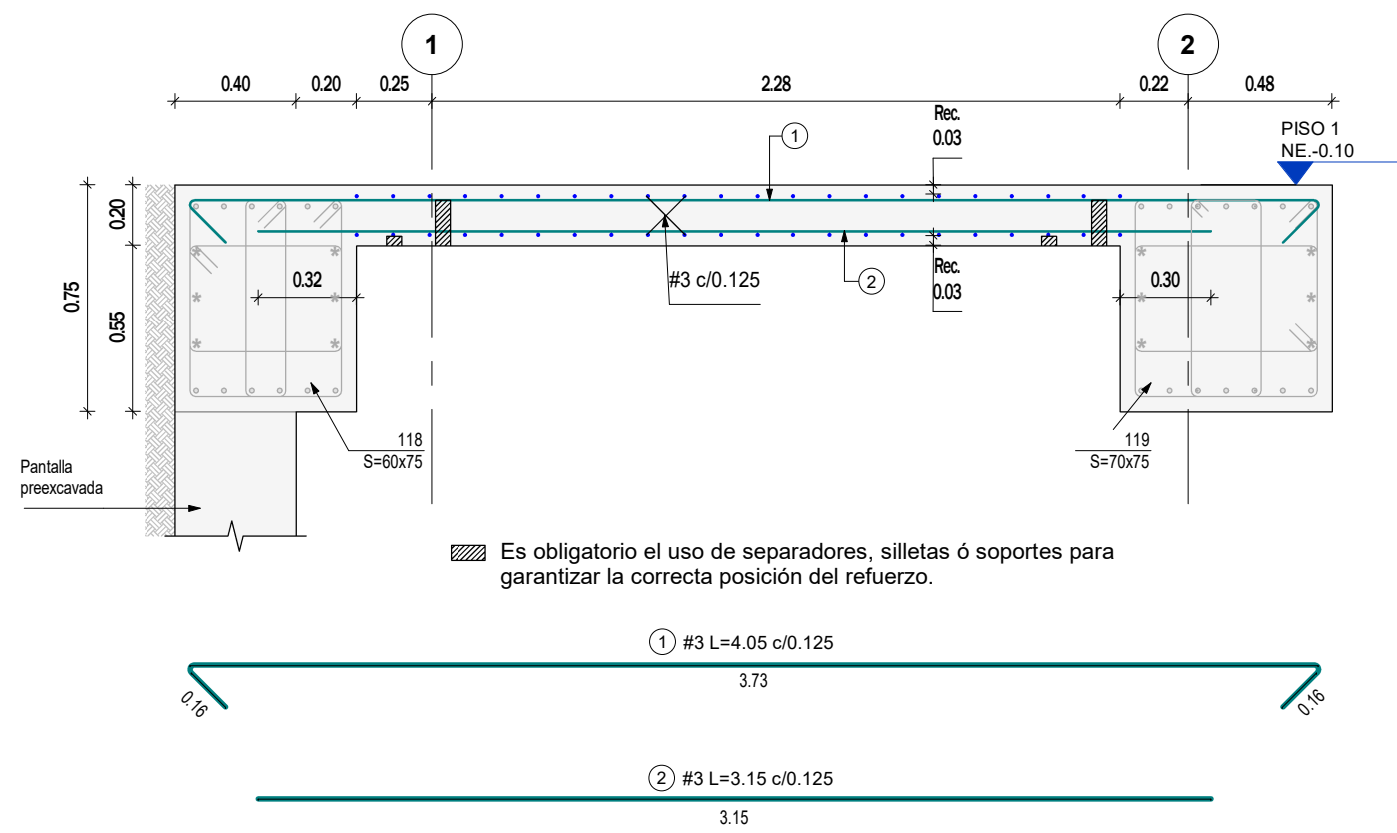


**CORTE 1 - 1**  
**Escala 1 : 25**

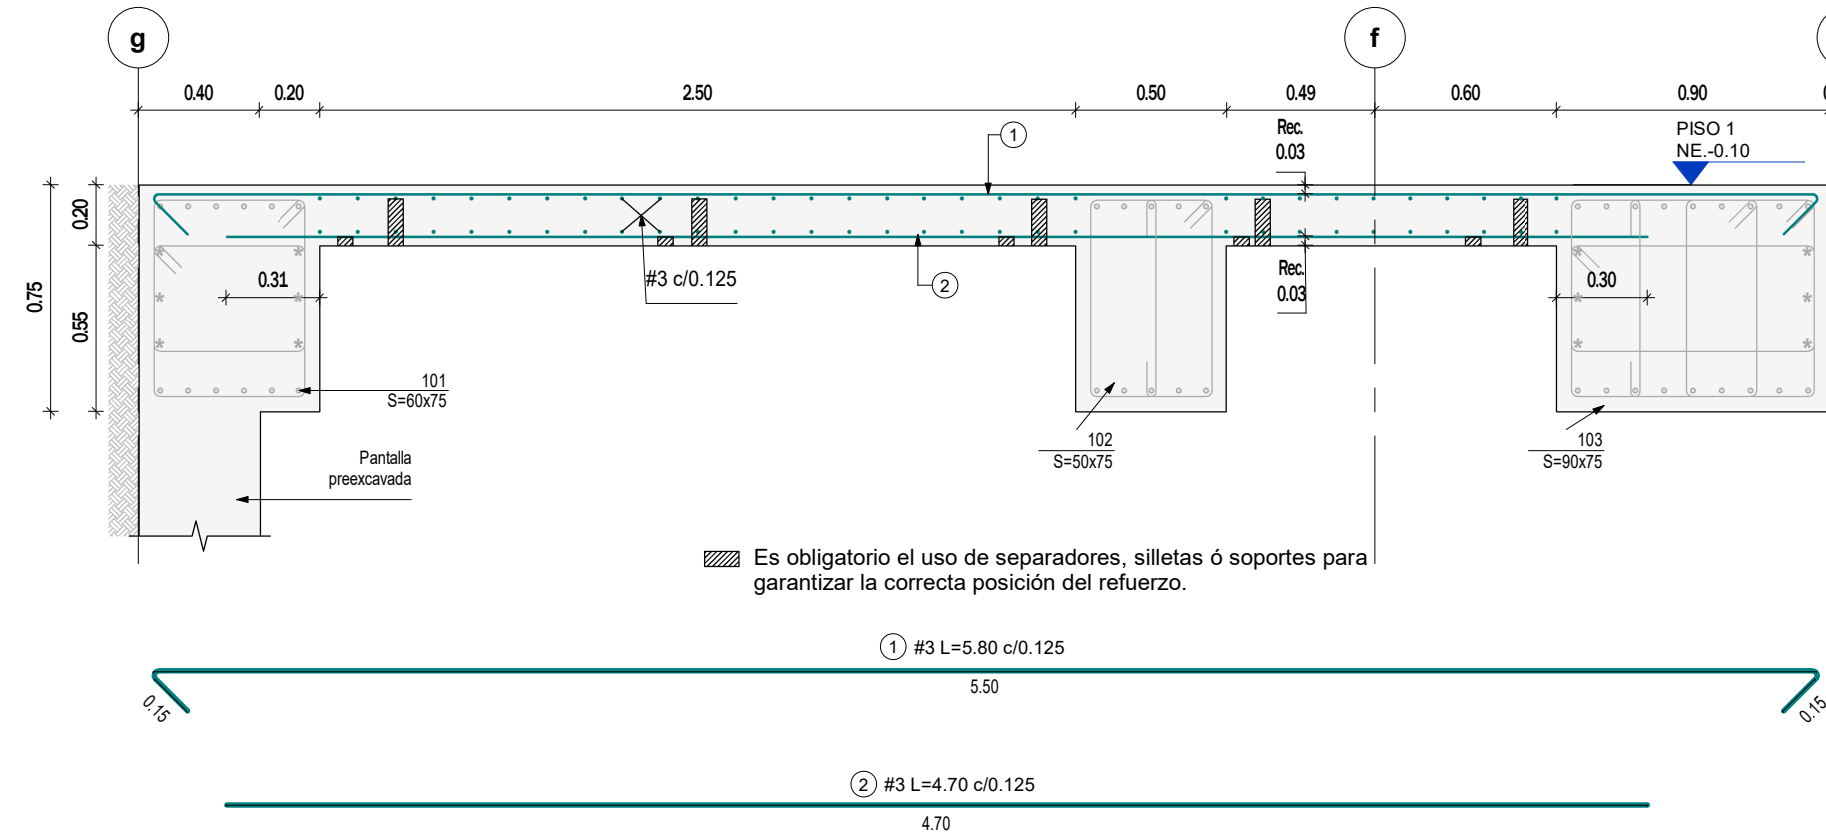


**CORTE 2 - 2**  
**Escala 1 : 25**

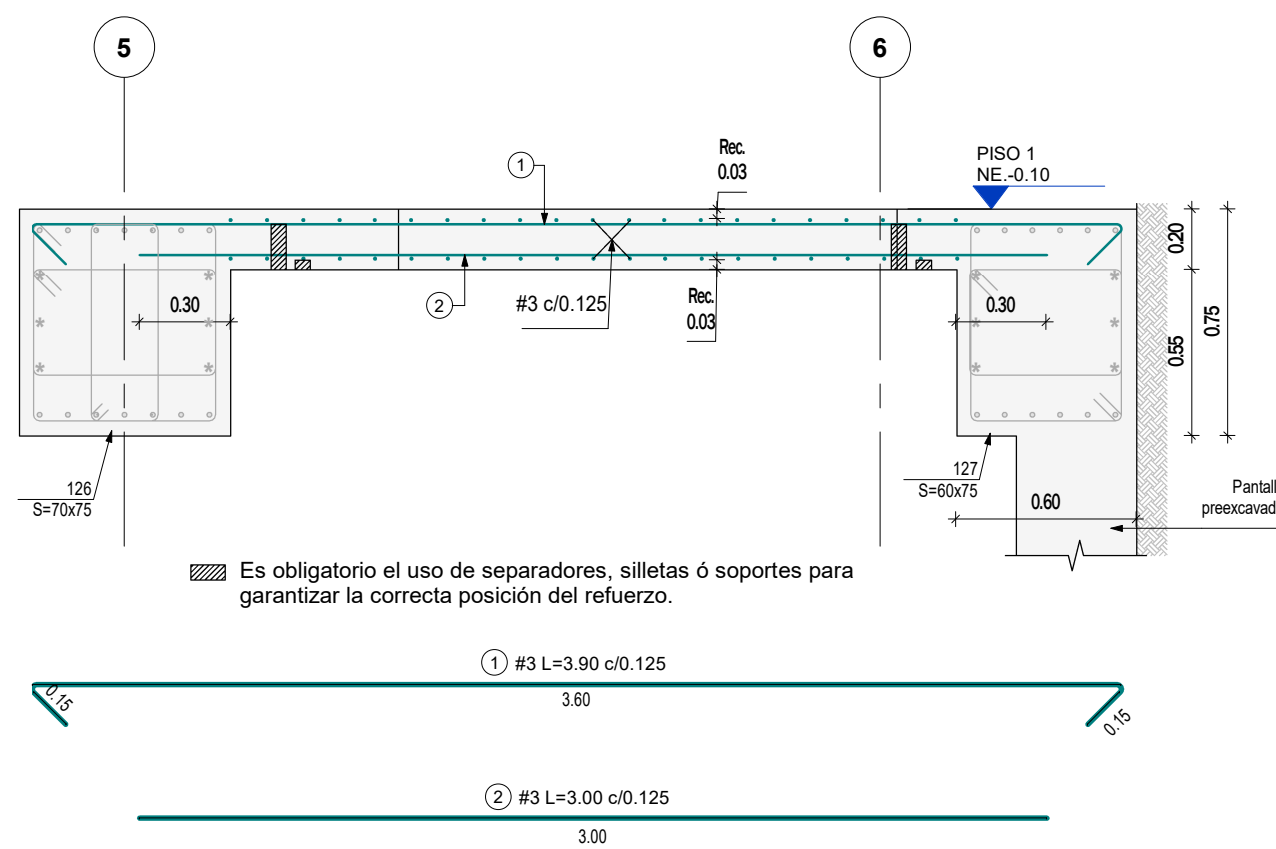

**CORTE 3 - 3**  
**Escala 1 : 25**

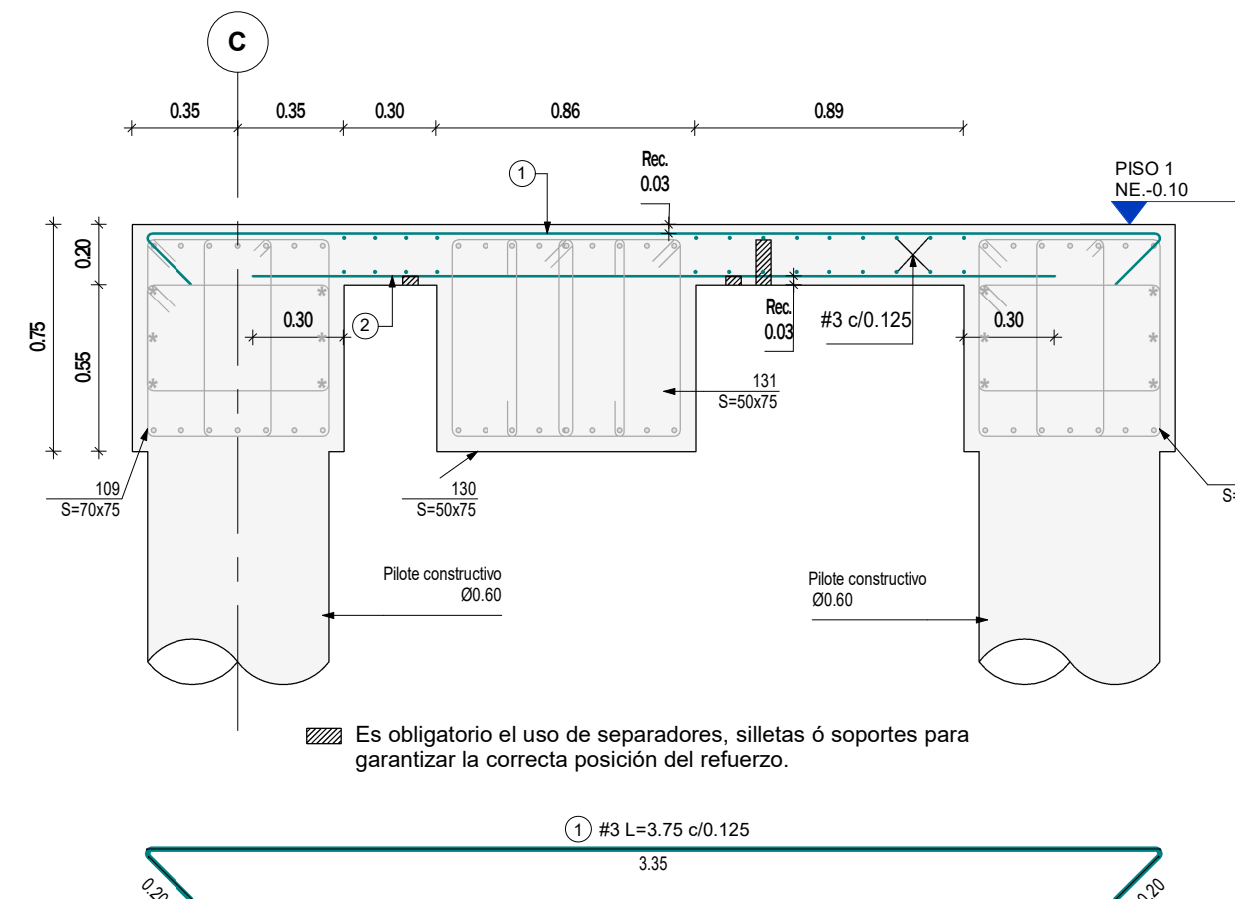

**CORTE 4 - 4**  
**Escala 1 : 25**

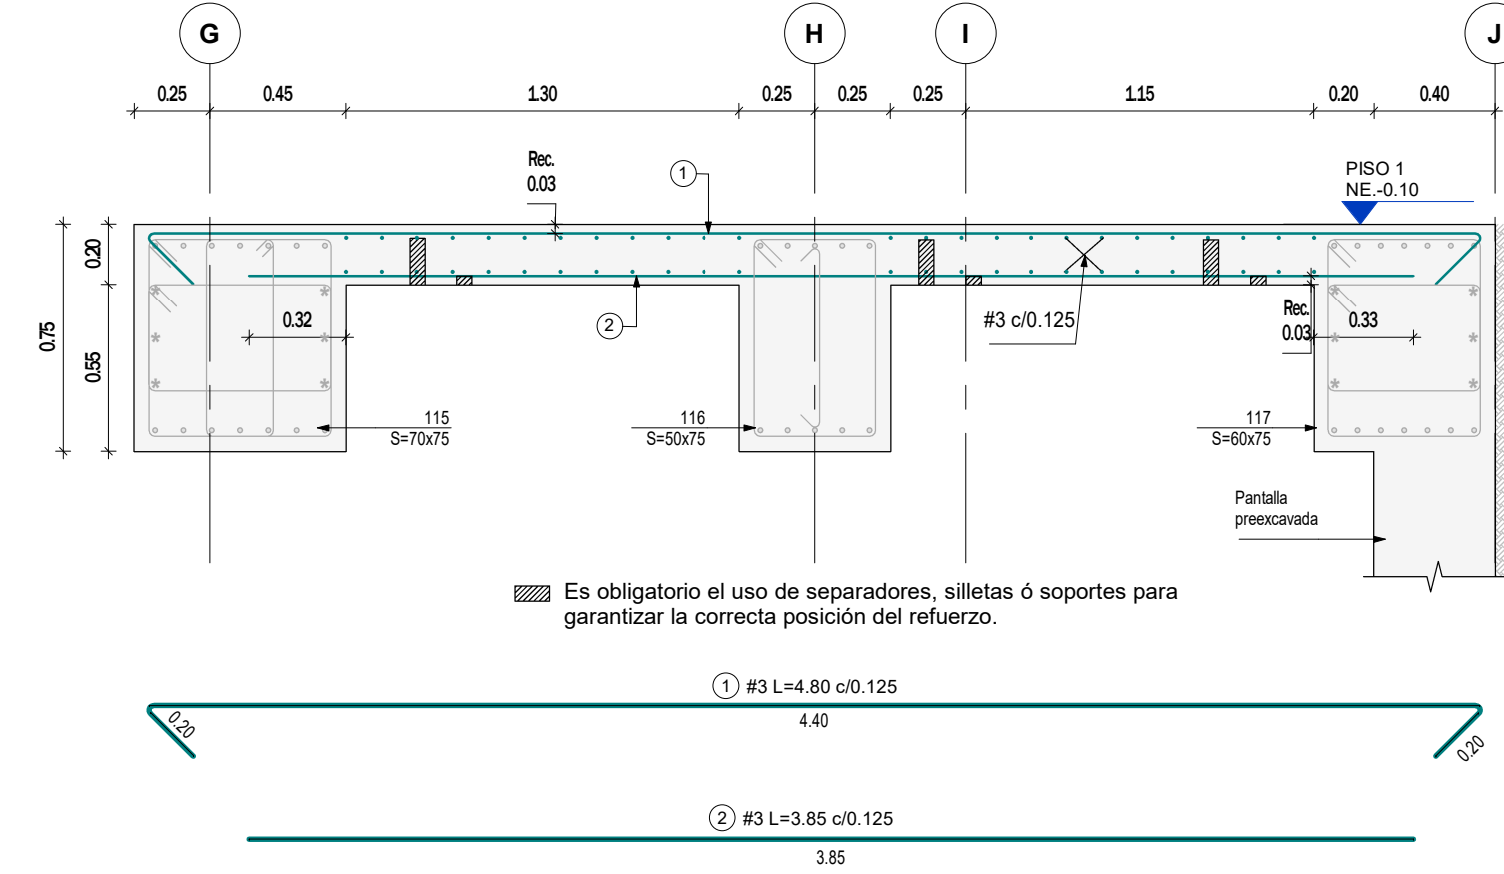

**CORTE 5 - 5**  
**Escala 1 : 25**

