




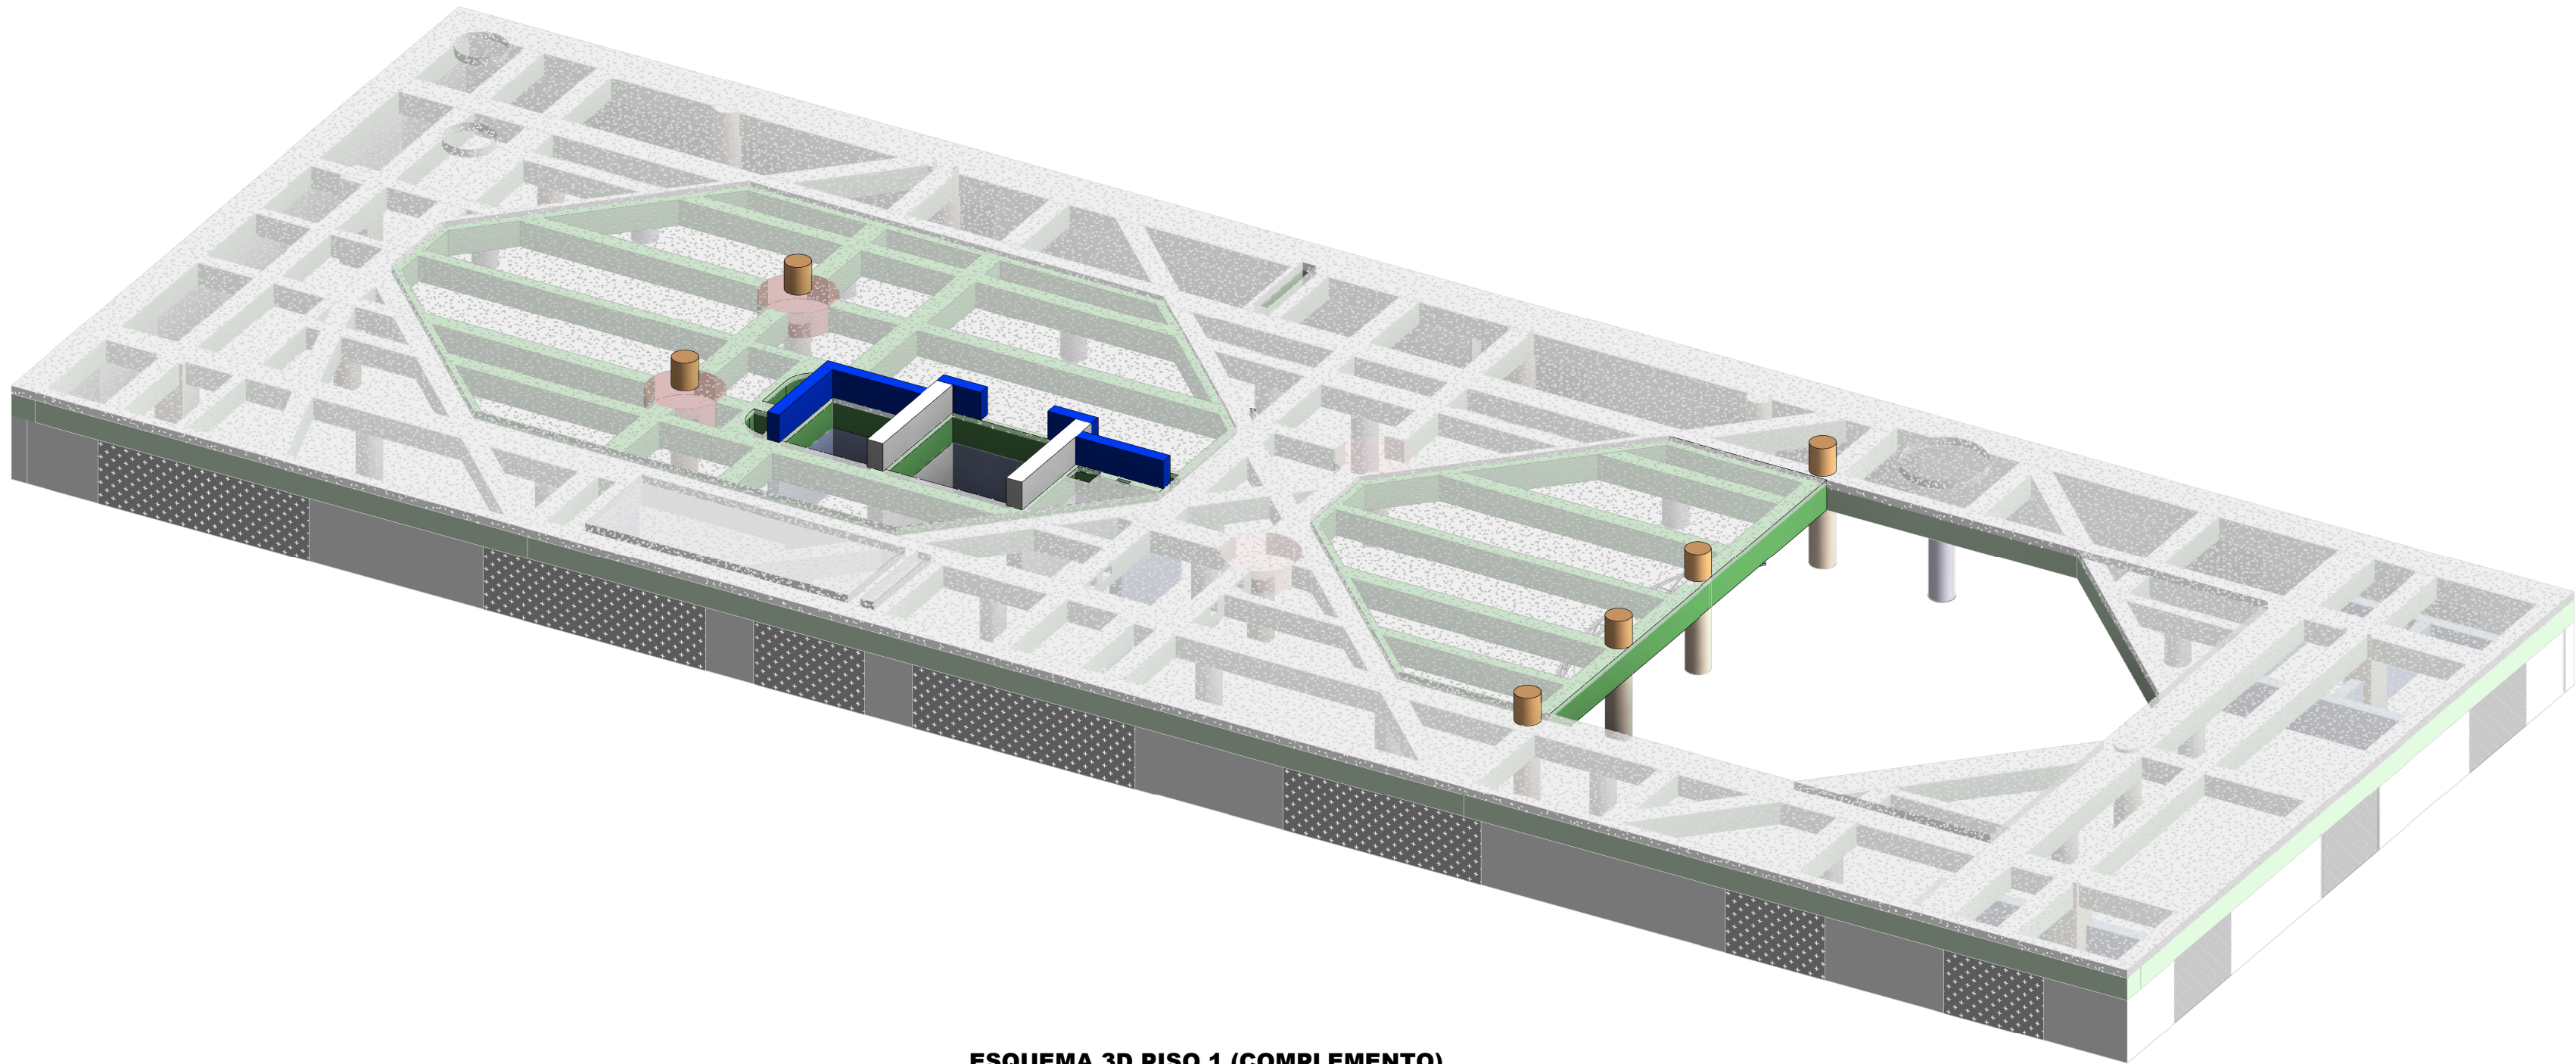

ESQUEMA 3D PISO 1 (COMPLEMENTO)
Sin escala

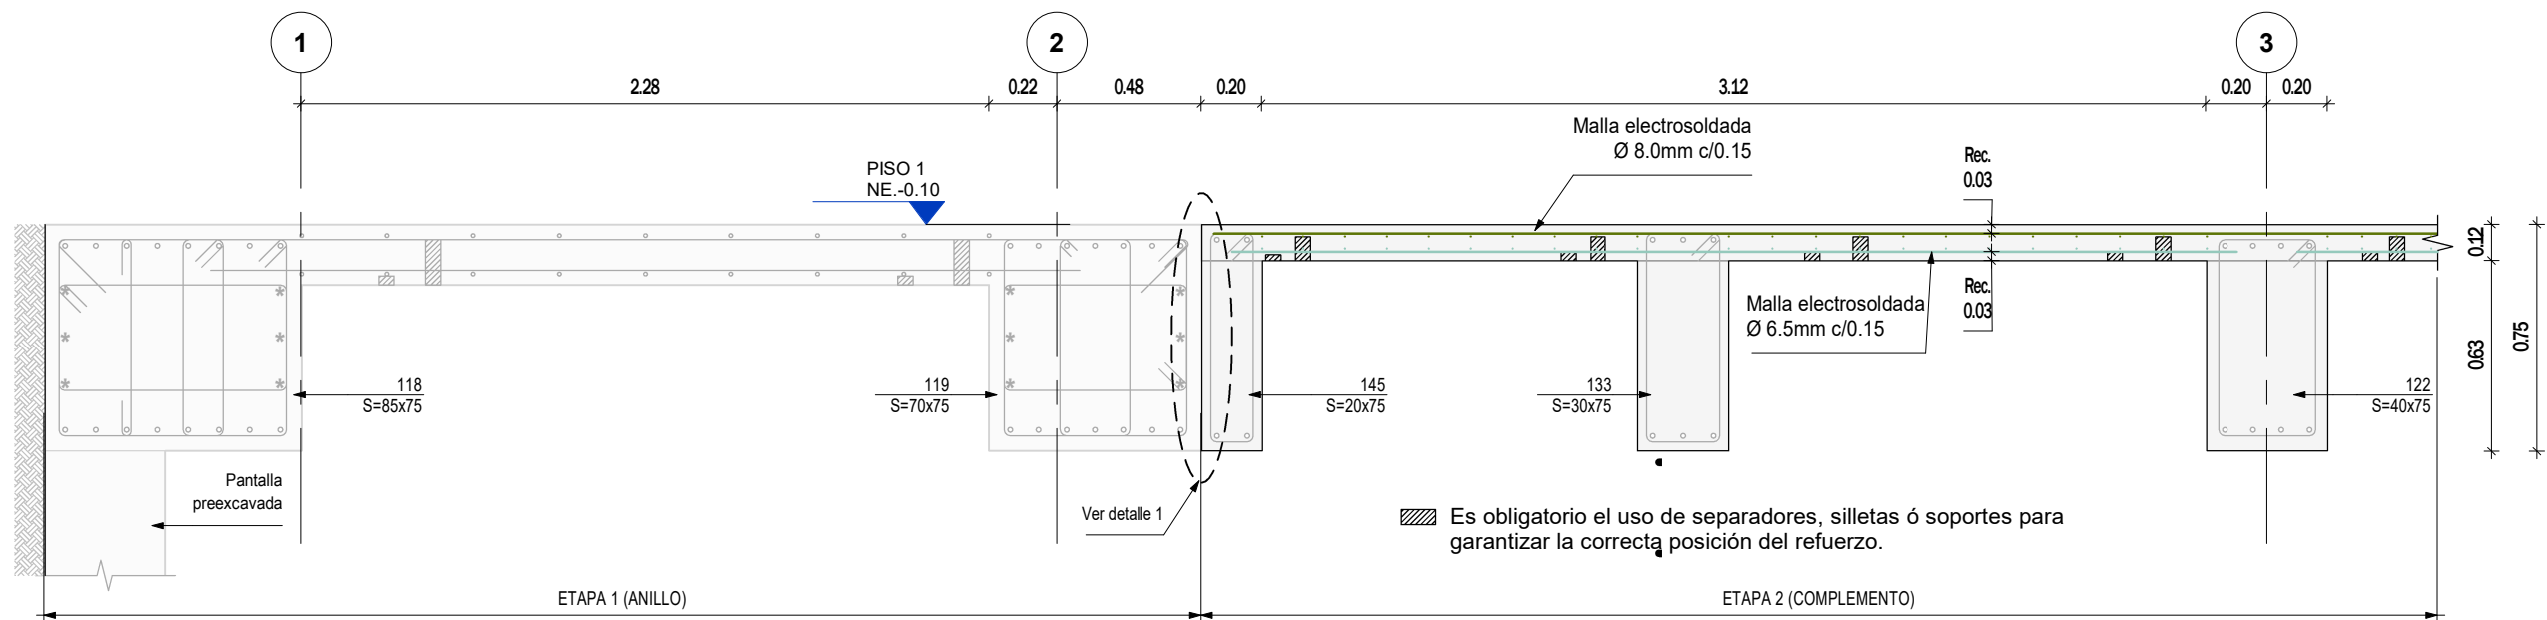


CORTE 1 - 1
Escala 1 : 25

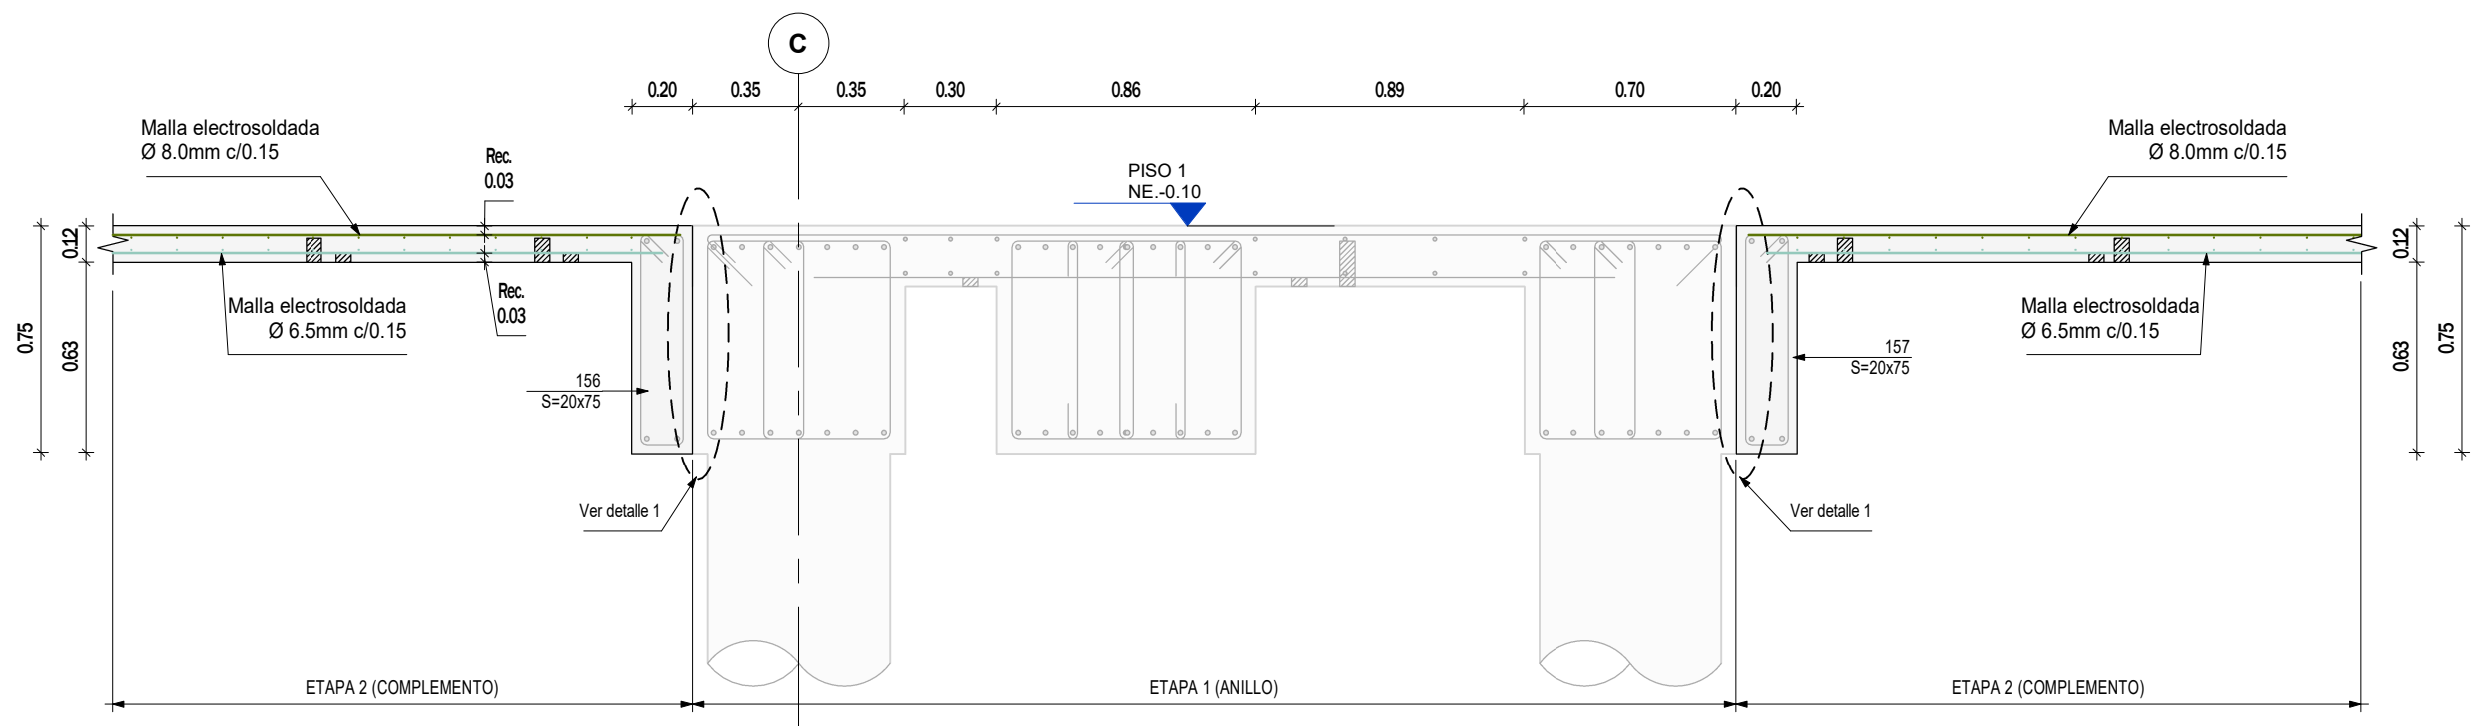

Es obligatorio el uso de separadores, silletas ó soportes para garantizar la correcta posición del refuerzo.

CORTE 2 - 2
Escala 1 : 25

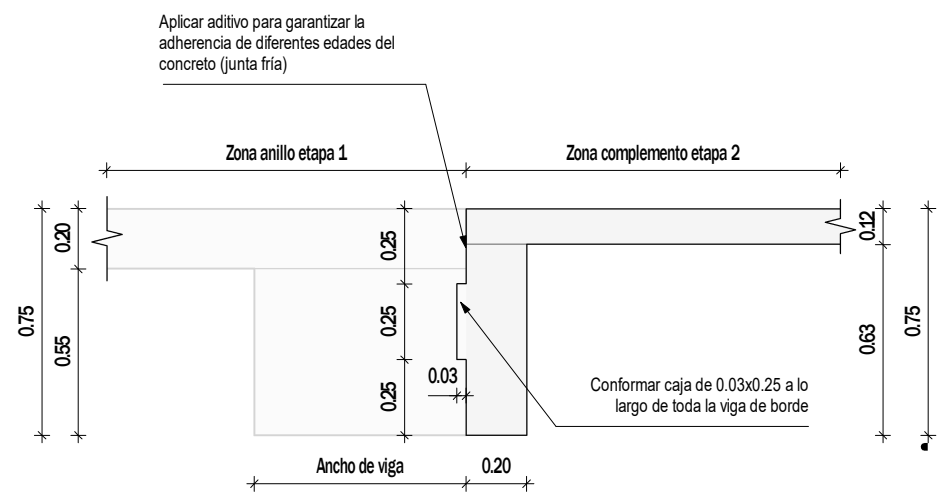

DETALLE 1 VINCULACIÓN DE VIGAS ETAPA 1 Y ETAPA 2
Escala 1 : 25

CONCRETO
 $f_c=35$ MPa
 $f_c=350$ kg/cm²
 $f_c=5000$ psi

NOTAS

- Ver detalles generales en PL N° 01.02 y 01.03
- Ver planta de piso 1 etapa 3 (demolición) en PL N° 07.04

PLANO N° 07.03

VERSIÓN :

0

Aycardi Estructural

GERENTE DE PROYECTO

LUIS ENRIQUE AYCARDI F.
MAT. 2520212794 CND

INGENIERO

DANIEL E. QUICANO C.

MODELADOR

PAULA ANDREA MONTOYA RENDÓN

MODIFICACIONES

FECHA

Emisión Inicial	21-11-2025

HUMANISE STUDIO

EAN-0519- AES-01-EST

Calle 71 #9-84

CORTES Y ESQUEMA 3D PISO 1
ETAPA 2 (COMPLEMENTO)

EAN-0519 -AES-01-EST-N01-PL-527 07.03

REVISOR ESTRUCTURAL

JULIO CESAR SANMIGUEL CAMACHO
MAT. 25202-57738 CND

PLANO N°

VERSIÓN :

07.03

0