



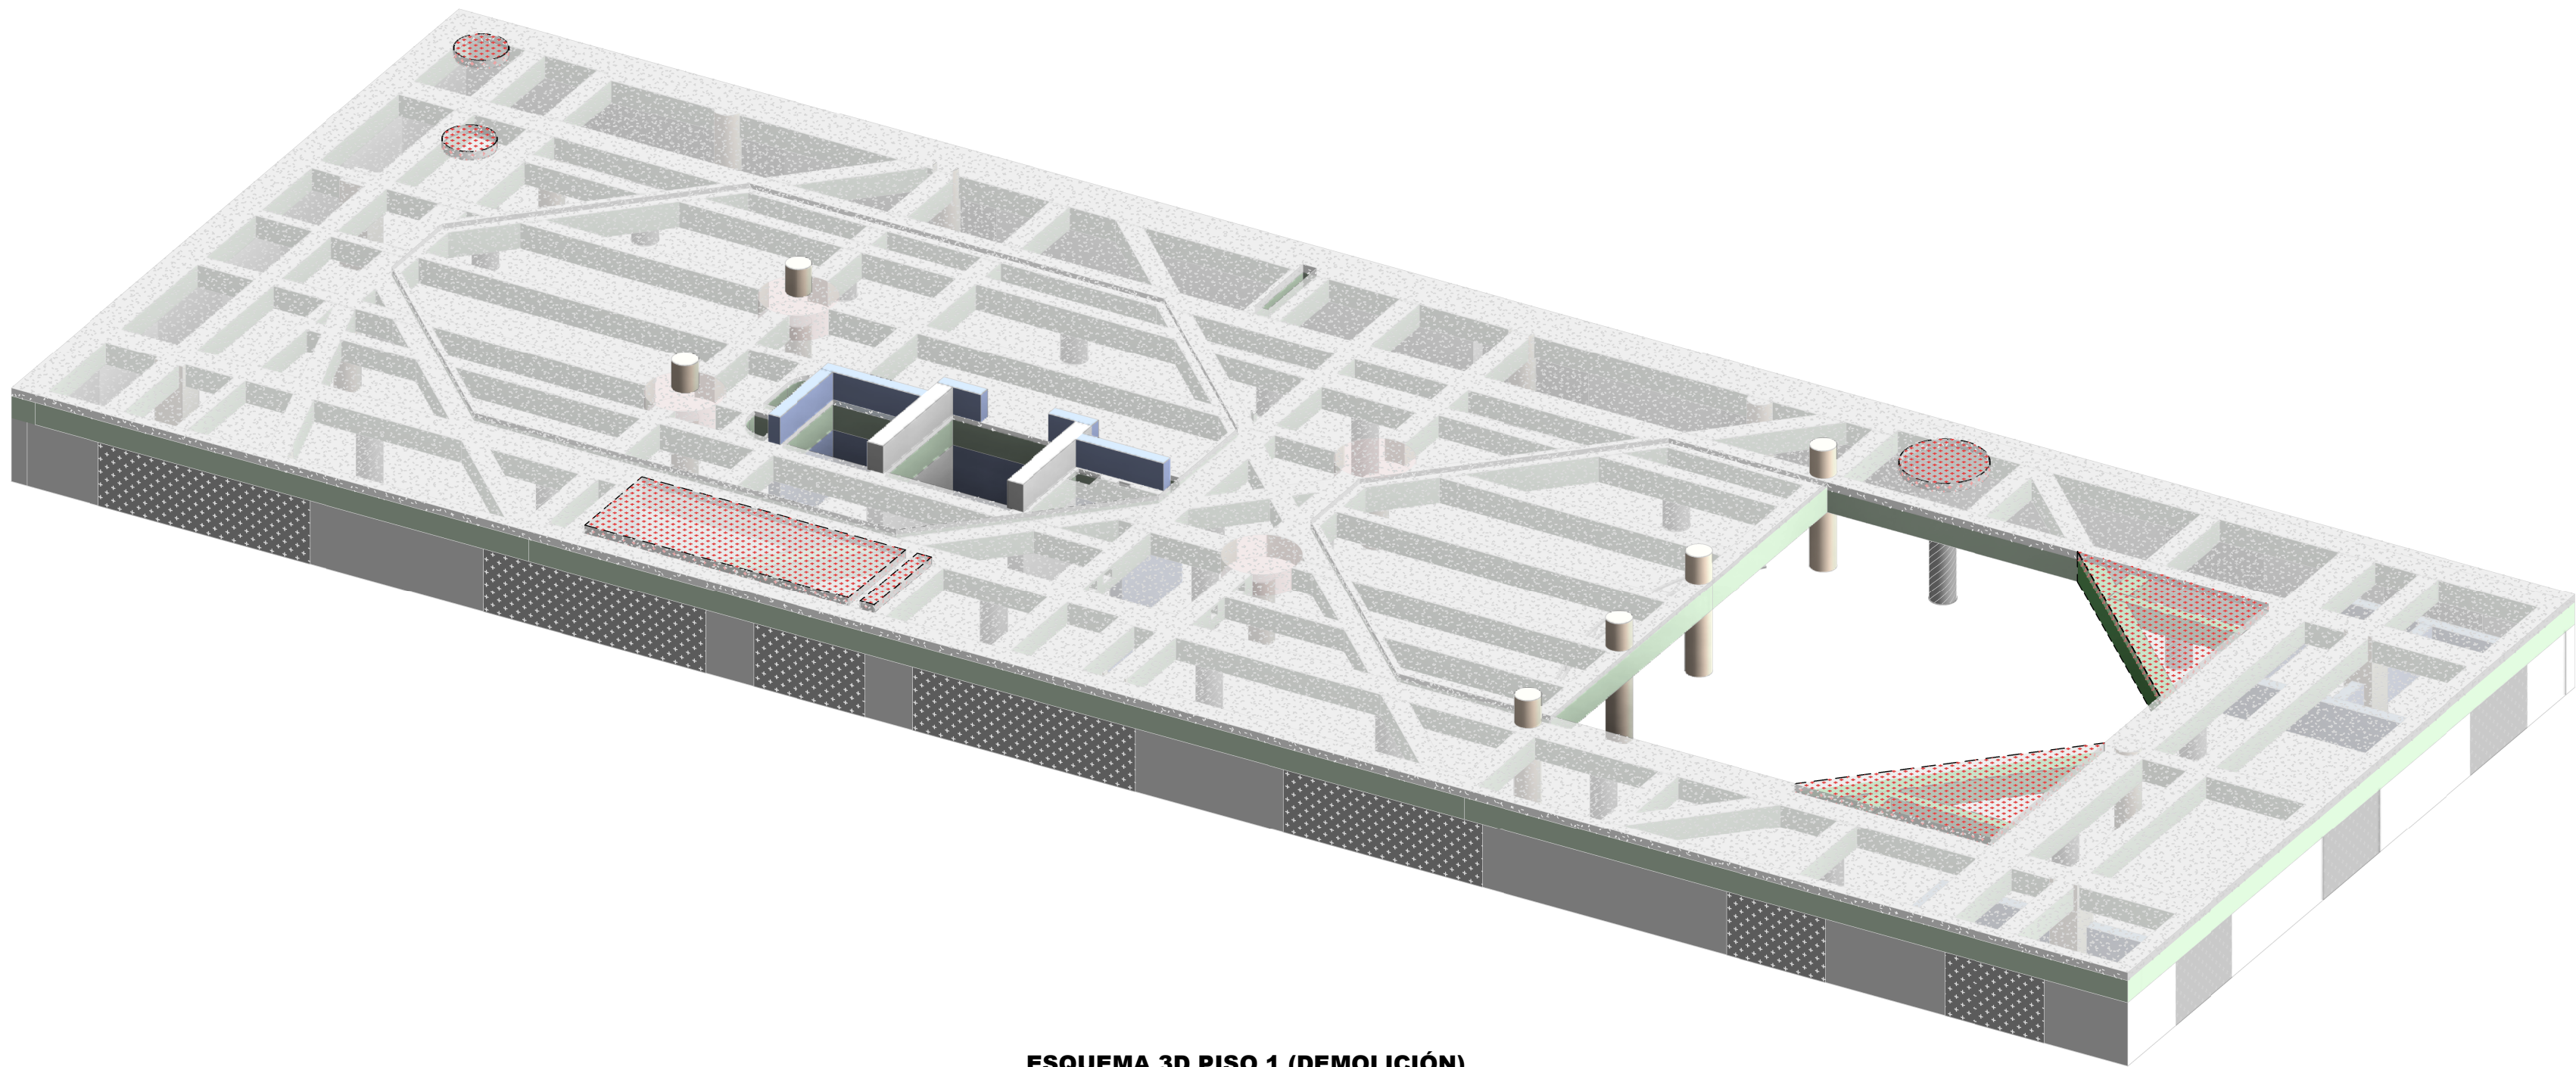

ESQUEMA 3D PISO 1 (DEMOLICIÓN)
Sin escala

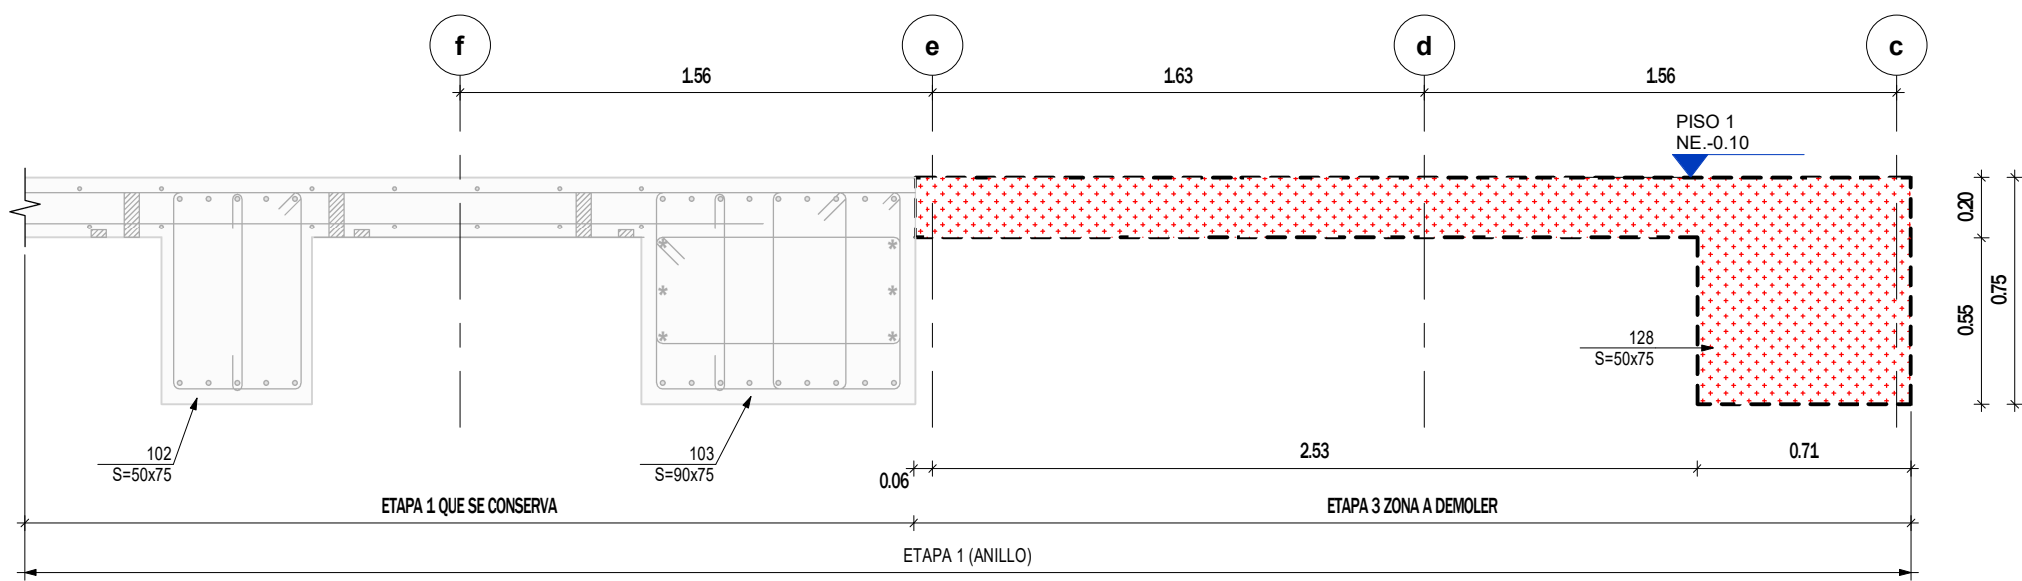

CORTE 1 - 1
Escala 1 : 25

CONCRETO
f'c=35 MPa
f'c=350 kg/cm²
f'c=5000 psi

CONVENCIONES
Indica demoler cuidadosamente

NOTAS
1. Ver planta de piso 1 etapa 2 (complemento) en PL N° 07.00
2. El proceso de demolición será acordado con el constructor, para garantizar la estabilidad de los elementos estructurales.

PLANO N° 07.05
VERSIÓN : 0



GERENTE DE PROYECTO
LUIS ENRIQUE AYCARDI F.
MAT. 2520212794 CND

INGENIERO
DANIEL E. QUICANO C.

MODELADOR
PAULA ANDREA MONTOYA RENDÓN

MODIFICACIONES	FECHA
Emisión Inicial	21-11-2025

HUMANISE STUDIO

EAN-0519- AES-01-EST

Calle 71 #9-84

CORTES Y ESQUEMA 3D PISO 1
ETAPA 3 (DEMOLICIÓN)

EAN-0519 -AES-01-EST-N01-PL-528 07.05

REVISOR ESTRUCTURAL
JULIO CESAR SANMIGUEL CAMACHO
MAT. 25202-57738 CND

PLANO N°

07.05

VERSIÓN :

0

