



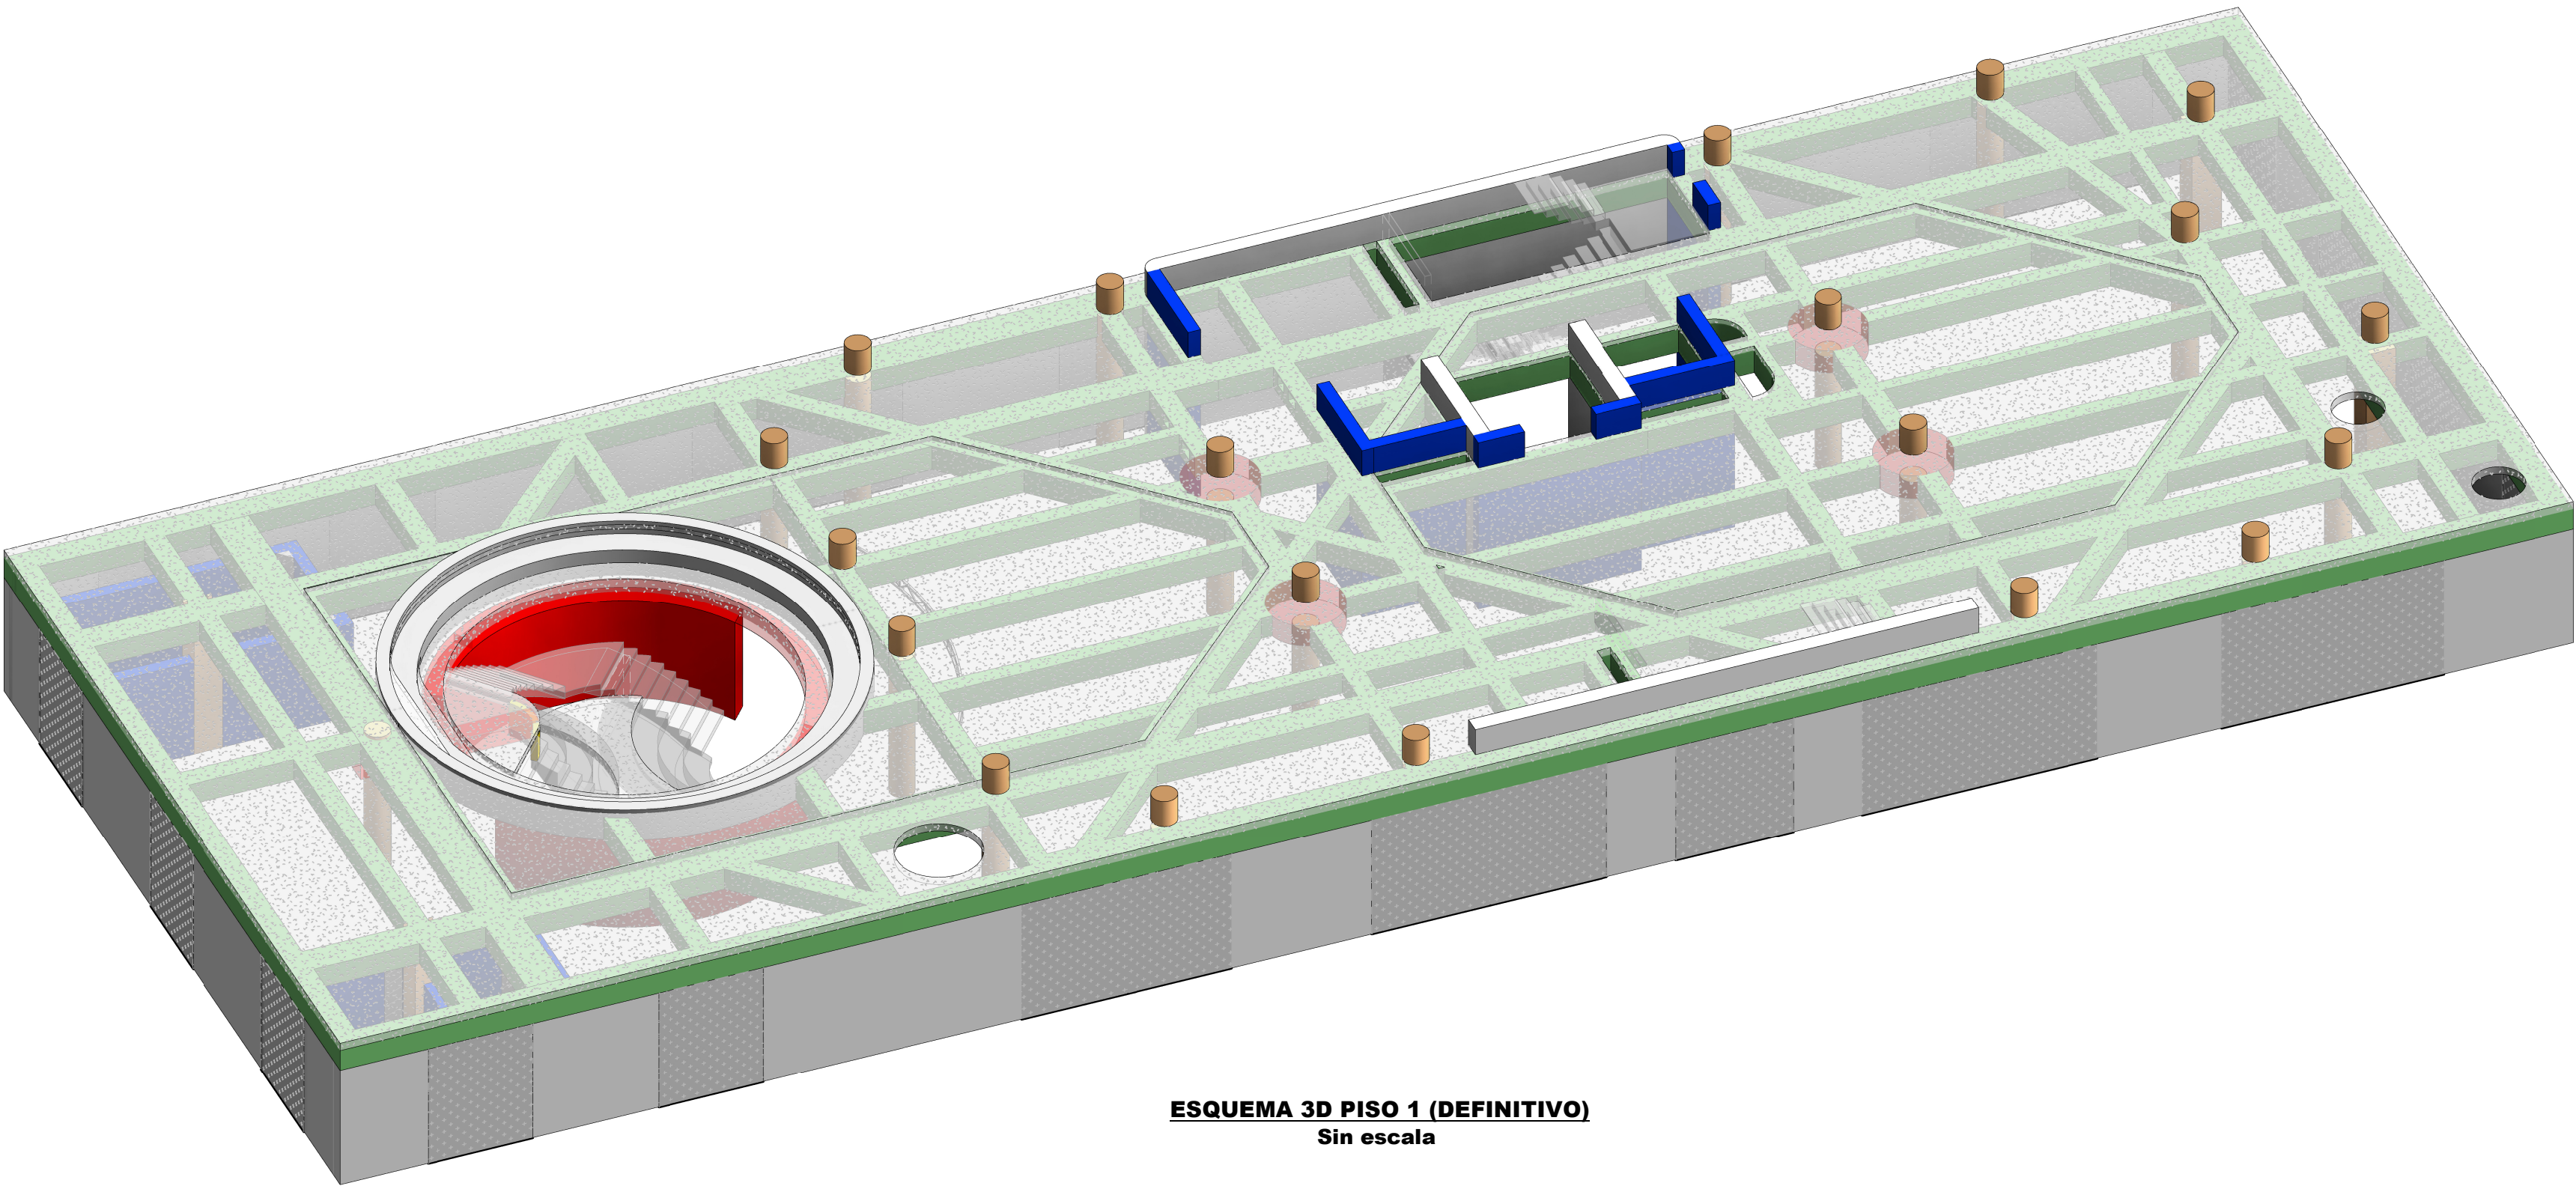

ESQUEMA 3D PISO 1 (DEFINITIVO)
Sin escala

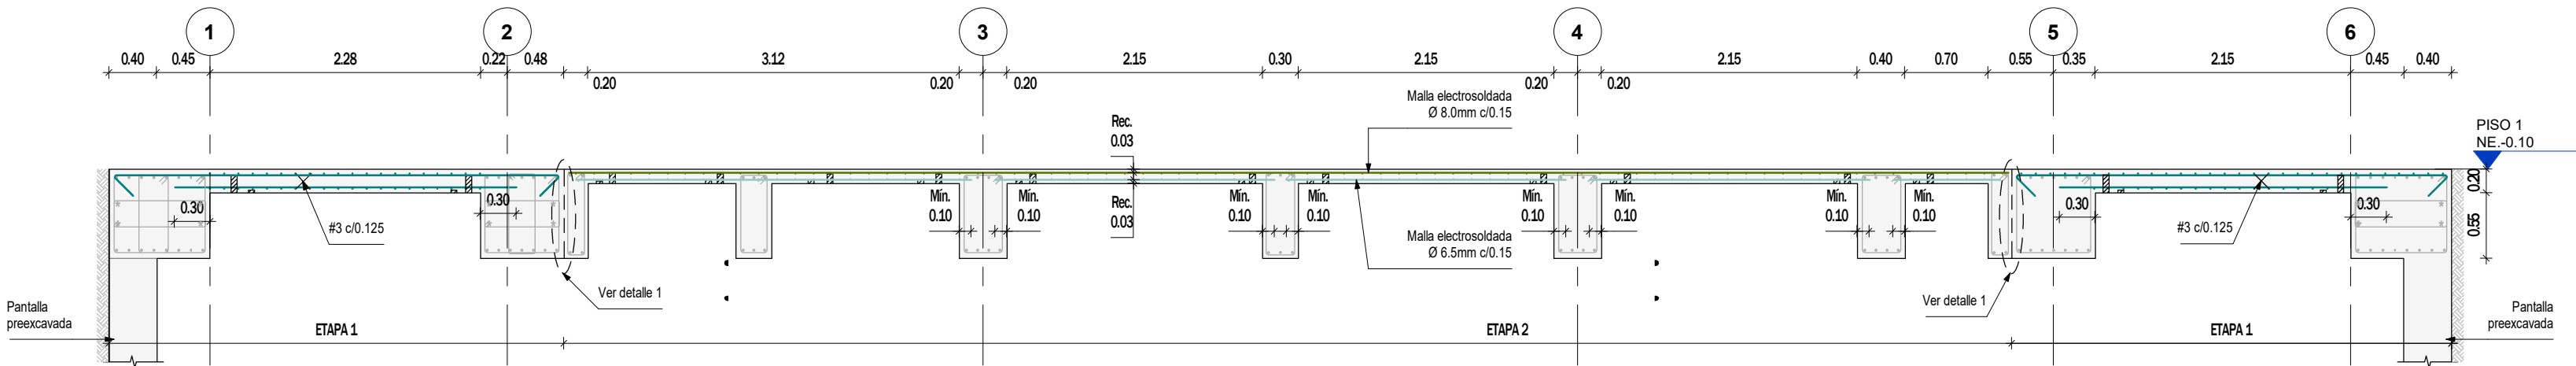

Es obligatorio el uso de separadores, silletas ó soportes para garantizar la correcta posición del refuerzo.

CORTE 1 - 1
Escala 1 : 50

MODIFICACIONES	FECHA
Emisión Inicial	21-11-2025

EAN-0519- AES-01-EST

Calle 71 #9-84

CORTES Y ESQUEMA 3D PISO 1
(DEFINITIVA)

EAN-0519 -AES-01-EST-N01-PL-530 07.09

REVISOR ESTRUCTURAL
JULIO CESAR SANMIGUEL CAMACHO
MAT. 25202-57738 CND

NOTAS

1. Ver detalle 1 en el PL N° 07.06

PLANO N° 07.09

VERSIÓN : 0

Aycardi Estructural

GERENTE DE PROYECTO
LUIS ENRIQUE AYCARDI F.
MAT. 2520212794 CND

INGENIERO
DANIEL E. QUICANO C.

MODELADOR
PAULA ANDREA MONTOYA RENDÓN

HUMANISE STUDIO