


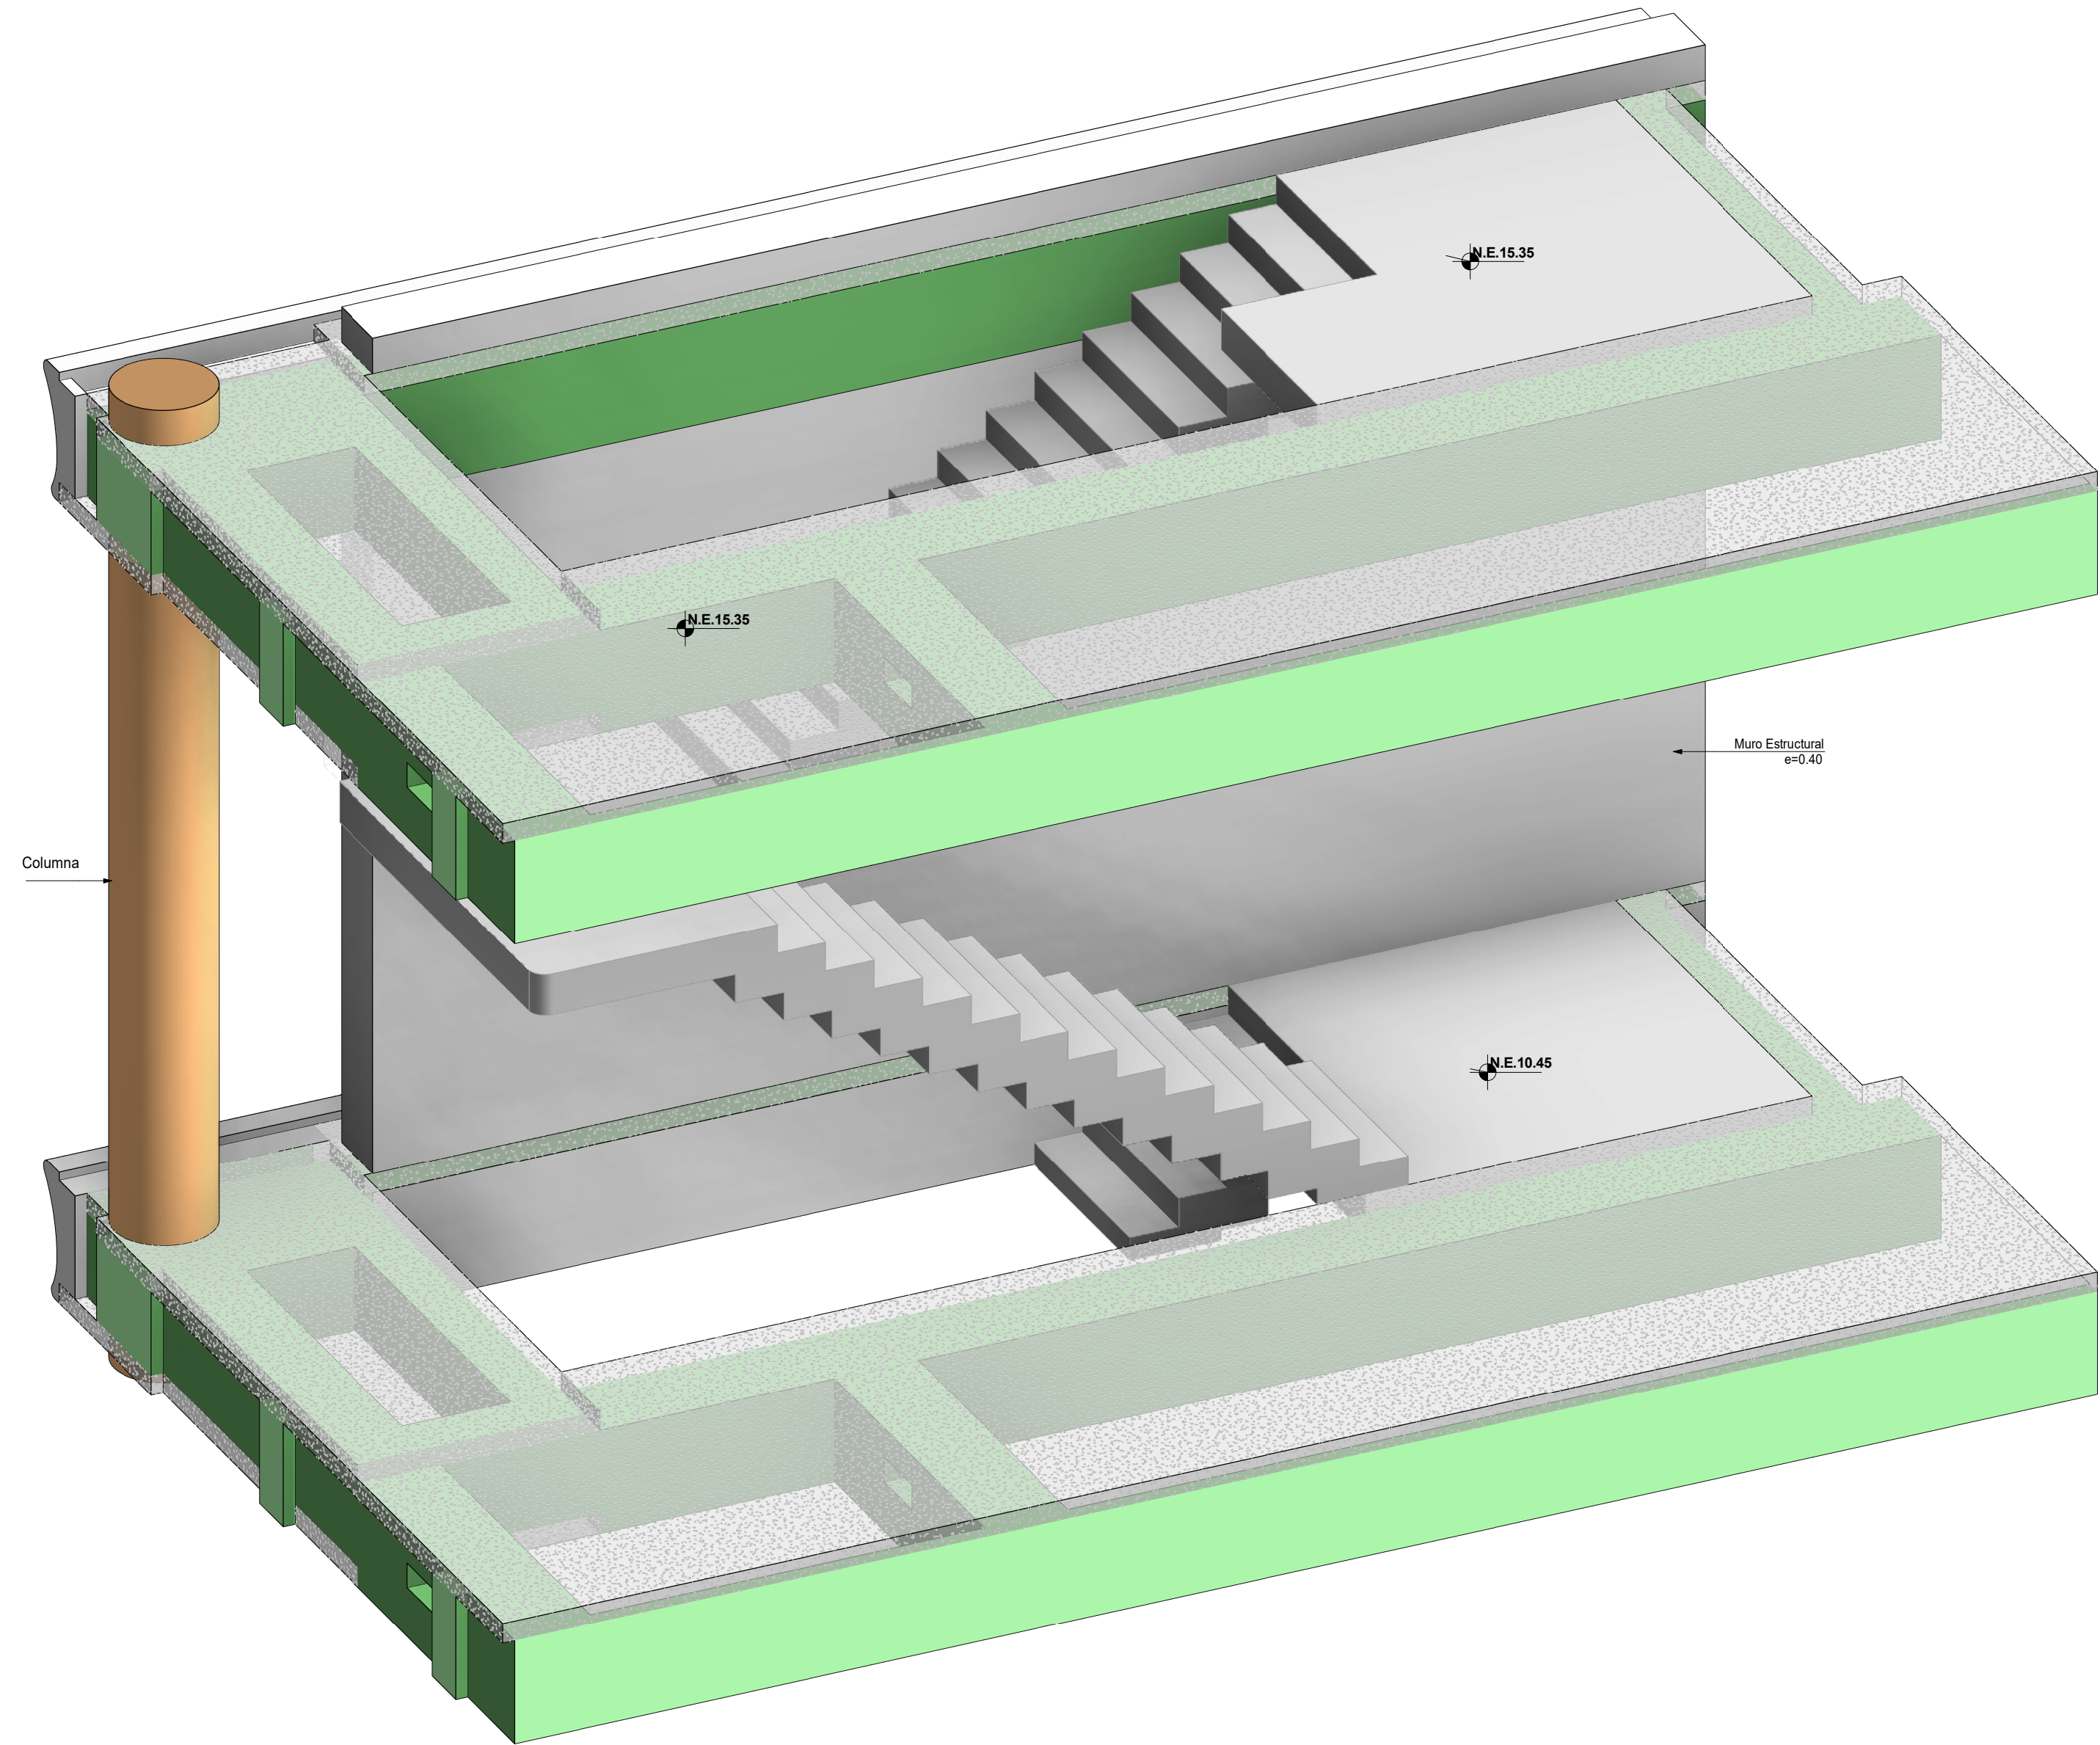

ESQUEMA 3D ESCALERA TIPO 2 PISO 3 A PISO 4
Sin escala

#	Ø	Figuración [m]	Longitud total [m]	Peso c/varilla [kg]	Cantidad varillas	Long. todas varillas [m]	Peso Total [kg]
①	#4		10.48	10.42	9	94.34	93.81
②	#6		10.63	23.78	9	95.64	213.98
③	#6		3.86	8.63	17	65.55	146.66
④	#3		0.53	0.3	252	133.61	74.73
⑤	#6		3.1	4.81	10	30.99	48.14
⑥	#4		2.89	2.87	10	28.9	28.74
⑦	#6		10.53	23.57	9	94.8	212.1
⑧	#4		10.48	10.42	9	94.34	93.81
⑨	#6		3.1	4.81	13	40.28	62.59
⑩	#3		0.56	0.31	252	139.96	78.29
⑪	#4		2.89	2.87	14	40.46	40.23
⑮	#5		3.1	4.81	14	43.38	67.4
⑯	#4		2.89	2.87	16	46.24	45.98
Total mass = 1206 kg							

Grade	Ø	Long. todas varillas [m]	Peso Total [kg]
Gr 60	#3	273.57	153.02
Gr 60	#4	304.28	302.58
Gr 60	#5	114.65	178.13
Gr 60	#6	255.98	572.75

CONCRETO

f'c=28 MPa
f'c=280 kg/cm²
f'c=4000 psi

NOTAS
1. Ver detalles generales en los planos PL N° 01.02 y 01.03

PLANO N° 17.13

VERSIÓN : 0



GERENTE DE PROYECTO
LUIS ENRIQUE AYCARDI F.
MAT. 2520212794 CND

INGENIERO
DANIEL E. QUICANO C.

MODELADOR
FELIPE SALINAS RODRÍGUEZ

MODIFICACIONES	FECHA
Emisión Inicial	21-11-2025

HUMANISE STUDIO

EAN-0519- AES-01-EST

Calle 71 #9-84

DESPIECE DE ESCALERA TIPO 2 PISO 3 A PISO 4

EAN-0519 -AES-01-EST-PL-5101 17.13

REVISOR ESTRUCTURAL
JULIO CESAR SANMIGUEL CAMACHO
MAT. 25202-57738 CND

PLANO N° 17.13
VERSIÓN : 0

