



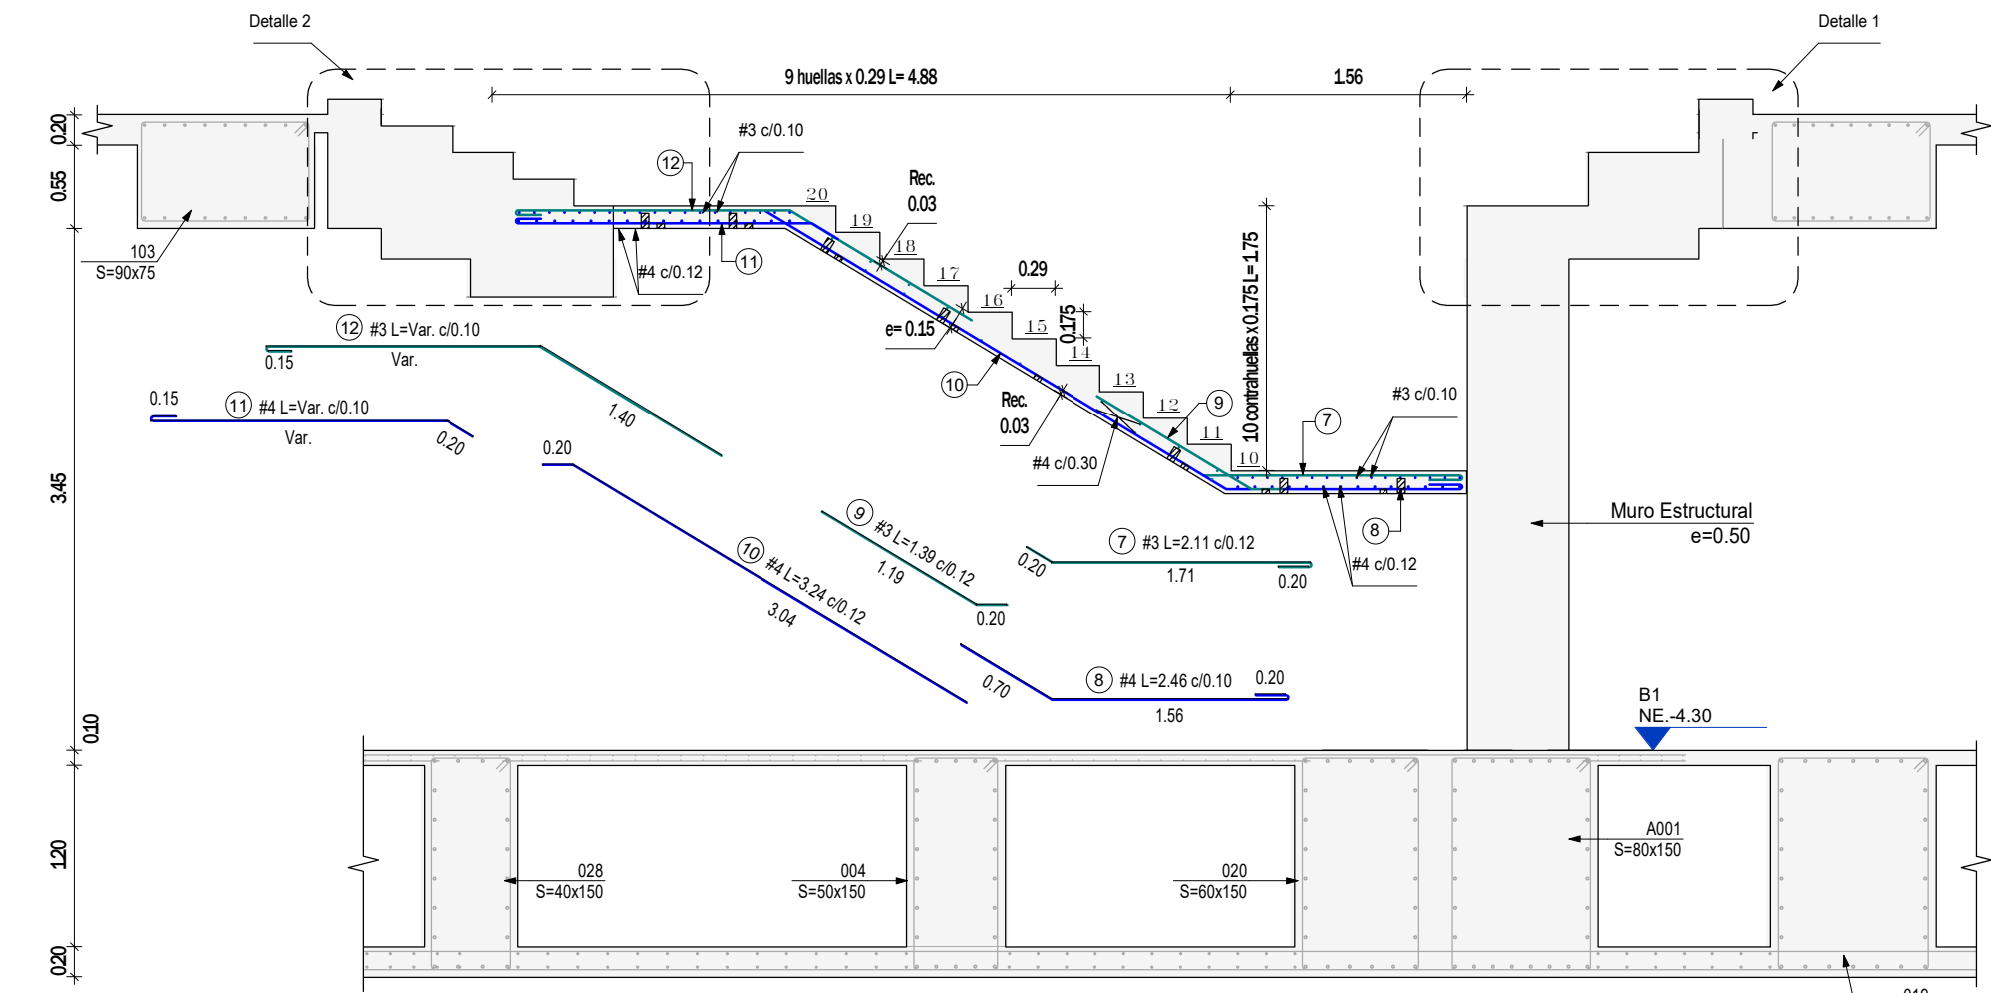


Es obligatorio el uso de separadores, silletas ó soportes para garantizar la correcta posición del refuerzo.


CORTE A3
Escala 1 : 50

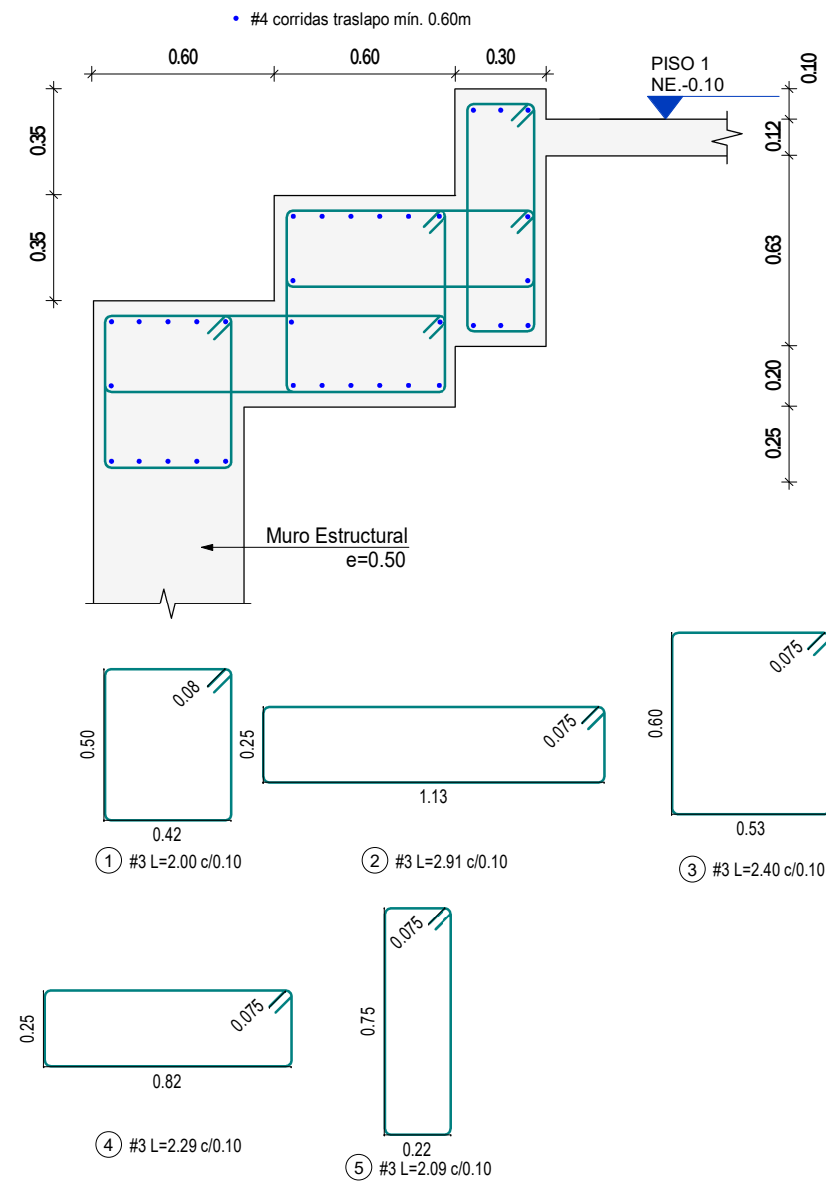


DETALLE 1 VIGAS CORONA ANFITEATRO
Escala 1 : 25

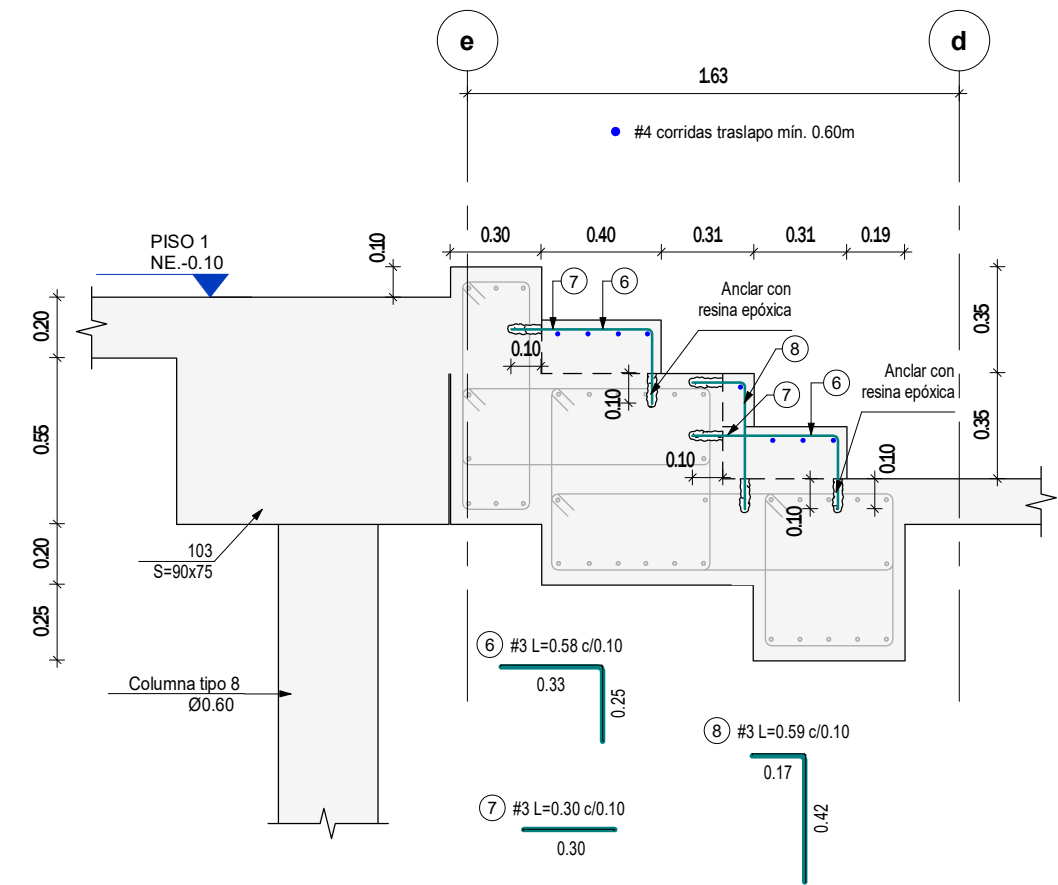

DETALLE 2 VIGAS CORONA ANFITEATRO
Escala 1 : 25

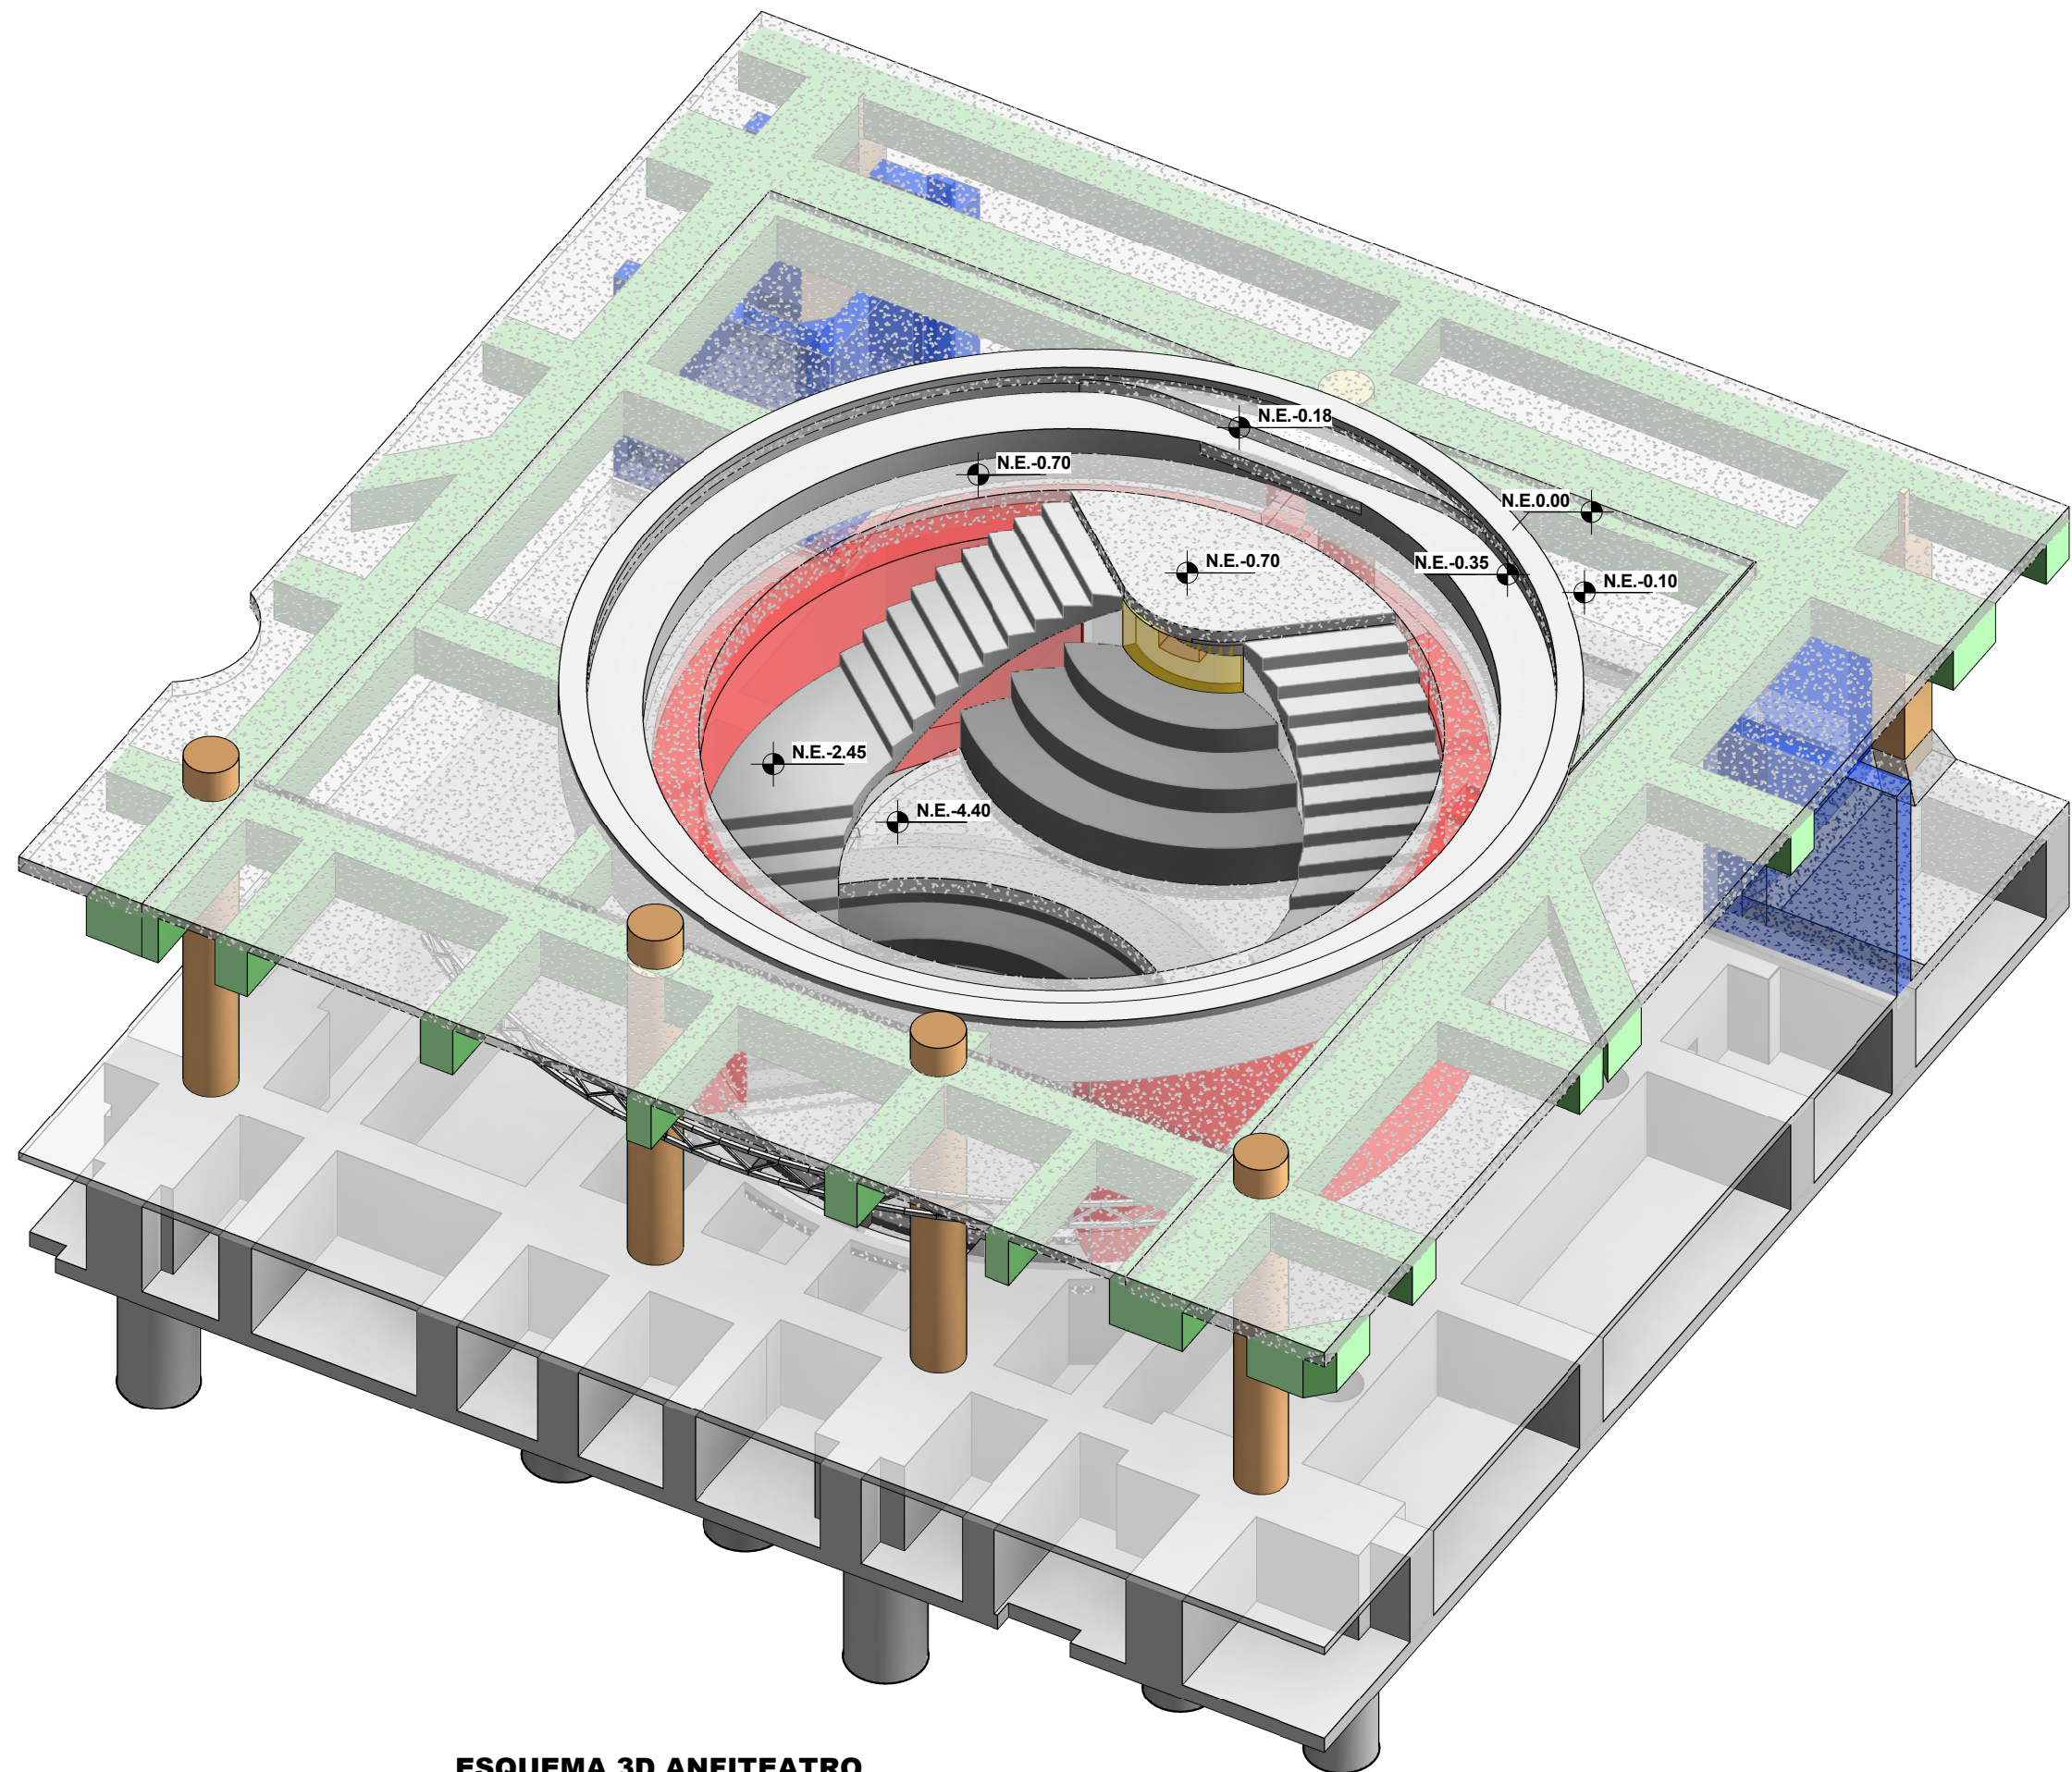

ESQUEMA 3D ANFITEATRO
Sin escala

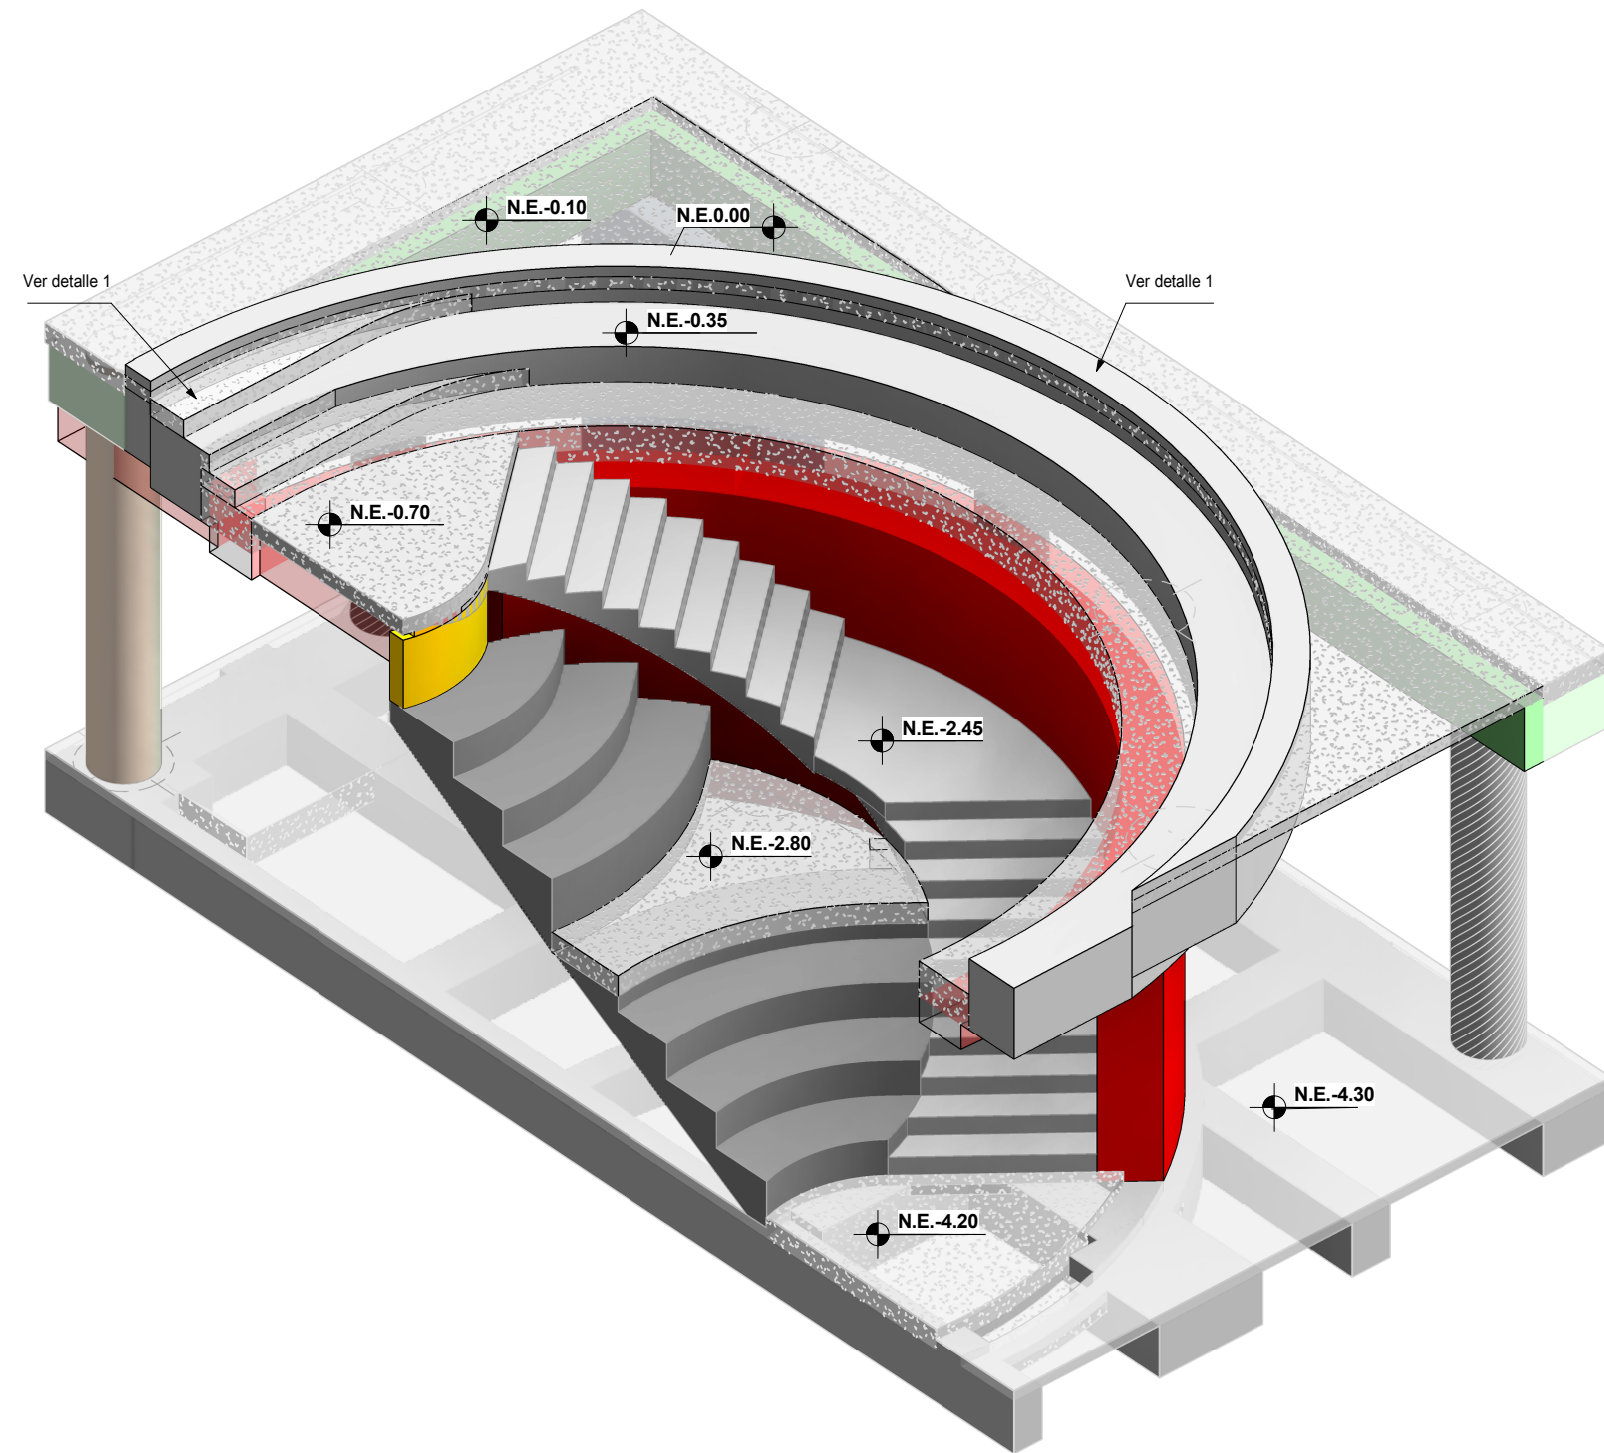

ESQUEMA 3D ESCALERA Y GRADERA ANFITEATRO
Sin escala

CONCRETO
 $f_c=35$ MPa
 $f_c=350$ kg/cm²
 $f_c=5000$ psi

PLANO N°

05.01

VERSIÓN :

0

GERENTE DE PROYECTO

LUIS ENRIQUE AYCARDI F.

MAT. 2520212794 CND

INGENIERO

DANIEL E. QUICANO C.

MODELADOR

PAULA ANDREA MONTOYA RENDÓN

MODIFICACIONES	FECHA
Emisión Inicial	21-11-2025

HUMANISE STUDIO

EAN-0519- AES-01-EST

Calle 71 #9-84

DETALLES ANFITEATRO

EAN-0519 -AES-01-EST-PL-516 05.01

REVISOR ESTRUCTURAL

JULIO CESAR SANMIGUEL CAMACHO

MAT. 25202-57738 CND

PLANO N°

05.01

VERSIÓN :

0