



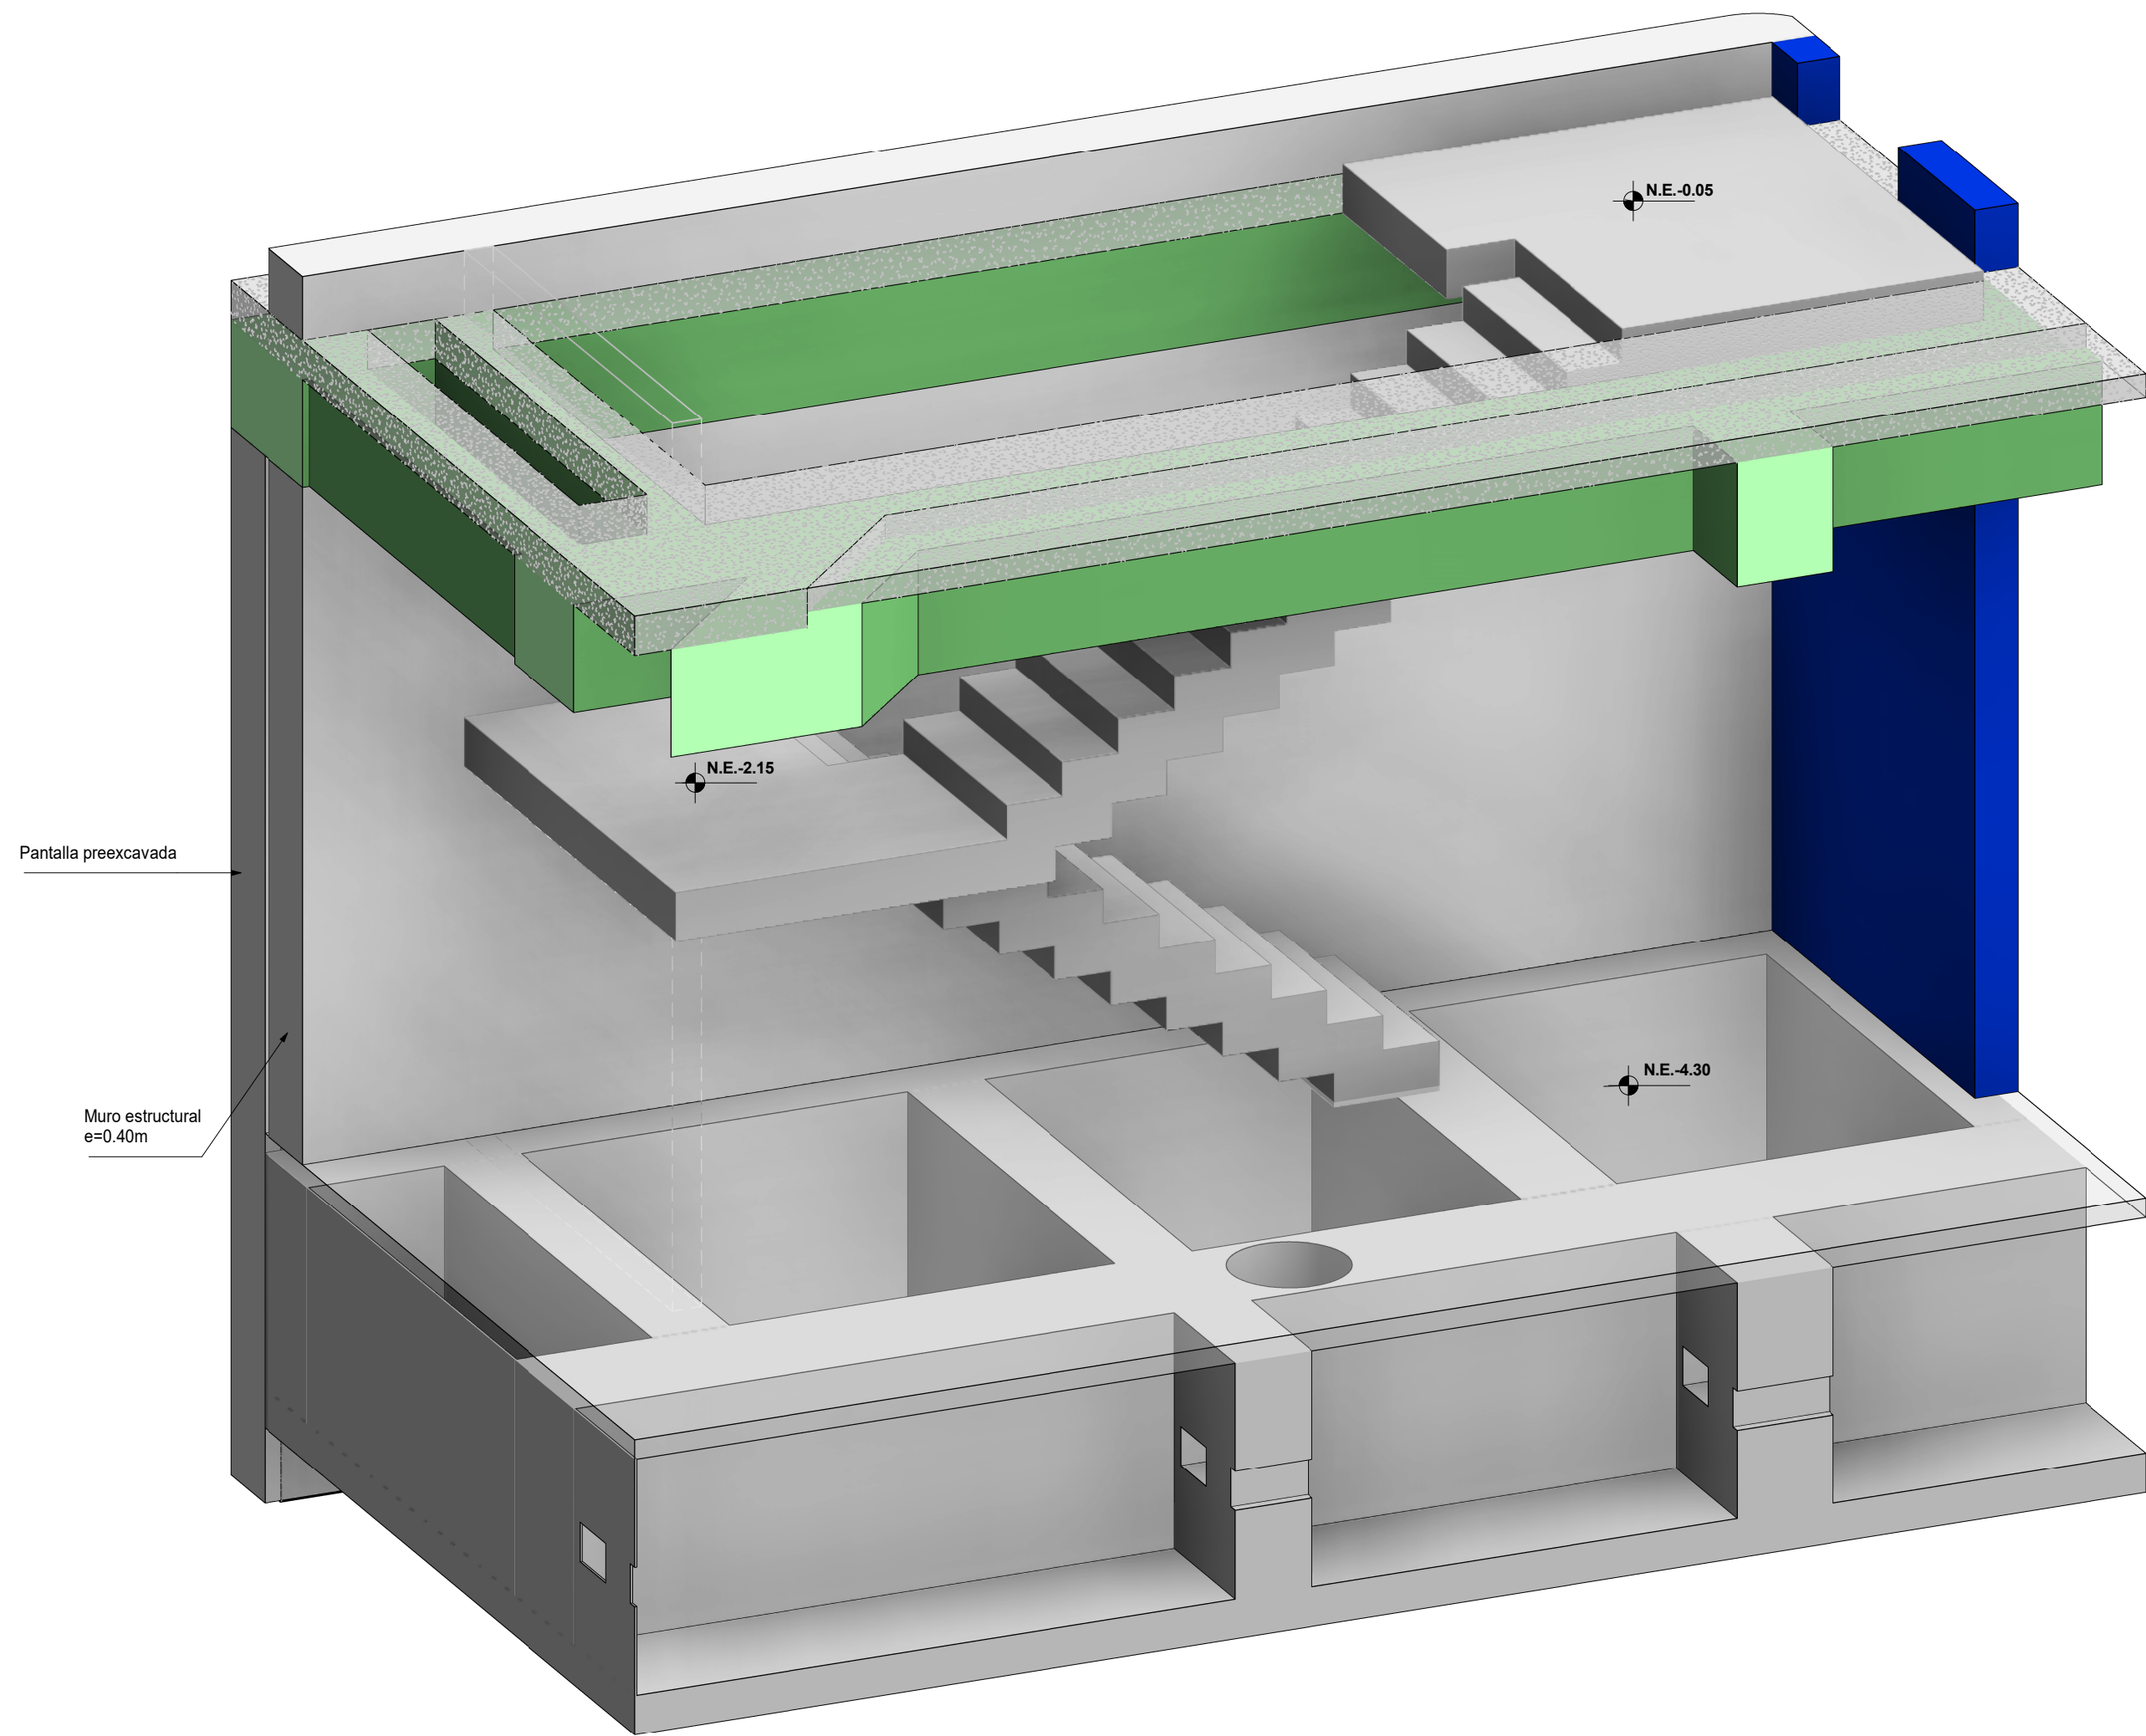

ESQUEMA 3D ESCALERA CIMENTACIÓN A PISO 1
Sin escala

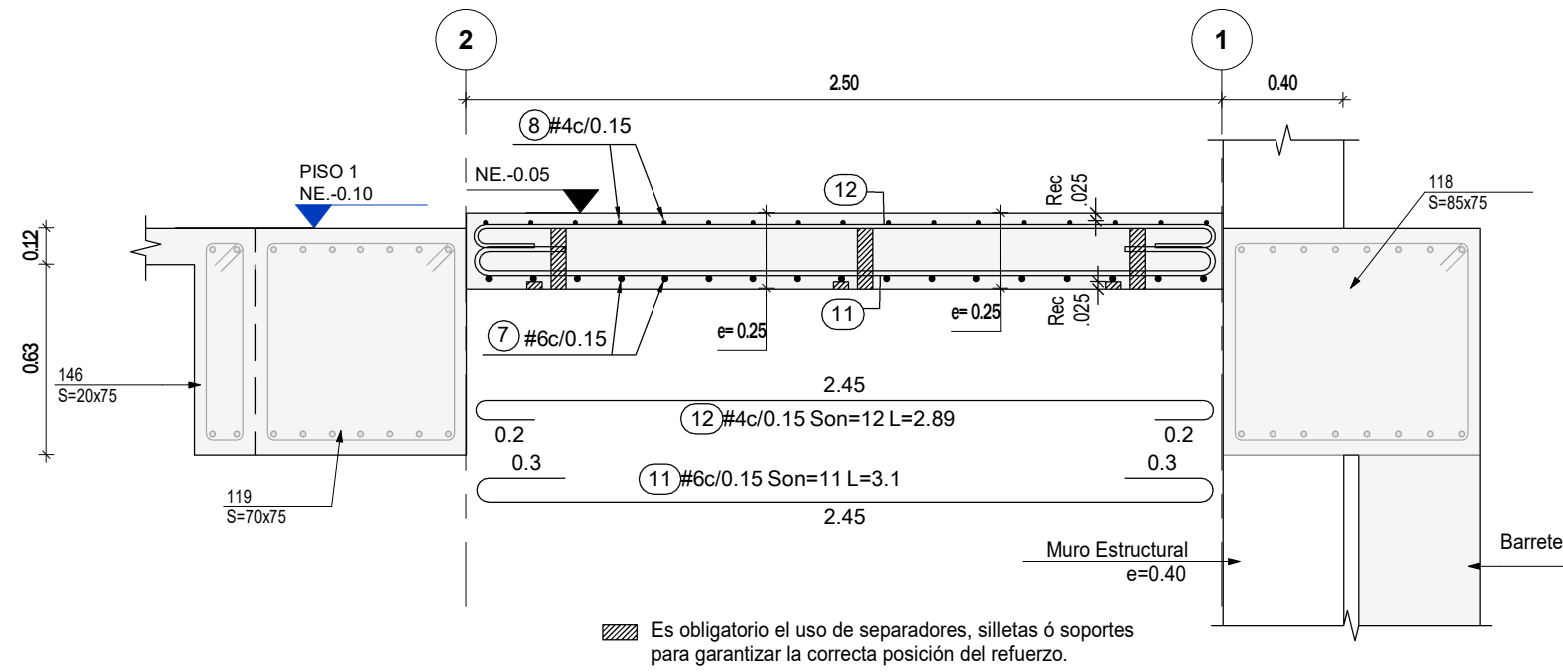

CORTE E-4
Escala 1 : 25

#	Ø	Figuración [m]	Longitud total [m]	Peso o'varilla [kg]	Cantidad varillas	Long. todas varillas [m]	Peso Total [kg]
1	#3		0.56	0.31	198	109.97	61.51
2	#6		6.96	15.56	9	62.6	140.07
3	#4		7.24	7.2	9	65.12	64.76
4	#6		4.12	9.22	18	74.16	165.93
5	#6		3.1	4.82	7	21.71	33.74
6	#4		2.89	2.88	9	26.04	25.89
7	#6		9.09	20.33	9	81.79	182.99
8	#4		9.03	8.98	9	81.3	80.84
9	#3		0.56	0.31	23	12.77	7.15
11	#6		3.1	4.82	11	34.12	53.01
12	#4		2.89	2.88	12	34.71	34.52
Total mass = 850 kg							

Grade	Ø	Long. todas varillas [m]	Peso Total [kg]
Gr 60	#3	122.74	68.66
Gr 60	#4	207.17	206.01
Gr 60	#5	55.83	86.75
Gr 60	#6	62.6	140.07
Gr 60	#6	155.95	348.93

CONCRETO
f'c=28 MPa
f'c=280 kg/cm²
f'c=4000 psi

NOTAS

1. Ver detalles generales en los planos PL N° 01.02 y 01.03

PLANO N° 17.01

VERSIÓN : 0



GERENTE DE PROYECTO
LUIS ENRIQUE AYCARDI F.
MAT. 2520212794 CND

INGENIERO
DANIEL E. QUICANO C.

MODELADOR
FELIPE SALINAS RODRIGUEZ

MODIFICACIONES	FECHA
Emisión Inicial	21-11-2025

HUMANISE STUDIO

EAN-0519- AES-01-EST

Calle 71 #9-84

DESPIECE DE ESCALERA TIPO 1 DE
CIMENTACIÓN A PISO 1

EAN-0519 -AES-01-EST-PL-589 17.01

REVISOR ESTRUCTURAL
JULIO CESAR SANMIGUEL CAMACHO
MAT. 25202-57738 CND

PLANO N°

17.01

VERSIÓN :

0