


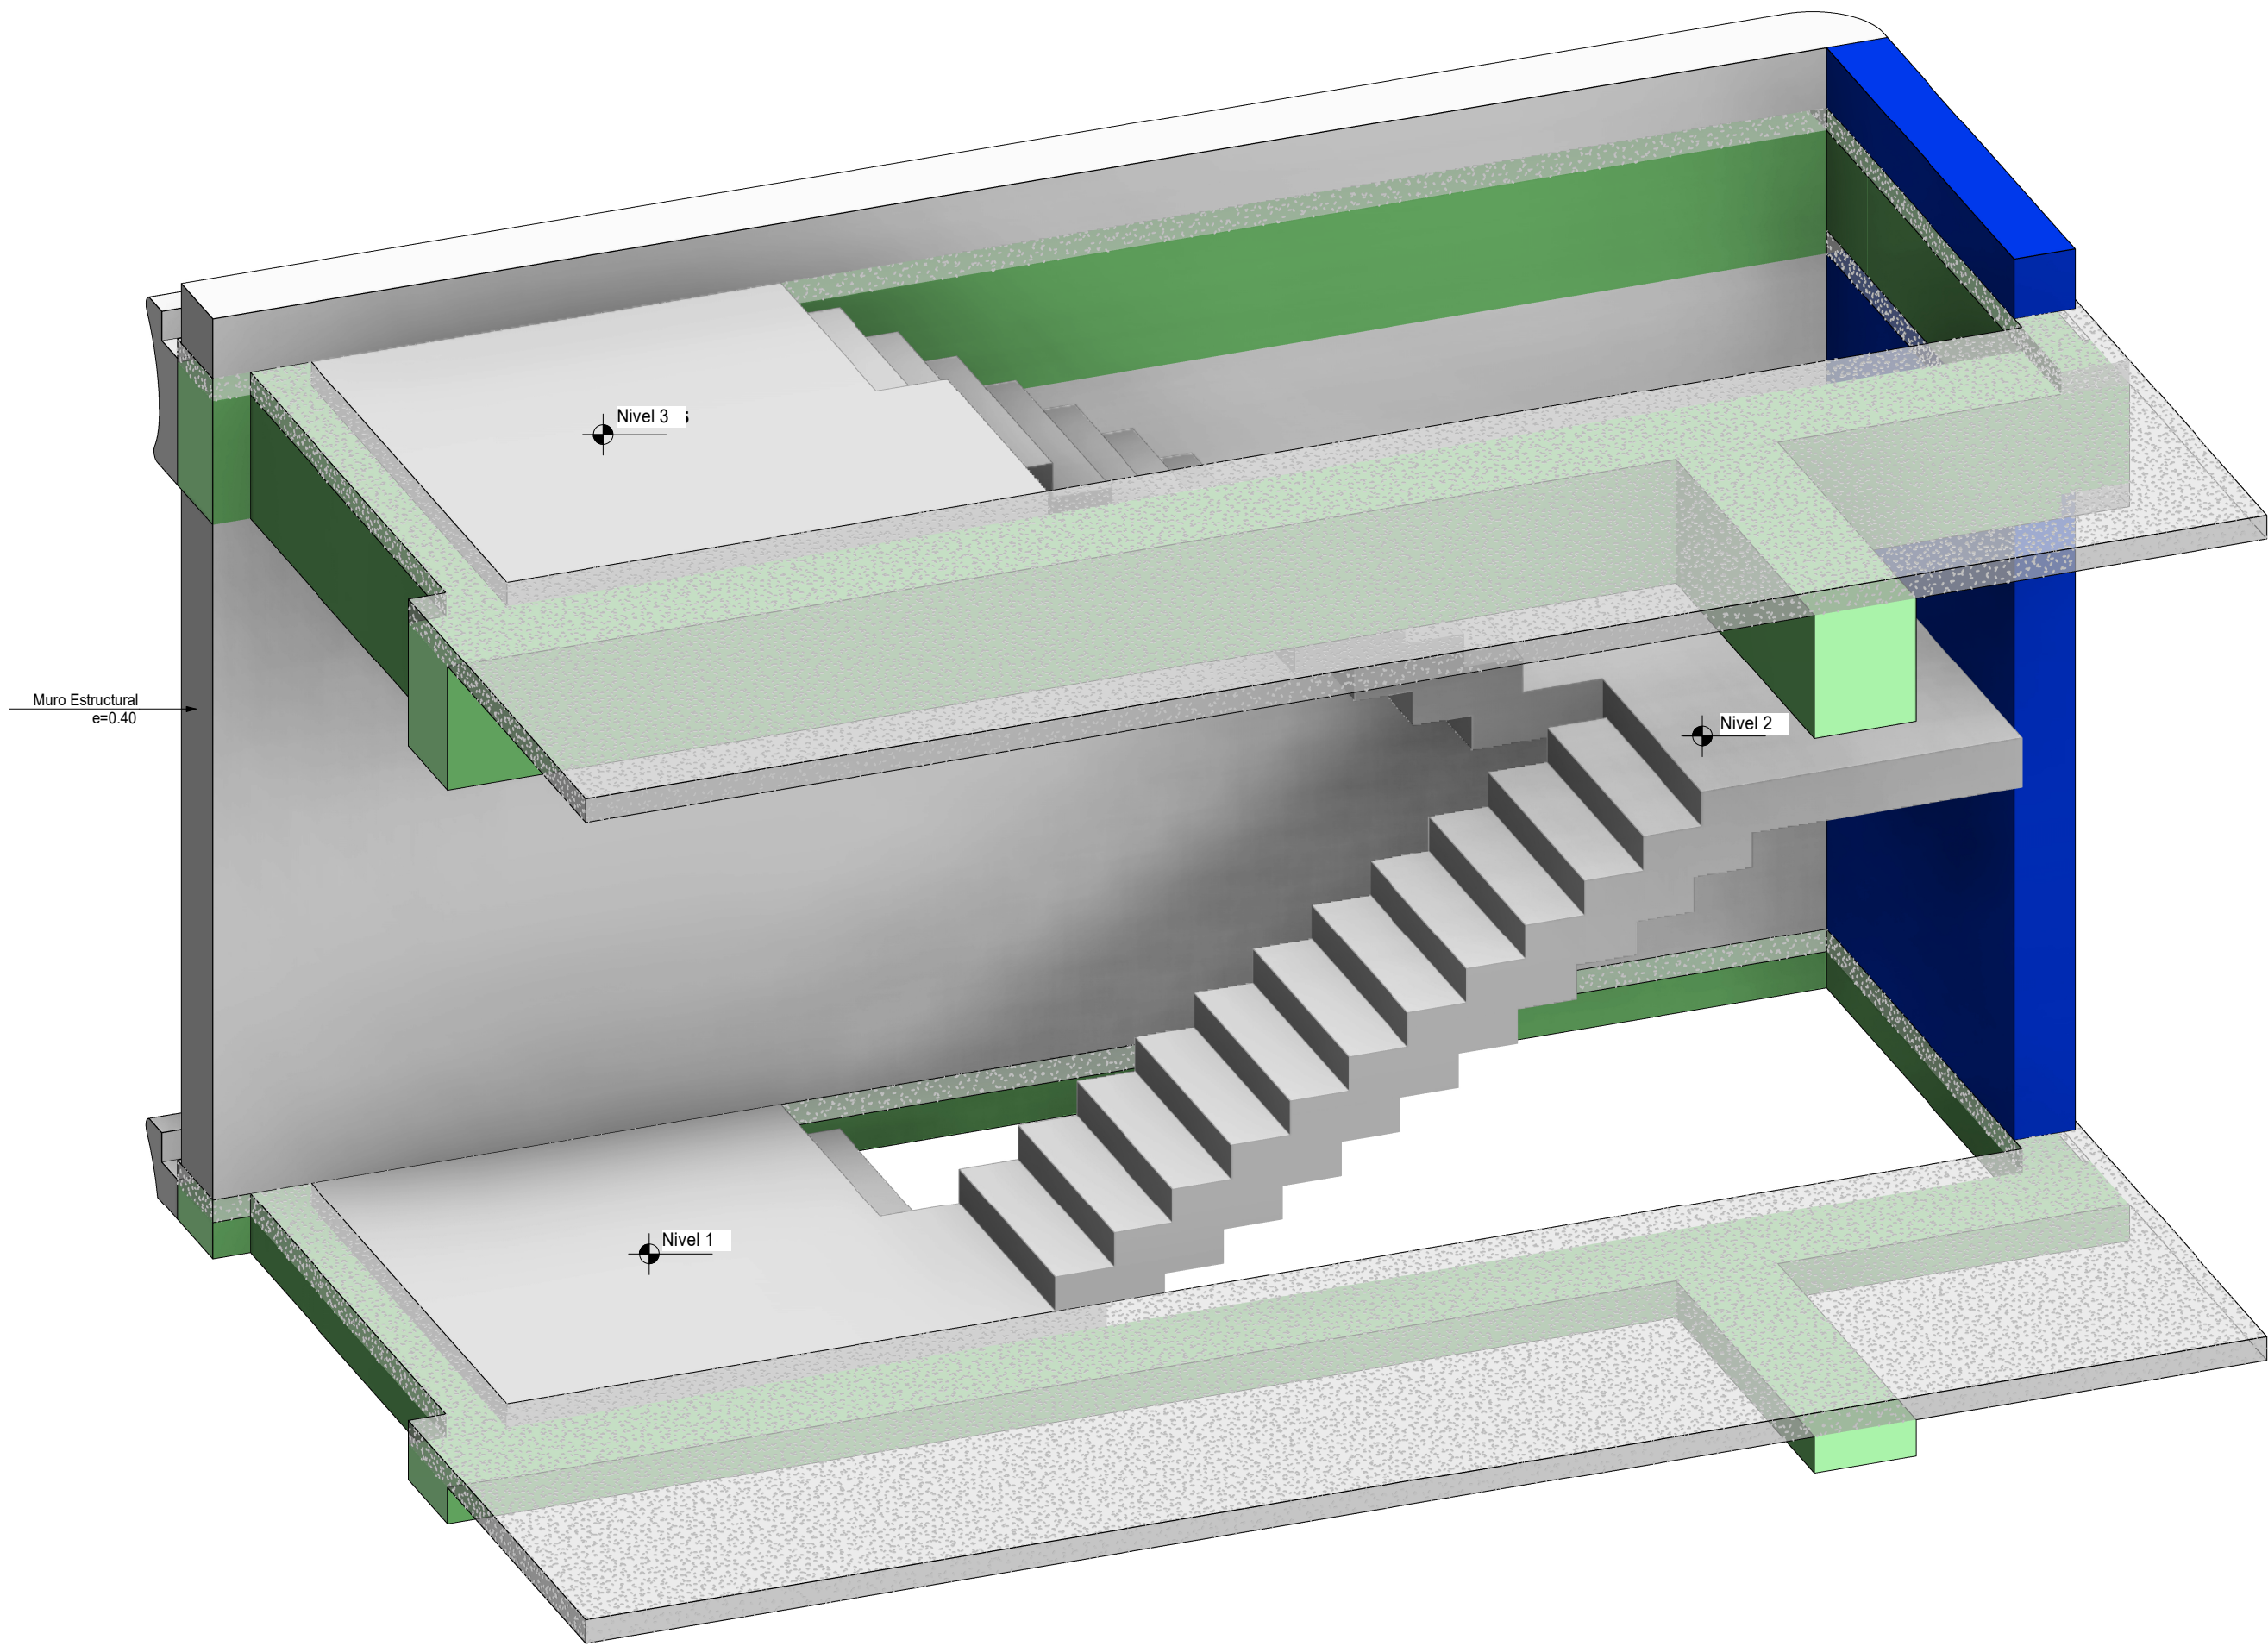

ESQUEMA 3D ESCALERA TÍPICA PISOS (2 Y 4 A CUBIERTA)
Sin escala

NIVELES ESCALERA TIPO 1 DE PISO 2 Y PISO 4 A CUBIERTA...				
Piso	NE.1	NE.2	NE.3	
PISO 2	6.25	8.35	10.45	
PISO 4	15.35	17.45	19.55	
PISO 5	19.55	21.65	23.75	
PISO 6	23.75	25.85	27.95	
PISO 7	27.95	30.05	32.15	
CUBIERTA	32.15	34.25	36.35	

#	Ø	Figuración [m]	Longitud total [m]	Peso c/varilla [kg]	Cantidad varillas	Long. todas varillas [m]	Peso Total [kg]
①	#4		10.01	9.95	9	90.08	89.58
②	#6		10.12	22.64	9	91.09	203.8
③	#3		0.56	0.31	24	13.33	7.46
④	#4		2.89	2.88	11	31.82	31.64
⑤	#6		3.1	4.82	9	27.92	43.37
⑥	#6		10.12	22.63	9	91.05	203.71
⑦	#4		10.02	9.96	9	90.14	89.63
⑧	#3		0.56	0.31	24	13.33	7.46
⑨	#6		3.1	4.82	14	43.42	67.47
⑩	#4		2.89	2.88	16	46.29	46.03
Total mass = 790 kg							

Grade	Ø	Long. todas varillas [m]	Peso Total [kg]
Gr 60	#3	26.66	14.91
Gr 60	#4	168.19	167.25
Gr 60	#5	71.34	110.85
Gr 60	#4	90.14	89.63
Gr 60	#6	182.14	407.51

NOTAS

1. Ver detalles generales en los planos PL N° 01.02 y 01.03

CONCRETO

f'c=28 MPa
f'c=280 kg/cm²
f'c=4000 psi

PLANO N° 17.05

VERSIÓN : 0



GERENTE DE PROYECTO

LUIS ENRIQUE AYCARDI F.
MAT. 2520212794 CND

INGENIERO

DANIEL E. QUICANO C.

MODELADOR

FELIPE SALINAS RODRÍGUEZ

MODIFICACIONES	FECHA
Emisión Inicial	21-11-2025

HUMANISE STUDIO

EAN-0519- AES-01-EST

Calle 71 #9-84

DESPIECE DE ESCALERA TIPO 1
TÍPICA PISOS (2 Y 4 A CUBIERTA)

EAN-0519 -AES-01-EST-PL-593 17.05

REVISOR ESTRUCTURAL

JULIO CESAR SANMIGUEL CAMACHO
MAT. 25202-57738 CND

PLANO N°

17.05

VERSIÓN :

0