


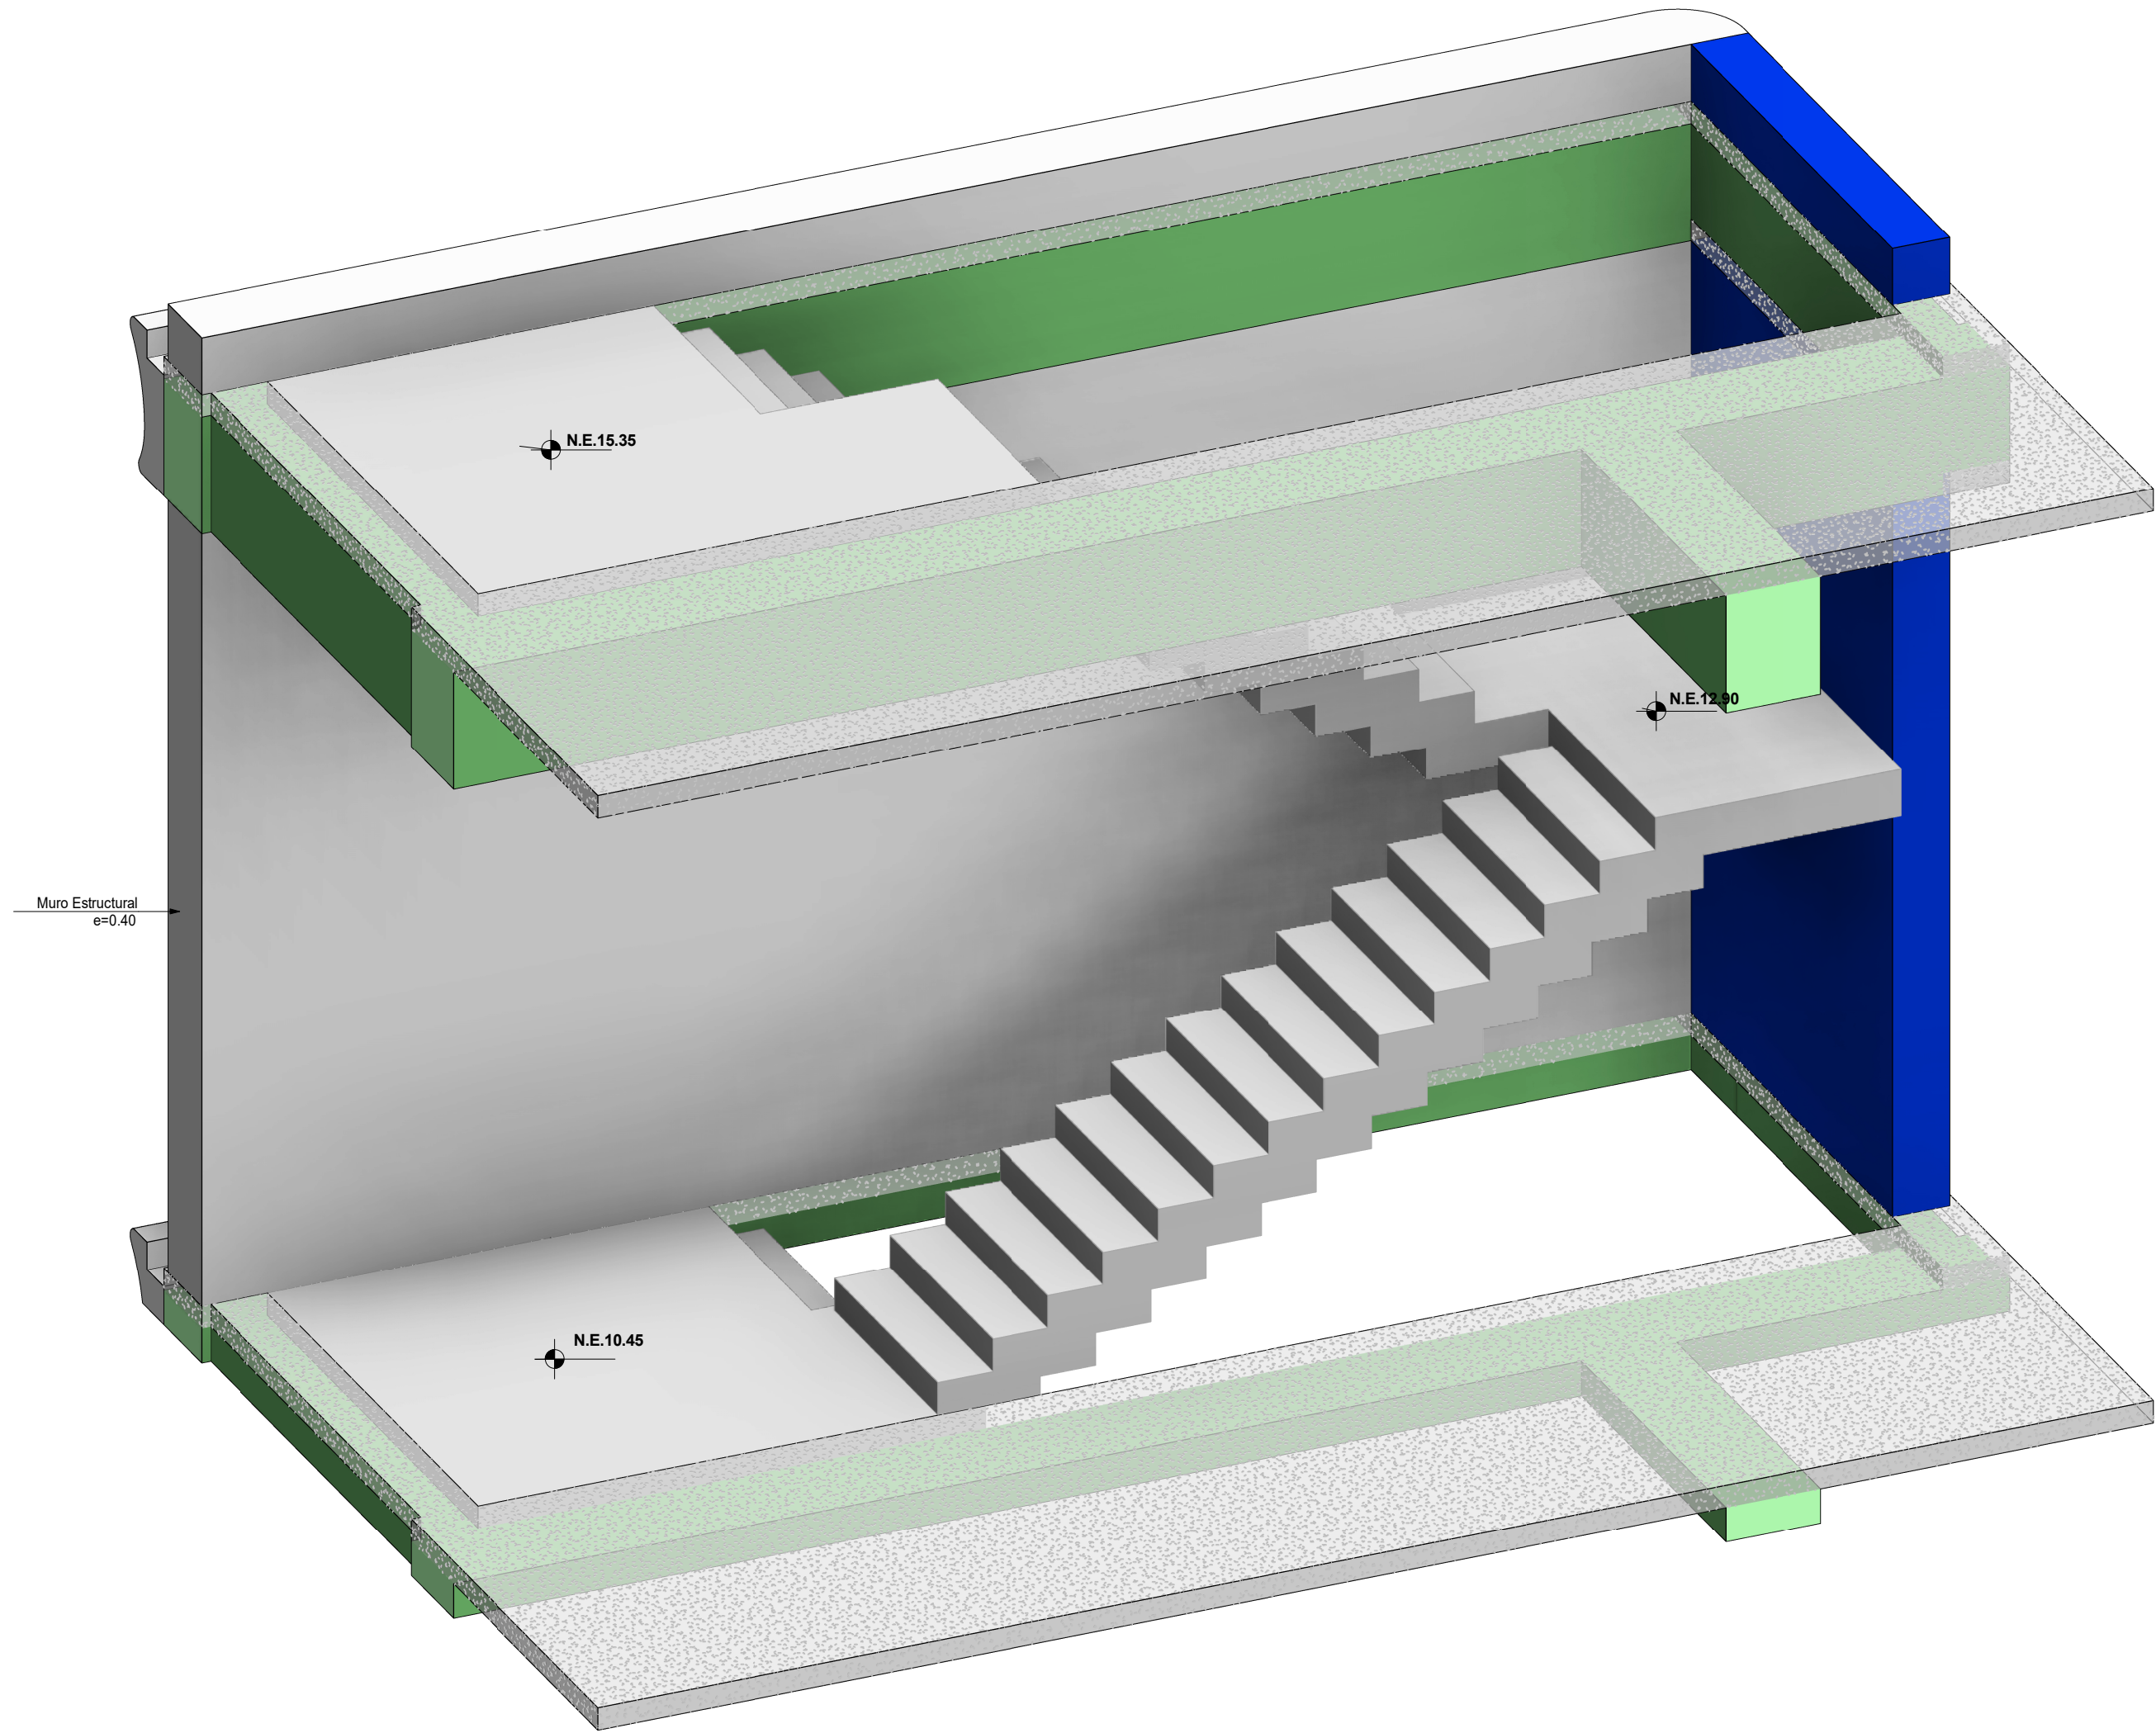

ESQUEMA 3D ESCALERA PISO 3 A PISO 4
Sin escala

#	Ø	Figuración [m]	Longitud total [m]	Peso c/varilla [kg]	Cantidad varillas	Long. todas varillas [m]	Peso Total [kg]
①	#6		10.4	23.28	9	93.63	209.5
②	#4		10.33	10.27	9	92.97	92.45
③	#3		0.56	0.31	28	15.55	8.7
④	#6		3.1	4.82	7	21.71	33.74
⑤	#4		2.89	2.88	8	23.14	23.01
⑥	#6		10.32	23.09	9	92.88	207.82
⑦	#4		10.33	10.28	9	93.01	92.49
⑧	#3		0.56	0.31	28	15.55	8.7
⑨	#6		3.1	4.82	13	40.32	62.65
⑩	#4		2.89	2.88	14	40.5	40.27
Total mass = 779 kg							

Grade	Ø	Long. todas varillas [m]	Peso Total [kg]
Gr 60	#3	31.1	17.4
Gr 60	#4	249.62	248.23
Gr 60	#5	62.03	96.39
Gr 60	#6	186.52	417.32

CONCRETO

f'c=28 MPa
f'c=280 kg/cm²
f'c=4000 psi

NOTAS
1. Ver detalles generales en los planos PL N° 01.02 y 01.03

PLANO N°17.07

VERSIÓN :0

AycardiEstructural

GERENTE DE PROYECTO
LUIS ENRIQUE AYCARDI F.
MAT. 2520212794 CND

INGENIERO
DANIEL E. QUICANO C.

MODELADOR
FELIPE SALINAS RODRÍGUEZ

MODIFICACIONES

FECHA

Emisión Inicial	21-11-2025

HUMANISE STUDIO

EAN-0519- AES-01-EST

Calle 71 #9-84

DESPIECE DE ESCALERA TIPO 1 DE
PISO 3 A PISO 4

EAN-0519 -AES-01-EST-PL-595 17.07

REVISOR ESTRUCTURAL
JULIO CESAR SANMIGUEL CAMACHO
MAT. 25202-57738 CND

PLANO N°17.07

VERSIÓN :0

