


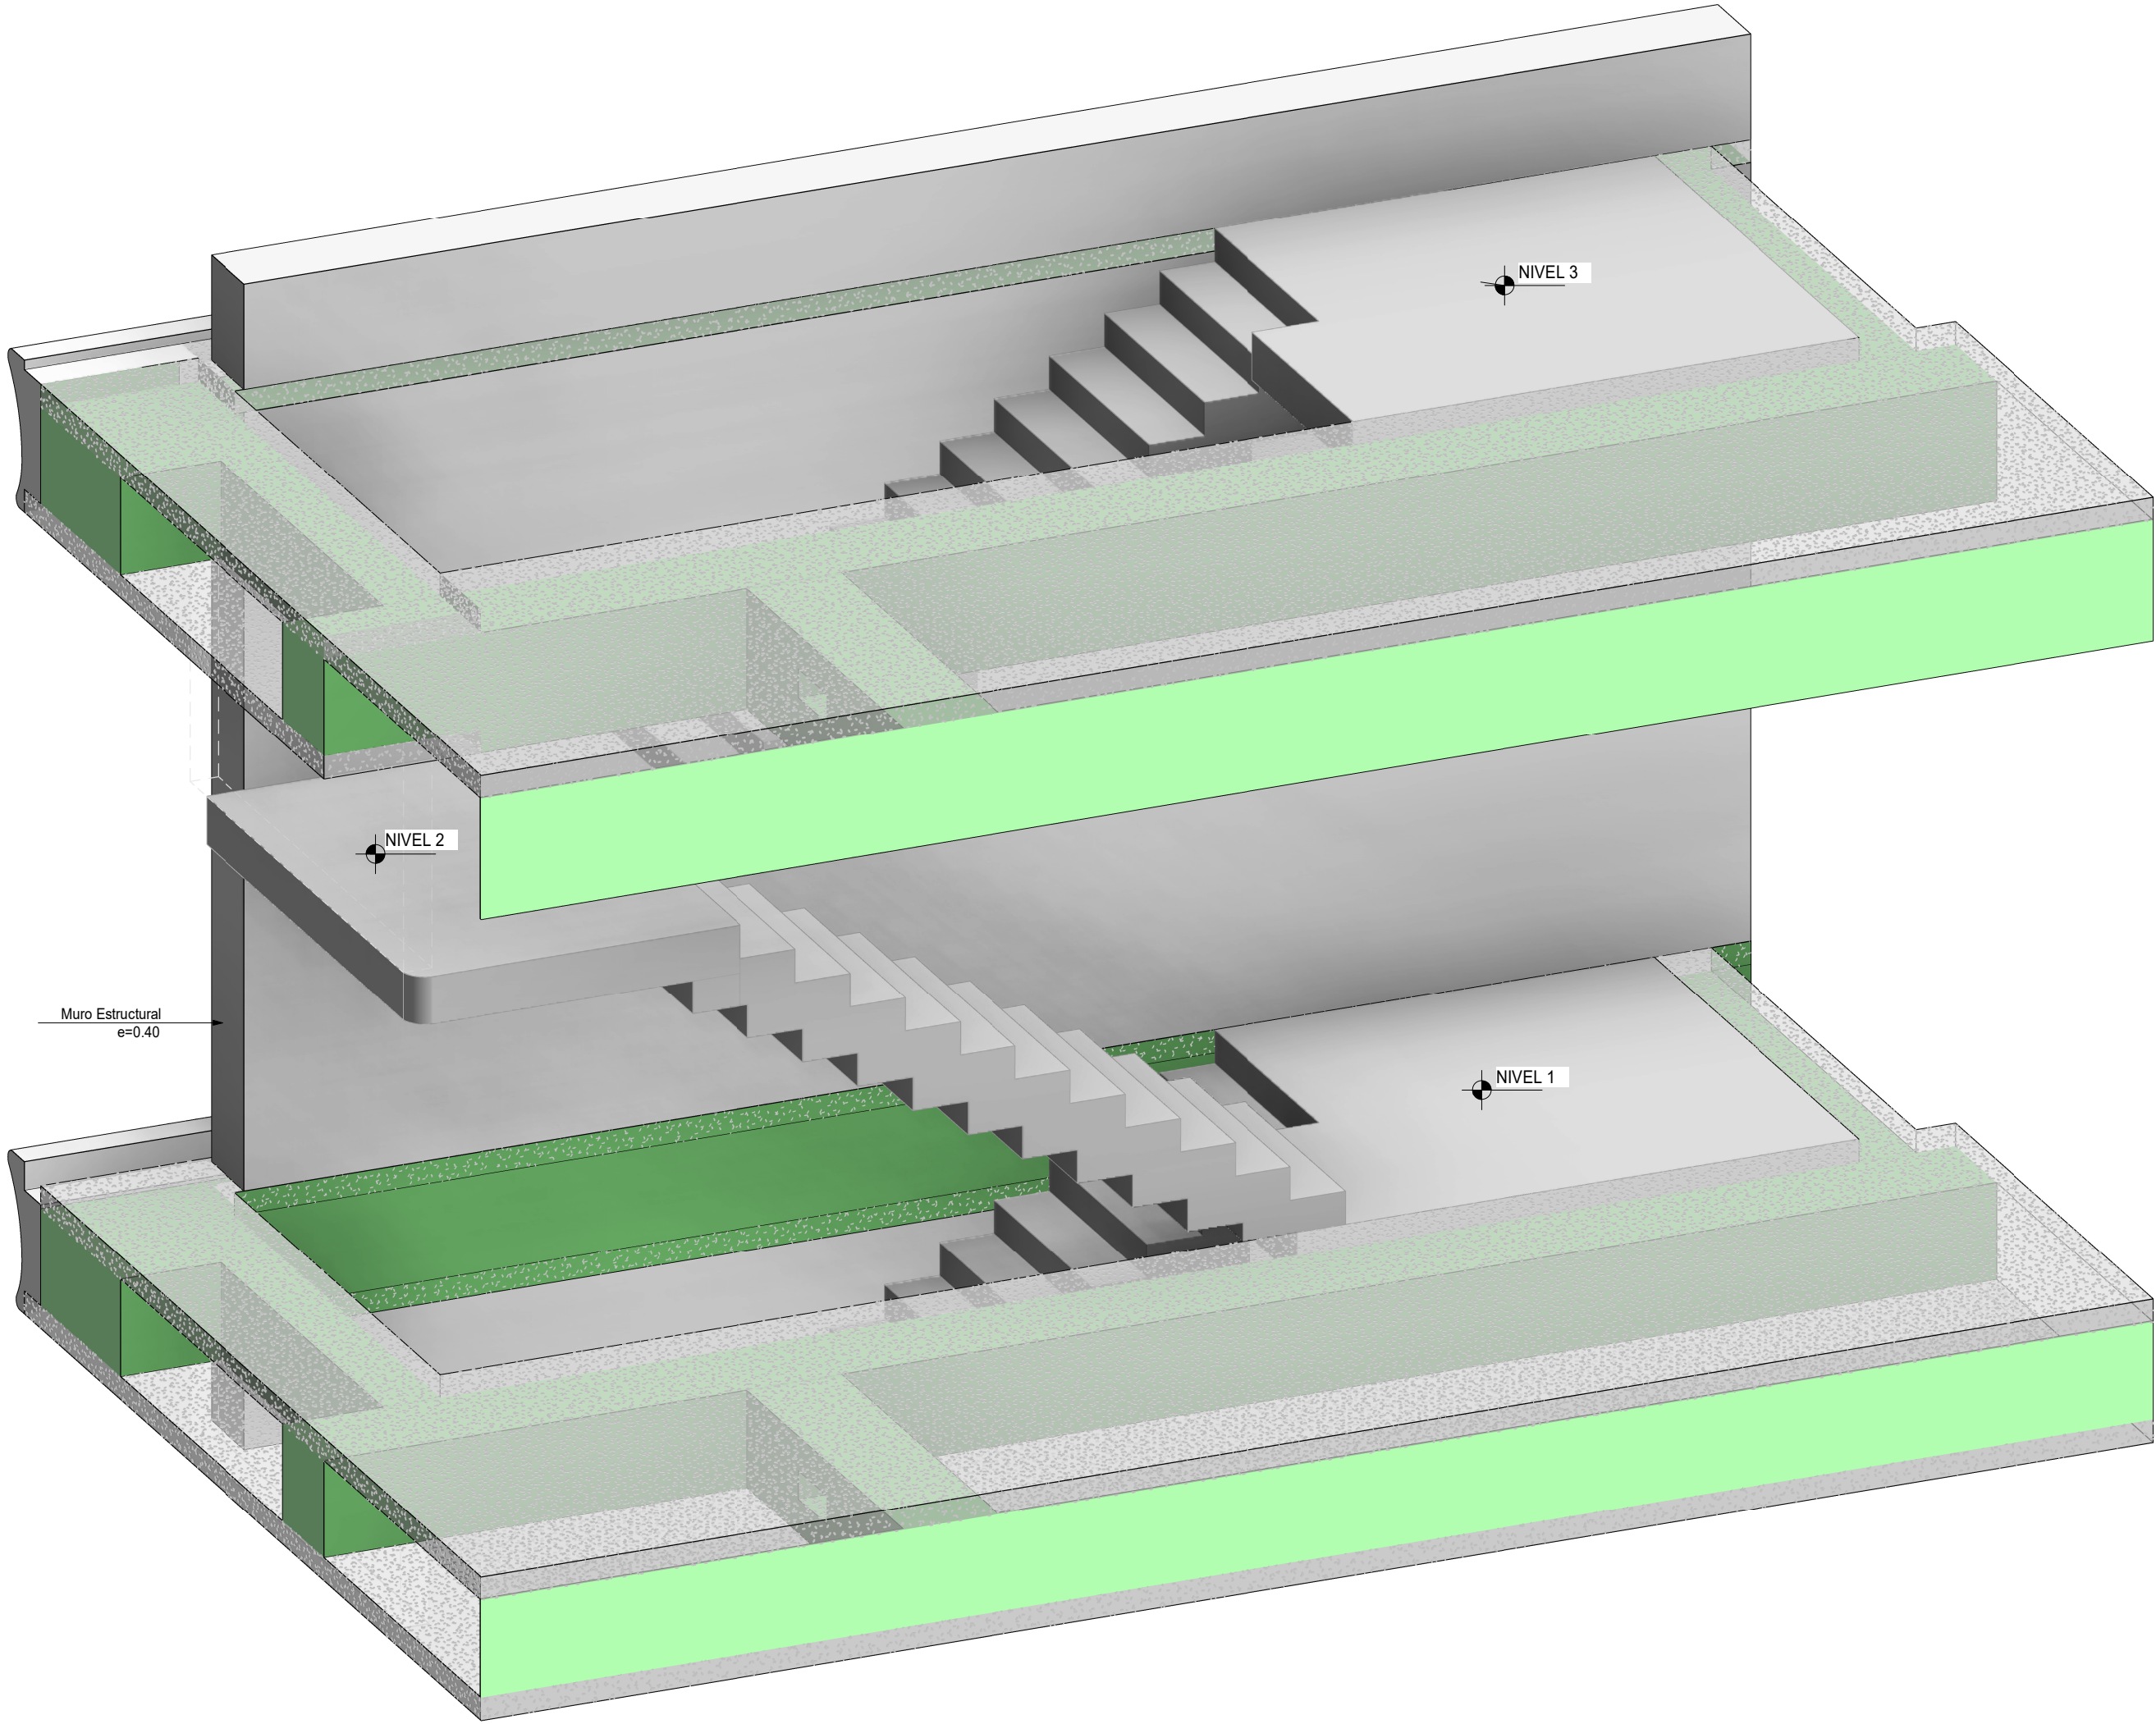

ESQUEMA 3D ESCALERA TIPO 2 PISO 2 A PISO 3
Sin escala

#	Ø	Figuración [m]	Longitud total [m]	Peso c/varilla [kg]	Cantidad varillas	Long. todas varillas [m]	Peso Total [kg]
①	#4		10.17	10.11	9	91.55	91.03
②	#6		10.33	23.1	9	92.93	207.92
③	#3		0.56	0.31	216	119.97	67.1
⑤	#6		3.51	7.85	9	31.59	70.68
⑥	#4		2.89	2.87	12	34.68	34.48
⑦	#6		3.1	4.81	10	30.99	48.14
⑧	#4		10.16	10.11	9	91.47	90.96
⑨	#6		10.22	22.88	9	92.02	205.88
⑩	#3		0.56	0.31	216	119.97	67.1
⑪	#6		3.51	7.85	9	31.59	70.68
⑫	#4		2.89	2.87	14	40.46	40.23
⑬	#6		3.1	4.81	14	43.38	67.4
⑮	#5		3.1	4.81	14	43.38	67.4
⑯	#4		2.89	2.87	16	46.24	45.98
Total mass = 1175 kg							

Grade	Ø	Long. todas varillas [m]	Peso Total [kg]
Gr 60	#3	239.93	134.21
Gr 60	#4	304.39	302.69
Gr 60	#5	117.74	182.95
Gr 60	#6	248.13	555.16

CONCRETO

f'c=28 MPa
f'c=280 kg/cm²
f'c=4000 psi

NOTAS

1. Ver detalles generales en los planos PL N° 01.02 y 01.03

PLANO N° 17.11

VERSIÓN : 0



GERENTE DE PROYECTO
LUIS ENRIQUE AYCARDI F.
MAT. 2520212794 CND

INGENIERO
DANIEL E. QUICANO C.

MODELADOR
FELIPE SALINAS RODRÍGUEZ

MODIFICACIONES	FECHA
Emisión Inicial	21-11-2025

HUMANISE STUDIO

EAN-0519- AES-01-EST

Calle 71 #9-84

DESPIECE DE ESCALERA TIPO 2 PISO 2 A PISO 3

EAN-0519 -AES-01-EST-PL-599 17.11

REVISOR ESTRUCTURAL
JULIO CESAR SANMIGUEL CAMACHO
MAT. 25202-57738 CND

PLANO N°

17.11

VERSIÓN :

0

