



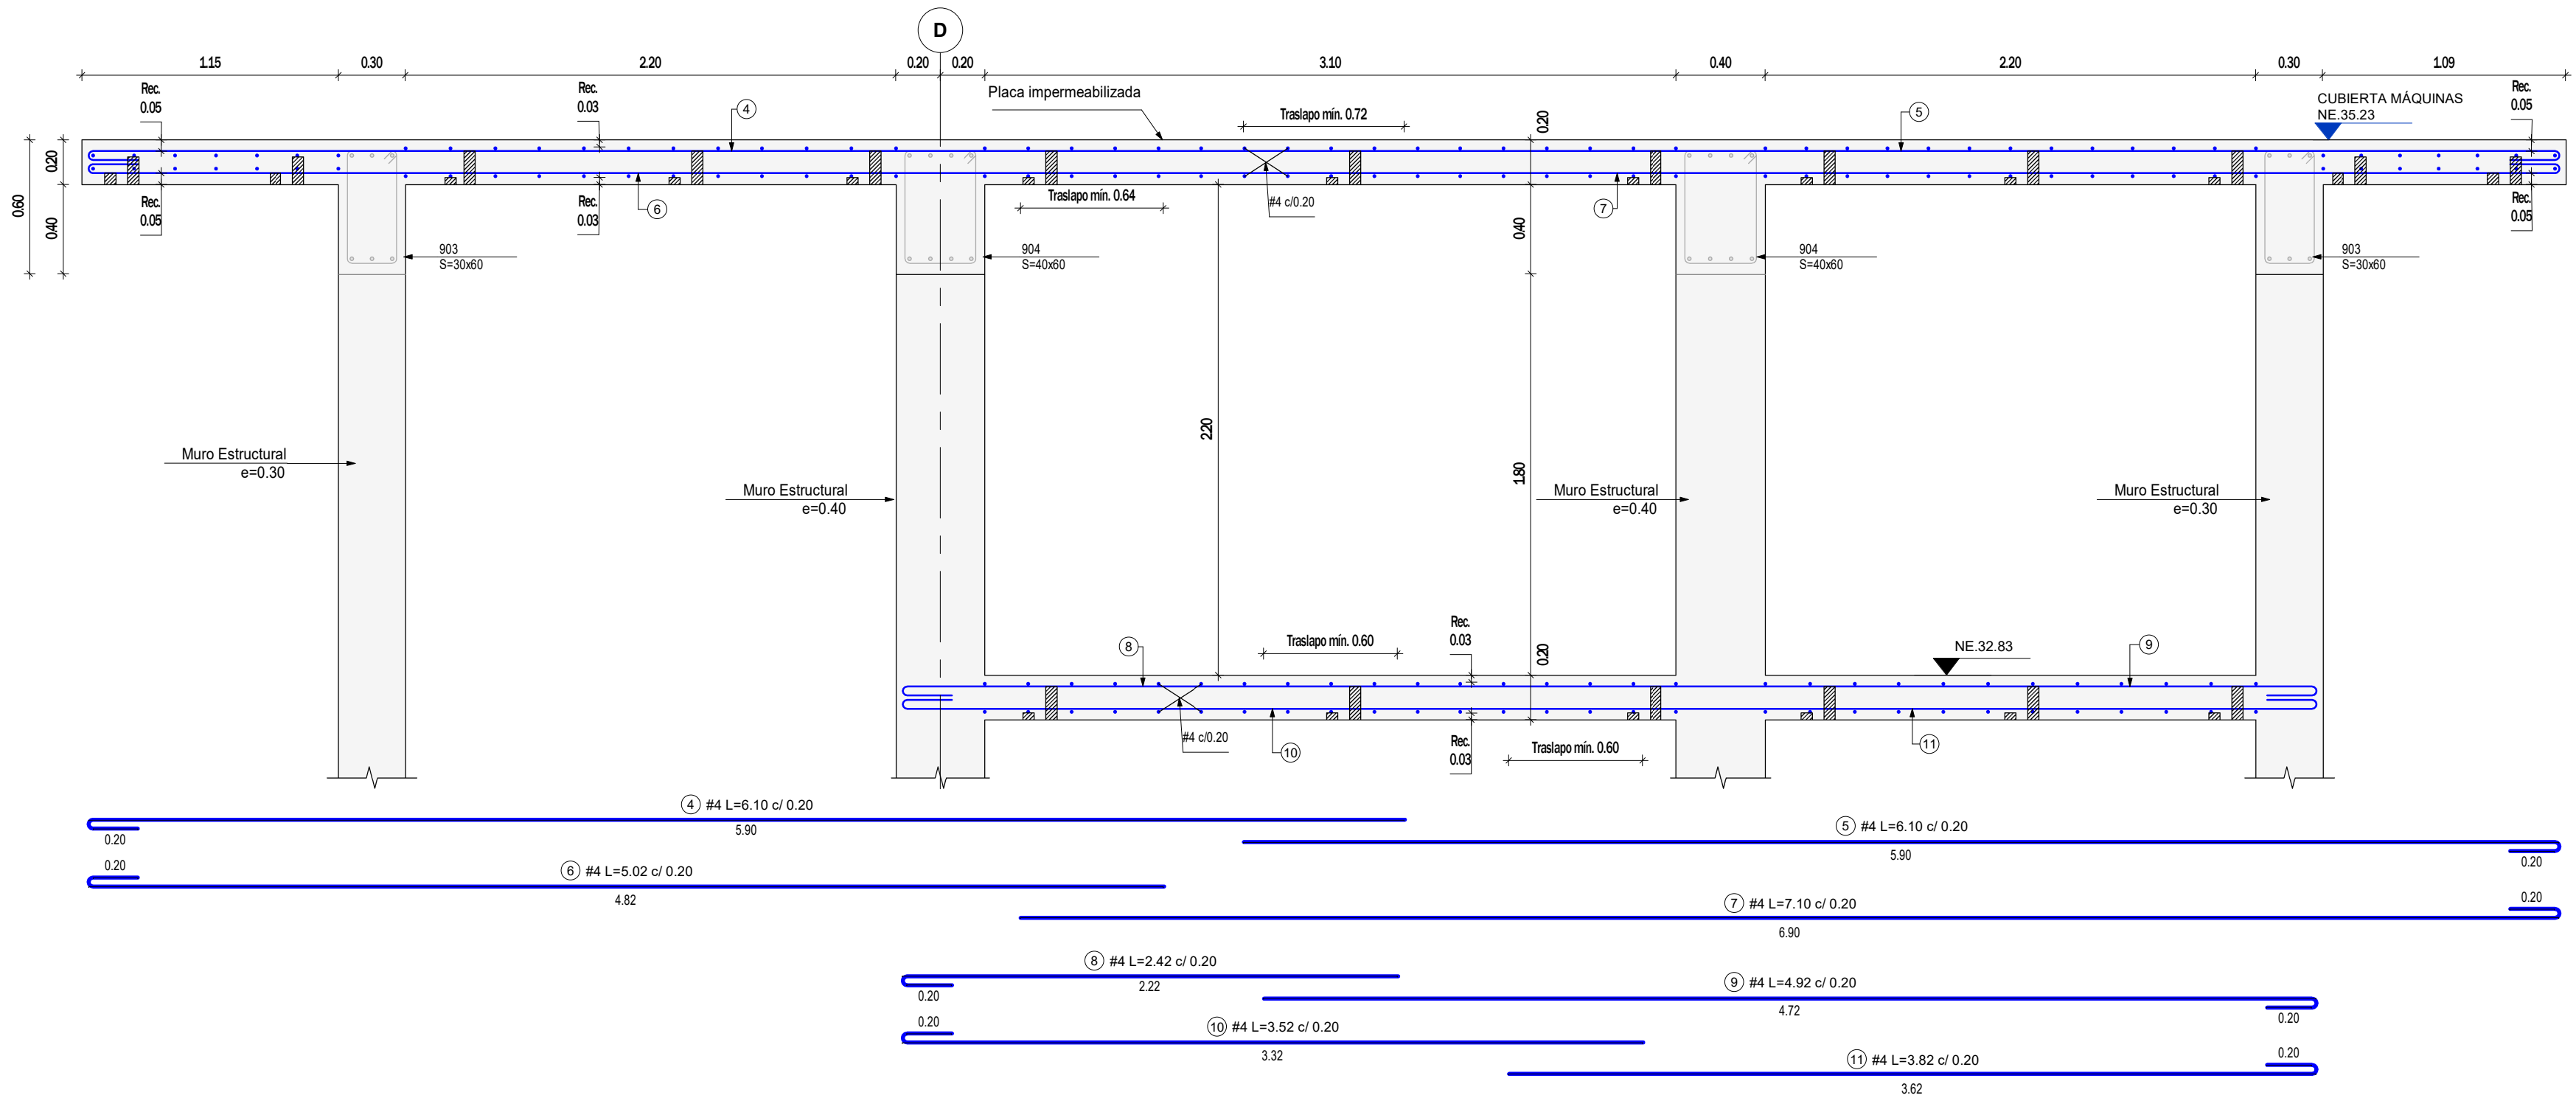


Es obligatorio el uso de separadores, sillotas ó soportes para garantizar la correcta posición del refuerzo.

CORTE 2 - 2
Escala 1 : 25

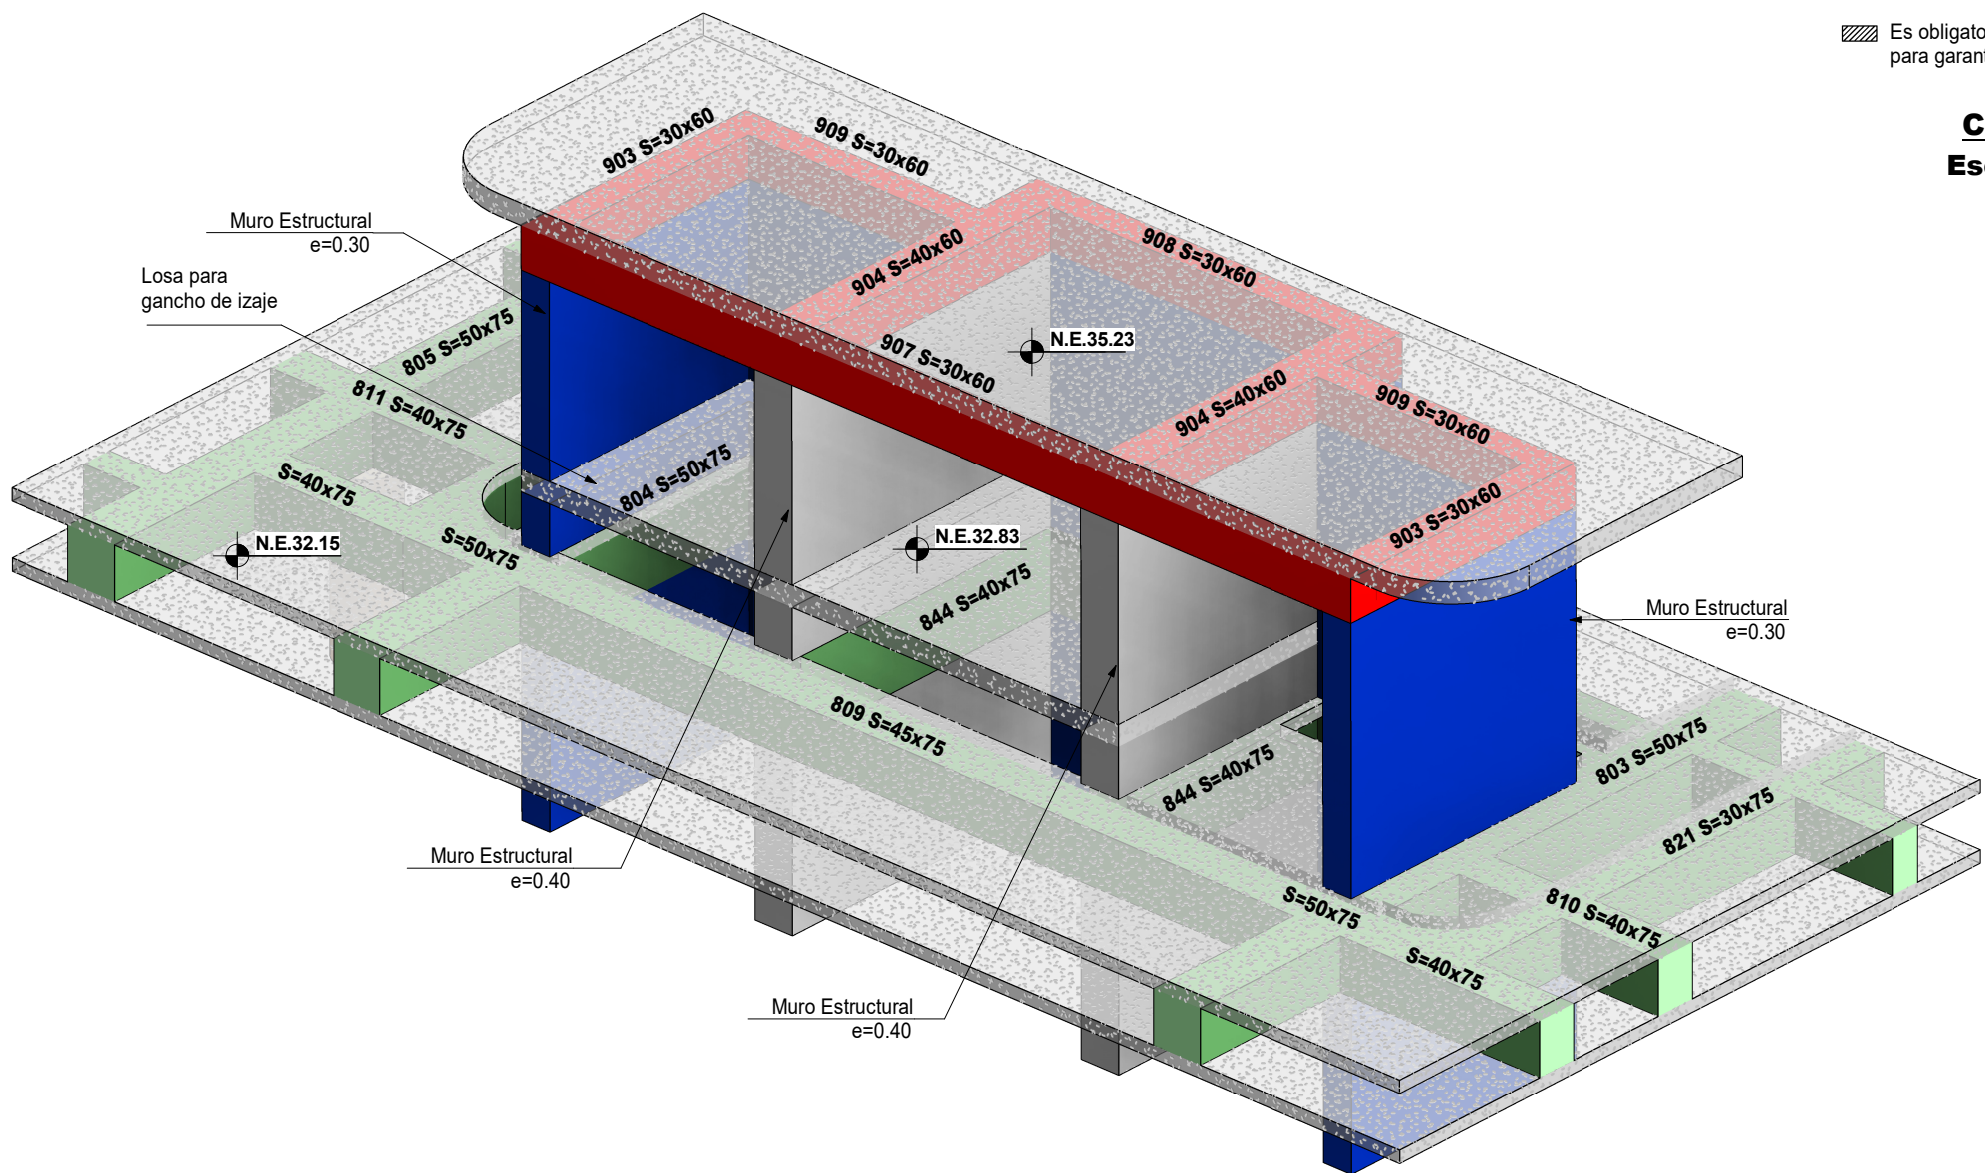

ESQUEMA 3D CUBIERTA ASCENSORES
Sin escala

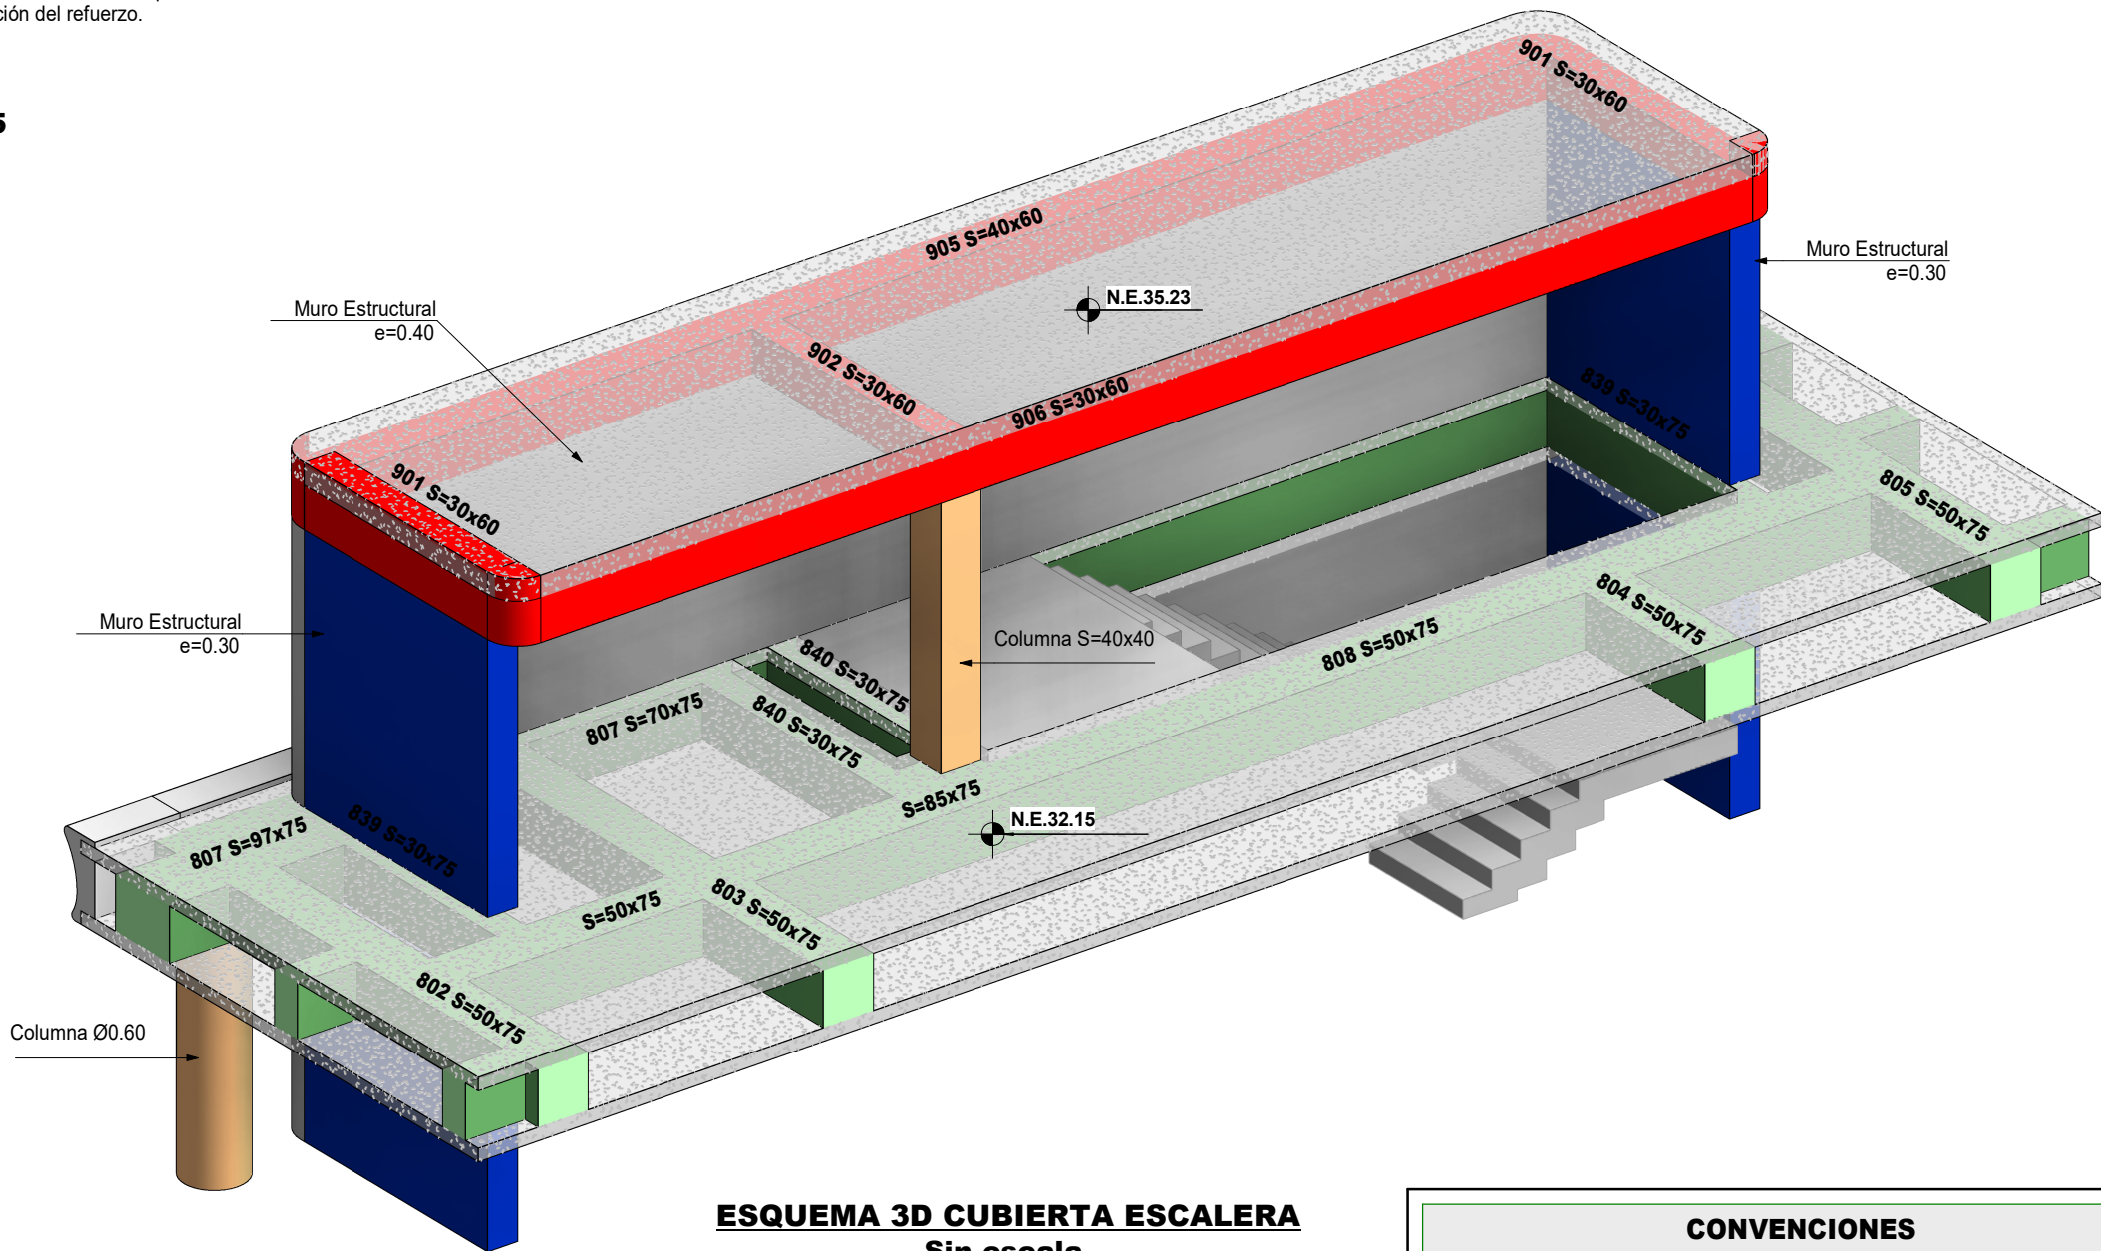

ESQUEMA 3D CUBIERTA ESCALERA
Sin escala

CONCRETO
f'c=35 MPa
f'c=350 kg/cm²
f'c=5000 psi

CONVENCIONES

- Indica columna
- Indica muro e=30
- Indica muro e=40
- Indica viga h=60

NOTAS

- Ver detalles generales en el PL N° 01.02 y 01.03
- Ver planta de cubierta de máquinas en el PL N° 15.02
- Ver despieces de vigas en los PL N° 15.02
- Se debe garantizar un tiempo mínimo de curado intensivo de por lo menos 15 días
- Debe estudiarse e implementar algún sistema de aislamiento térmico de la losa de concreto

PLANO N° **15.01**

VERSIÓN : **0**



GERENTE DE PROYECTO
LUIS ENRIQUE AYCARDI F.
MAT. 2520212794 CND

INGENIERO
DANIEL E. QUICANO C.

MODELADOR
PAULA ANDREA MONTOYA RENDÓN

MODIFICACIONES	FECHA
Emisión Inicial	21-11-2025

HUMANISE STUDIO

EAN-0519- AES-01-EST

Calle 71 #9-84

CORTE Y ESQUEMA 3D CUBIERTA DE MÁQUINAS

EAN-0519- AES-01-EST-SCU-PL-579 15.01

REVISOR ESTRUCTURAL
JULIO CESAR SANMIGUEL CAMACHO
MAT. 25202-57738 CND

PLANO N° **15.01** VERSIÓN : **0**